


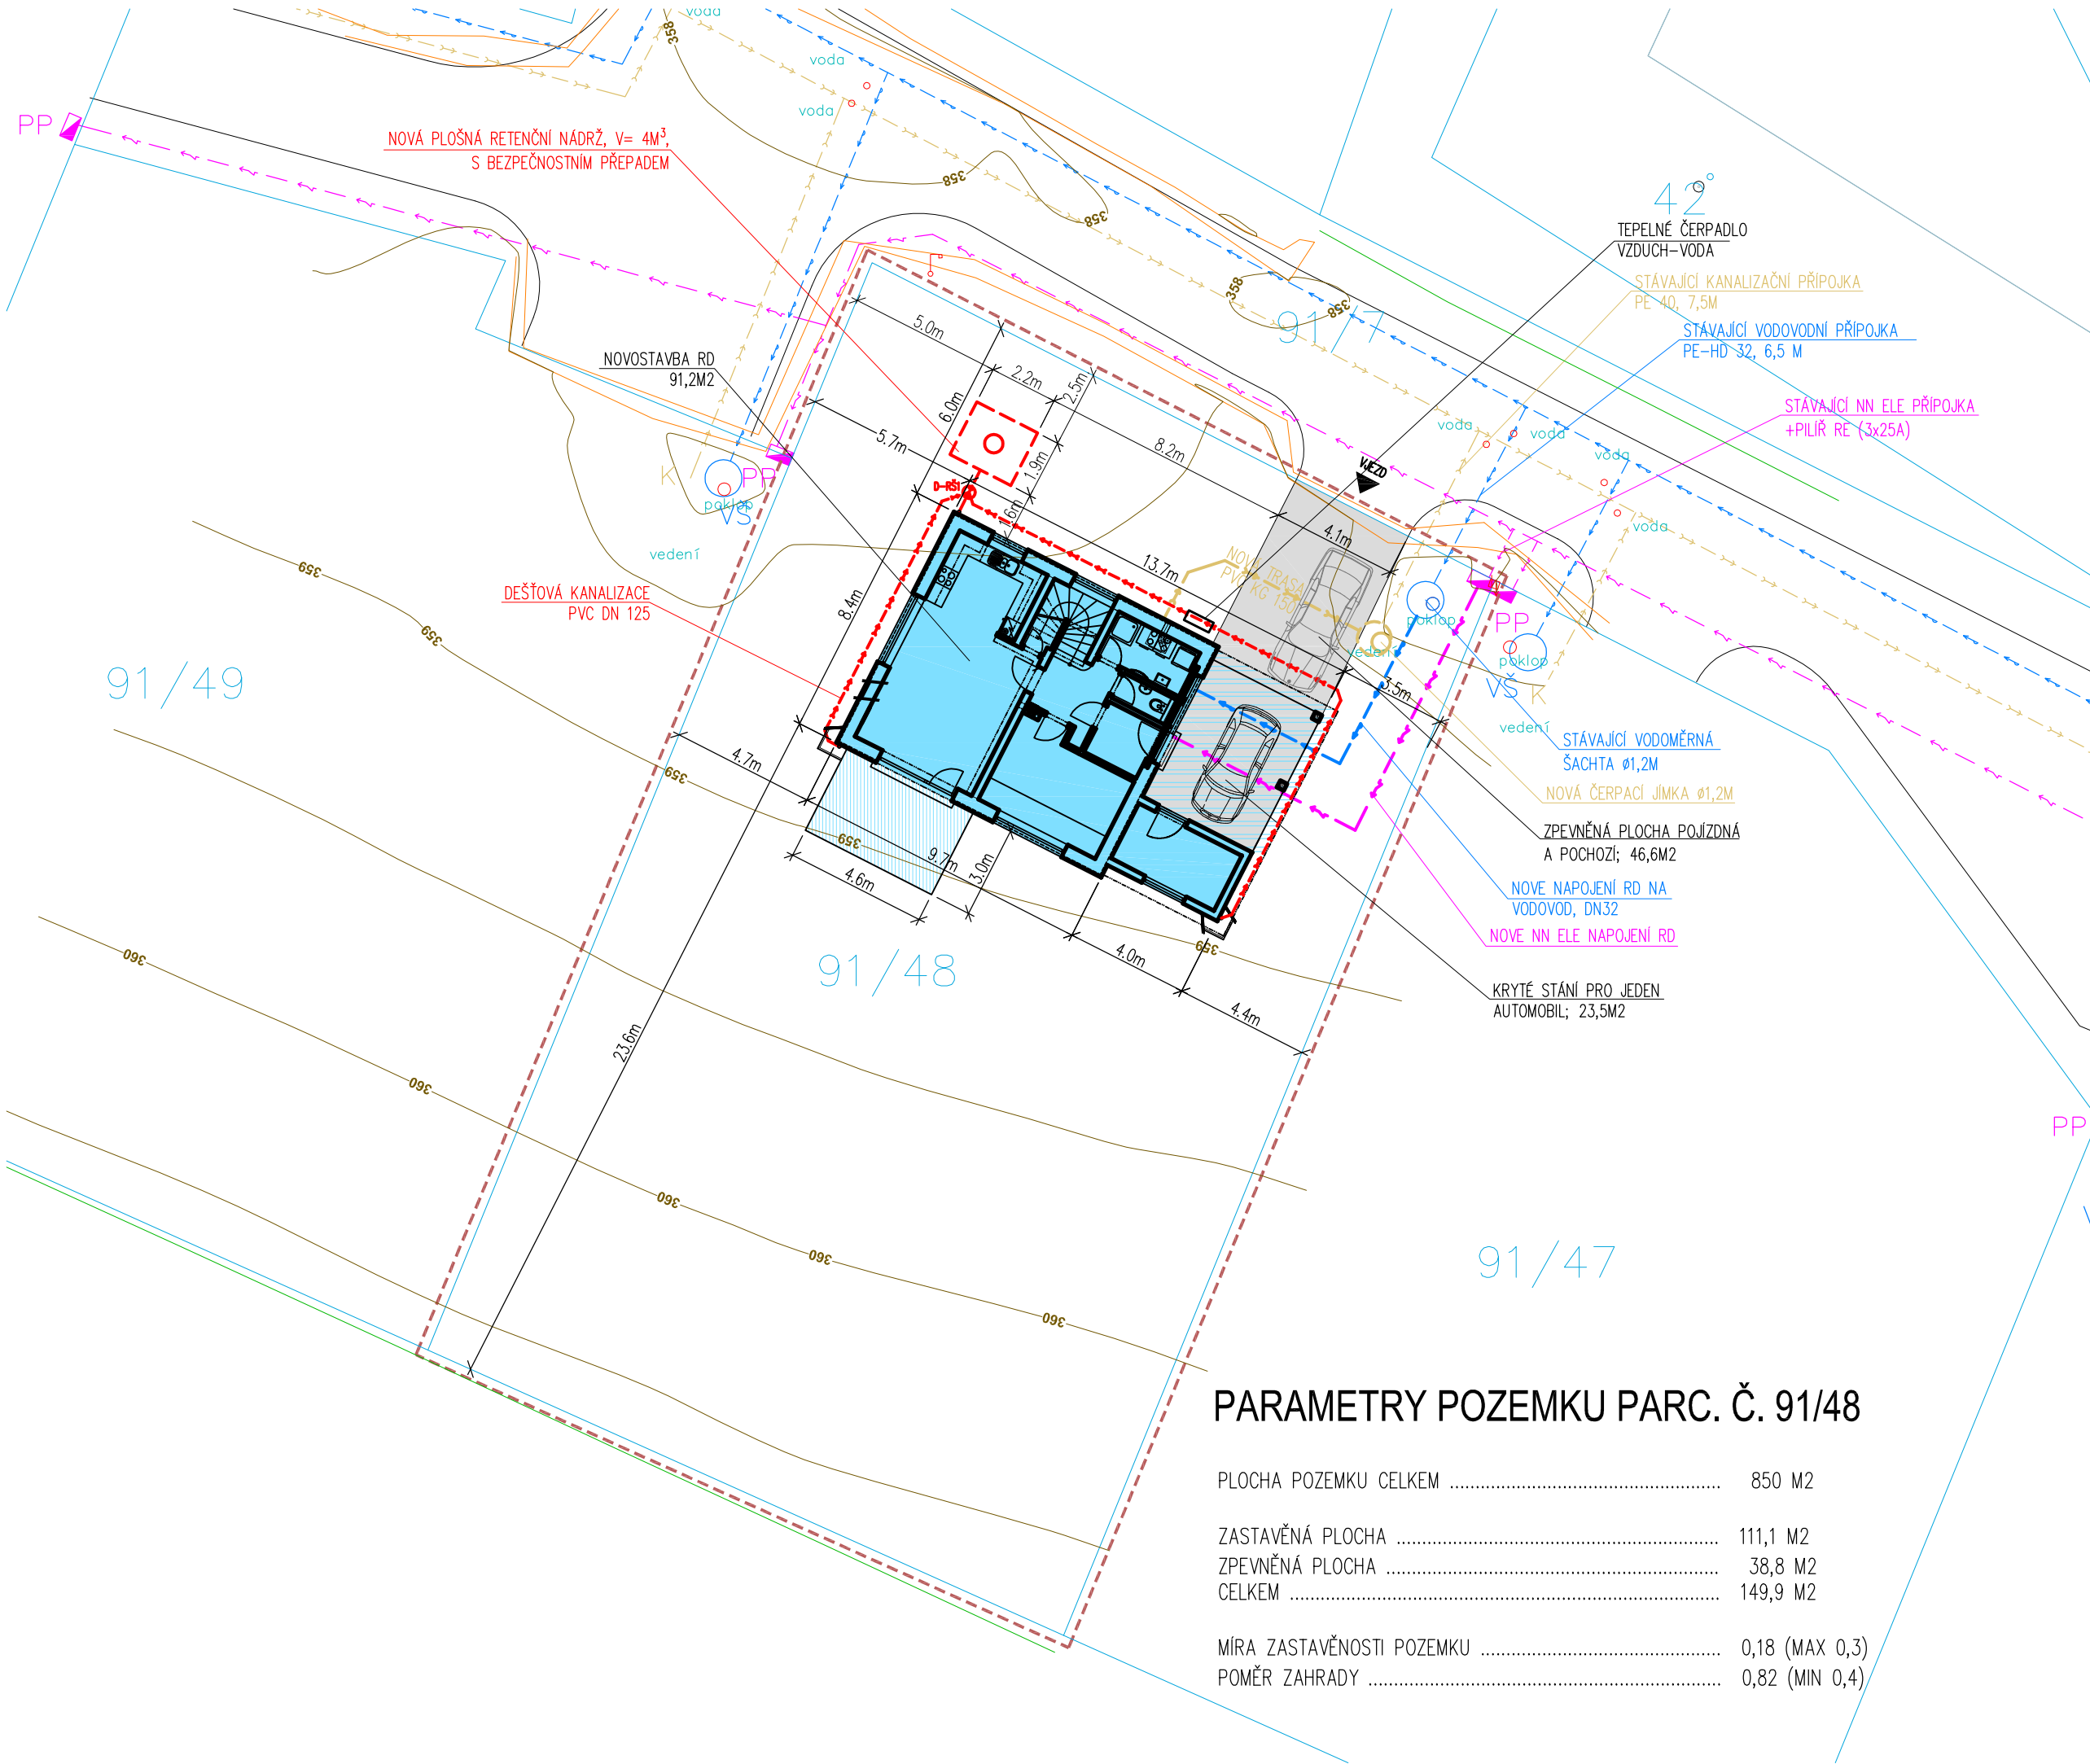

LEGENDA


- NOVÝ OBJEKT RD
- NOVÝ OBJEKT – KRYTÉ STÁNÍ
- NOVÝ OBJEKT – TERASA
- HRANICE KATASTRU
- ŘEŠENÉ ÚZEMÍ
- NOVÉ ZPEVNĚNÉ PLOCHY

INŽENÝRSKE SÍŤ – STÁVAJÍCÍ

- VODOVOD
- SILNOPROUD
- SPLAŠKOVÁ KANALIZACE

INŽENÝRSKE SÍŤ – NOVÉ

- VODOVOD
- KANALIZACE – SPLAŠKOVÁ
- KANALIZACE – DEŠŤOVÁ
- SILNOPROUD

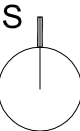

± 0.000 = 359,200 m n.m. (BpV)

Tato dokumentace je duševním vlastnictvím f. PÍSEK SEYČEK ARCHITEKTI s.r.o.

STUPĚŇ:		DOKUMENTACE PRO SPOLEČNÉ ŘÍZENÍ	
Č. ZAKÁZKY:		PARÉ:	
DATUM: PROSINEC 2021			
MĚŘITKO: 1:200			
FORMÁT: 2xA4			
ZODPOVĚDNÝ PROJEKTANT		 písek seyček architekti	
ING. ARCH. JAN SEYČEK		PÍSEK SEYČEK ARCHITEKTI S.R.O. KRAŠOVA 749/17, 130 00 PRAHA 3 TEL: +420 774 627 114, +420 606 427 854	
VYPRACOVAL		PÍSEK SEYČEK ARCHITEKTI S.R.O. KRAŠOVA 749/17, 130 00 PRAHA 3 TEL: +420 774 627 114, +420 606 427 854	
ING. JIŘÍ KLOFÁK			
INVESTOR:		EKATERINA MATVEEVA U SILOVANKY 2440/5C, 182 00, PRAHA	
STAVBA:		RODINNÝ DŮM "BEÁTA" K.Ú. VELKÁ HRAŠTICE PARC.Č. 91/48	
ČÁST DOKUMENTACE:		Č. ČÁSTI:	
KOORDINAČNÍ SITUACE		C.3	
NÁZEV VÝKRESU:		Č. VÝKRESU:	
-		-	

PARAMETRY POZEMKU PARC. Č. 91/48

PLOCHA POZEMKU CELKEM	850 M2
ZASTAVĚNÁ PLOCHA	111,1 M2
ZPEVNĚNÁ PLOCHA	38,8 M2
CELKEM	149,9 M2
MÍRA ZASTAVĚNOSTI POZEMKU	0,18 (MAX 0,3)
POMĚR ZAHRADY	0,82 (MIN 0,4)