


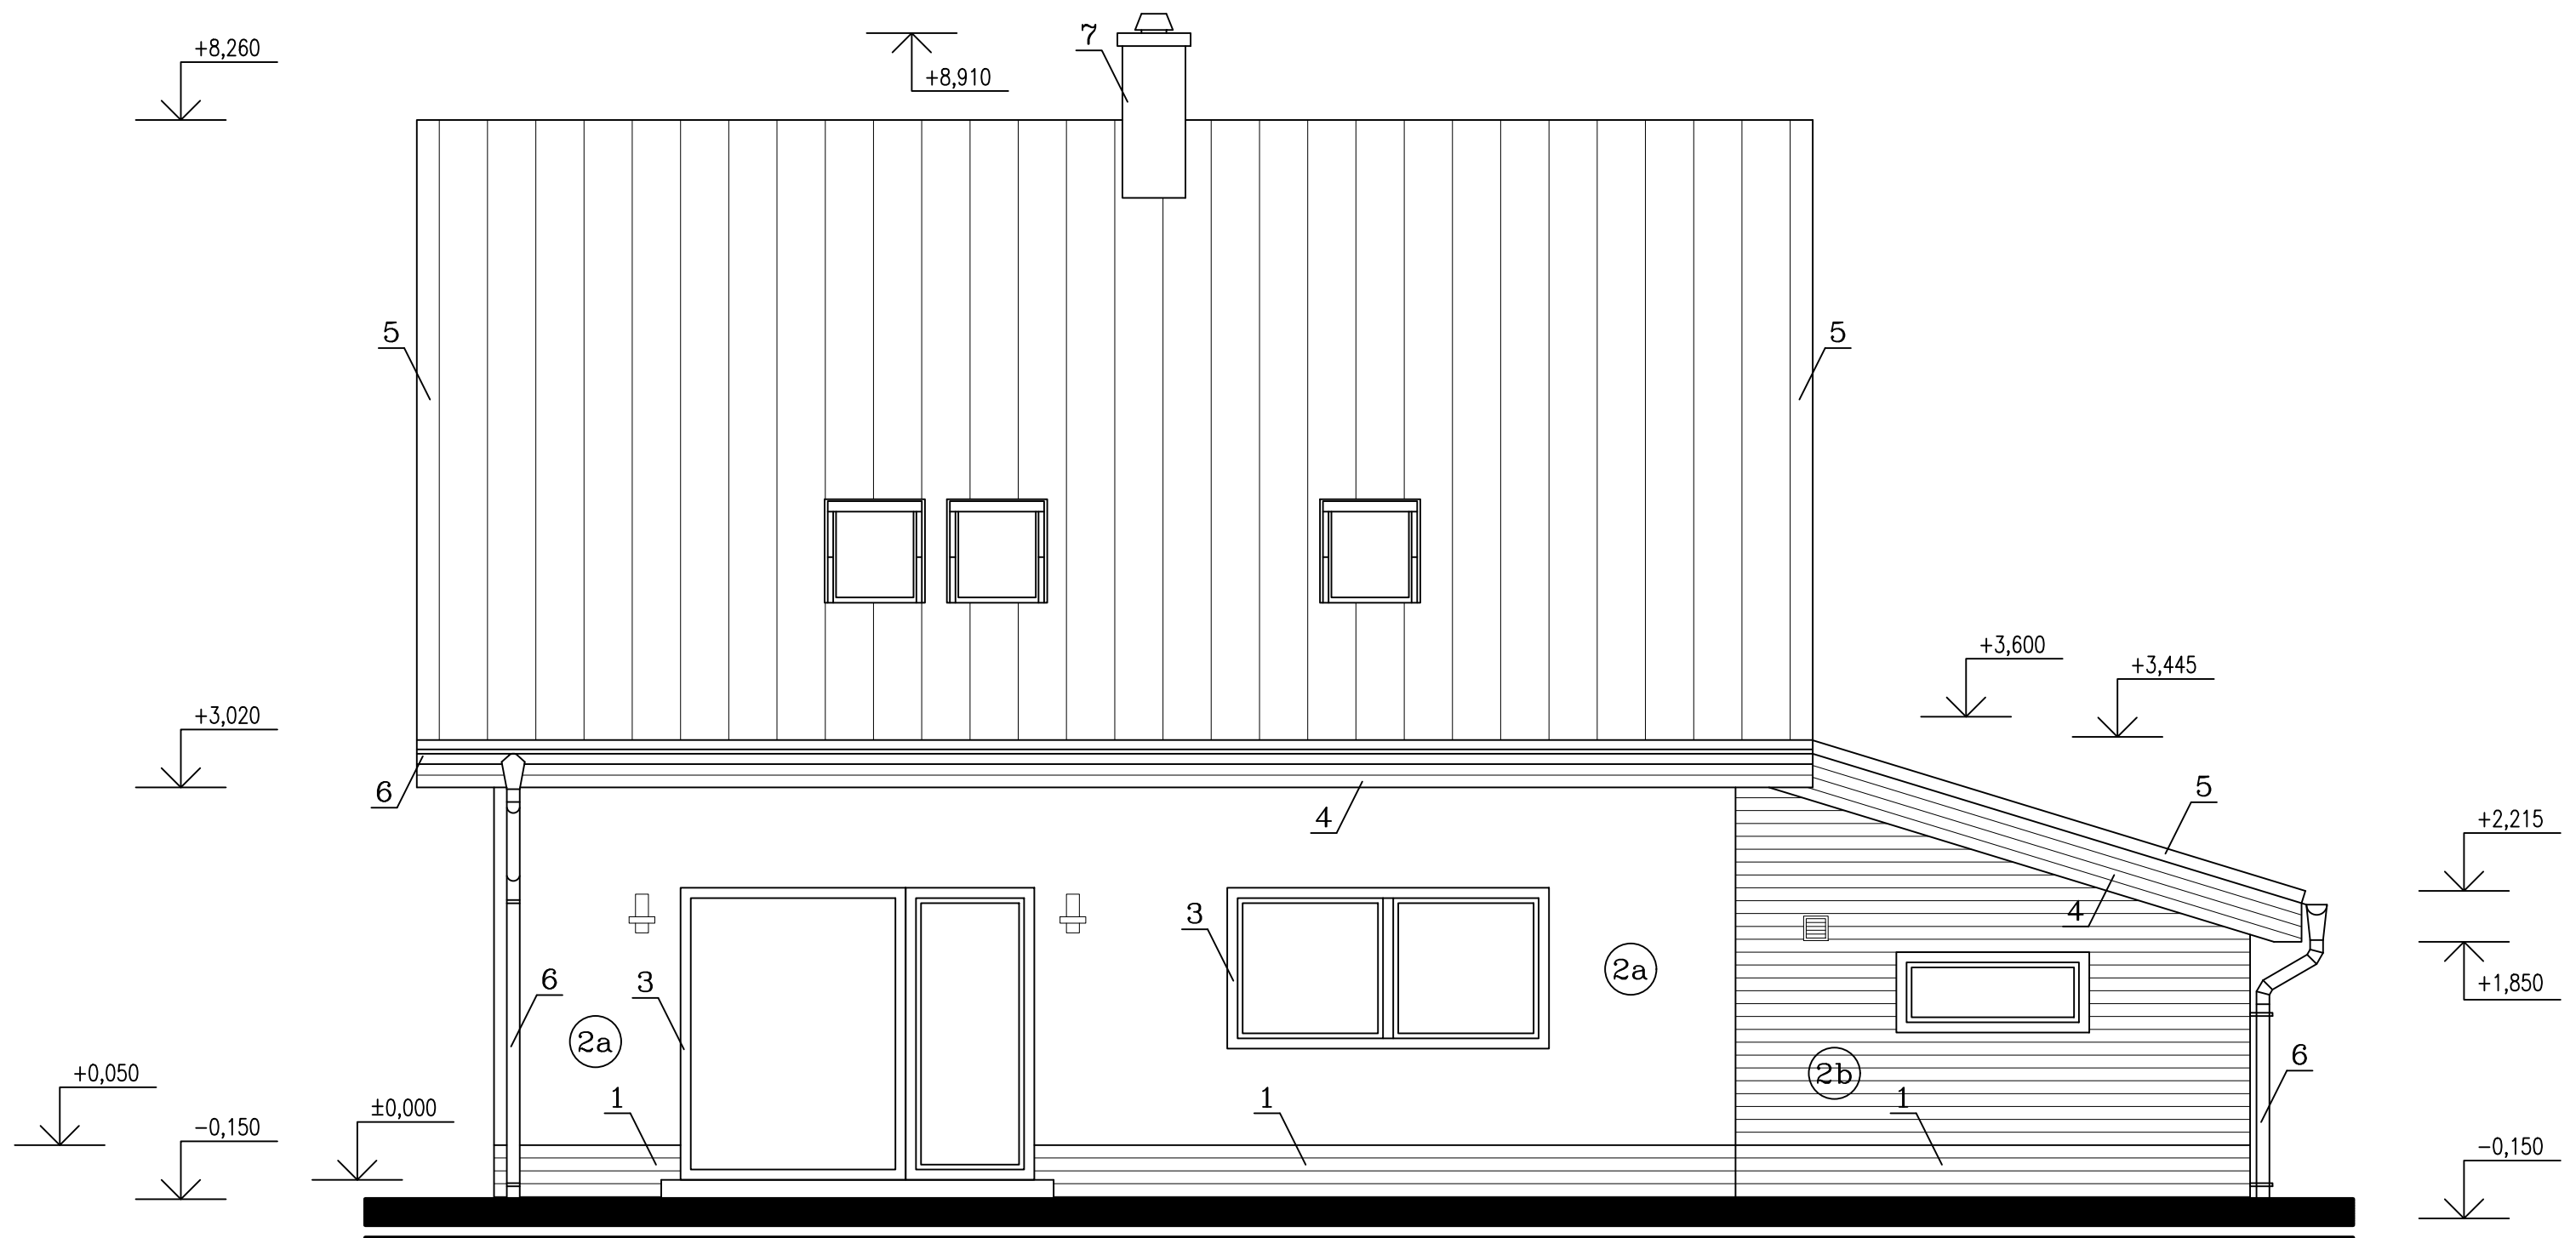

## Legenda materiálů

- 1 sokl – klinkerové pásky TERCA  
barevný odstín tmavě hnědý
- 2 vnější omítka WEBER.PAS AQUABALANCE tenkovrstvá jemnozrná (zrno 1,5 mm)  
barevný odstín č. OK4C – okrový (2a) v kombinaci s obkladem klinkerovými pásky  
TERCA – odstín tmavě hnědý (2b)
- 3 výplně otvorů – dveře, okna budou dřevěné  
barevný odstín tmavě hnědý
- 4 dřevěné prvky – podbití palubkami  
nátěr lazurovacím lakem na dřevo – odstín tmavě hnědý
- 5 betonová střešní taška BRAMAC CLASSIC – barevný odstín břidlicově černý
- 6 klempířské výrobky – pozinkovaný plech + nátěr odstín tmavě hnědý
- 7 nadstřešní část komína – vnější omítka WEBER.PAS AQUABALANCE  
tenkovrstvá jemnozrná (zrno 1,5 mm), barevný odstín č. OK4C – okrový

Tato dokumentace je duševním majetkem projektového ateliéru: Ing. Karel Peterka, Thermo plus, Trutnov  
Nesmí být užívána, šířena kopiemi a uveřejňována bez předchozího písemného souhlasu autora.



|                                                                       |                                                          |                                    |
|-----------------------------------------------------------------------|----------------------------------------------------------|------------------------------------|
| Hlavní projektant: Ing. Karel Peterka                                 | Zodpovědný projektant: Ing. Karel Peterka                | Vypracoval: Lukáš Materna          |
| Místo: k.ú. Velká Hraštice, p.p.č. 91/48                              | Stavebník: Ekaterina Matveeva, U Slovanky 2440/5C, Praha |                                    |
| Název akce: <b>RODINNÝ DŮM<br/>"BEÁTA"</b>                            |                                                          | Formát: 2xA4                       |
|                                                                       |                                                          | Datum: listopad 2021               |
|                                                                       |                                                          | Stupeň PD: typový projekt          |
|                                                                       |                                                          | Č.zakázky: 030/21/TP               |
| Příloha: ARCHITEKTONICKO-STAVEBNÍ ŘEŠENÍ<br><b>POHLED JIHOZÁPADNÍ</b> |                                                          | Měřítko: 1:50<br><b>D.1.1.A.10</b> |

Paré číslo