


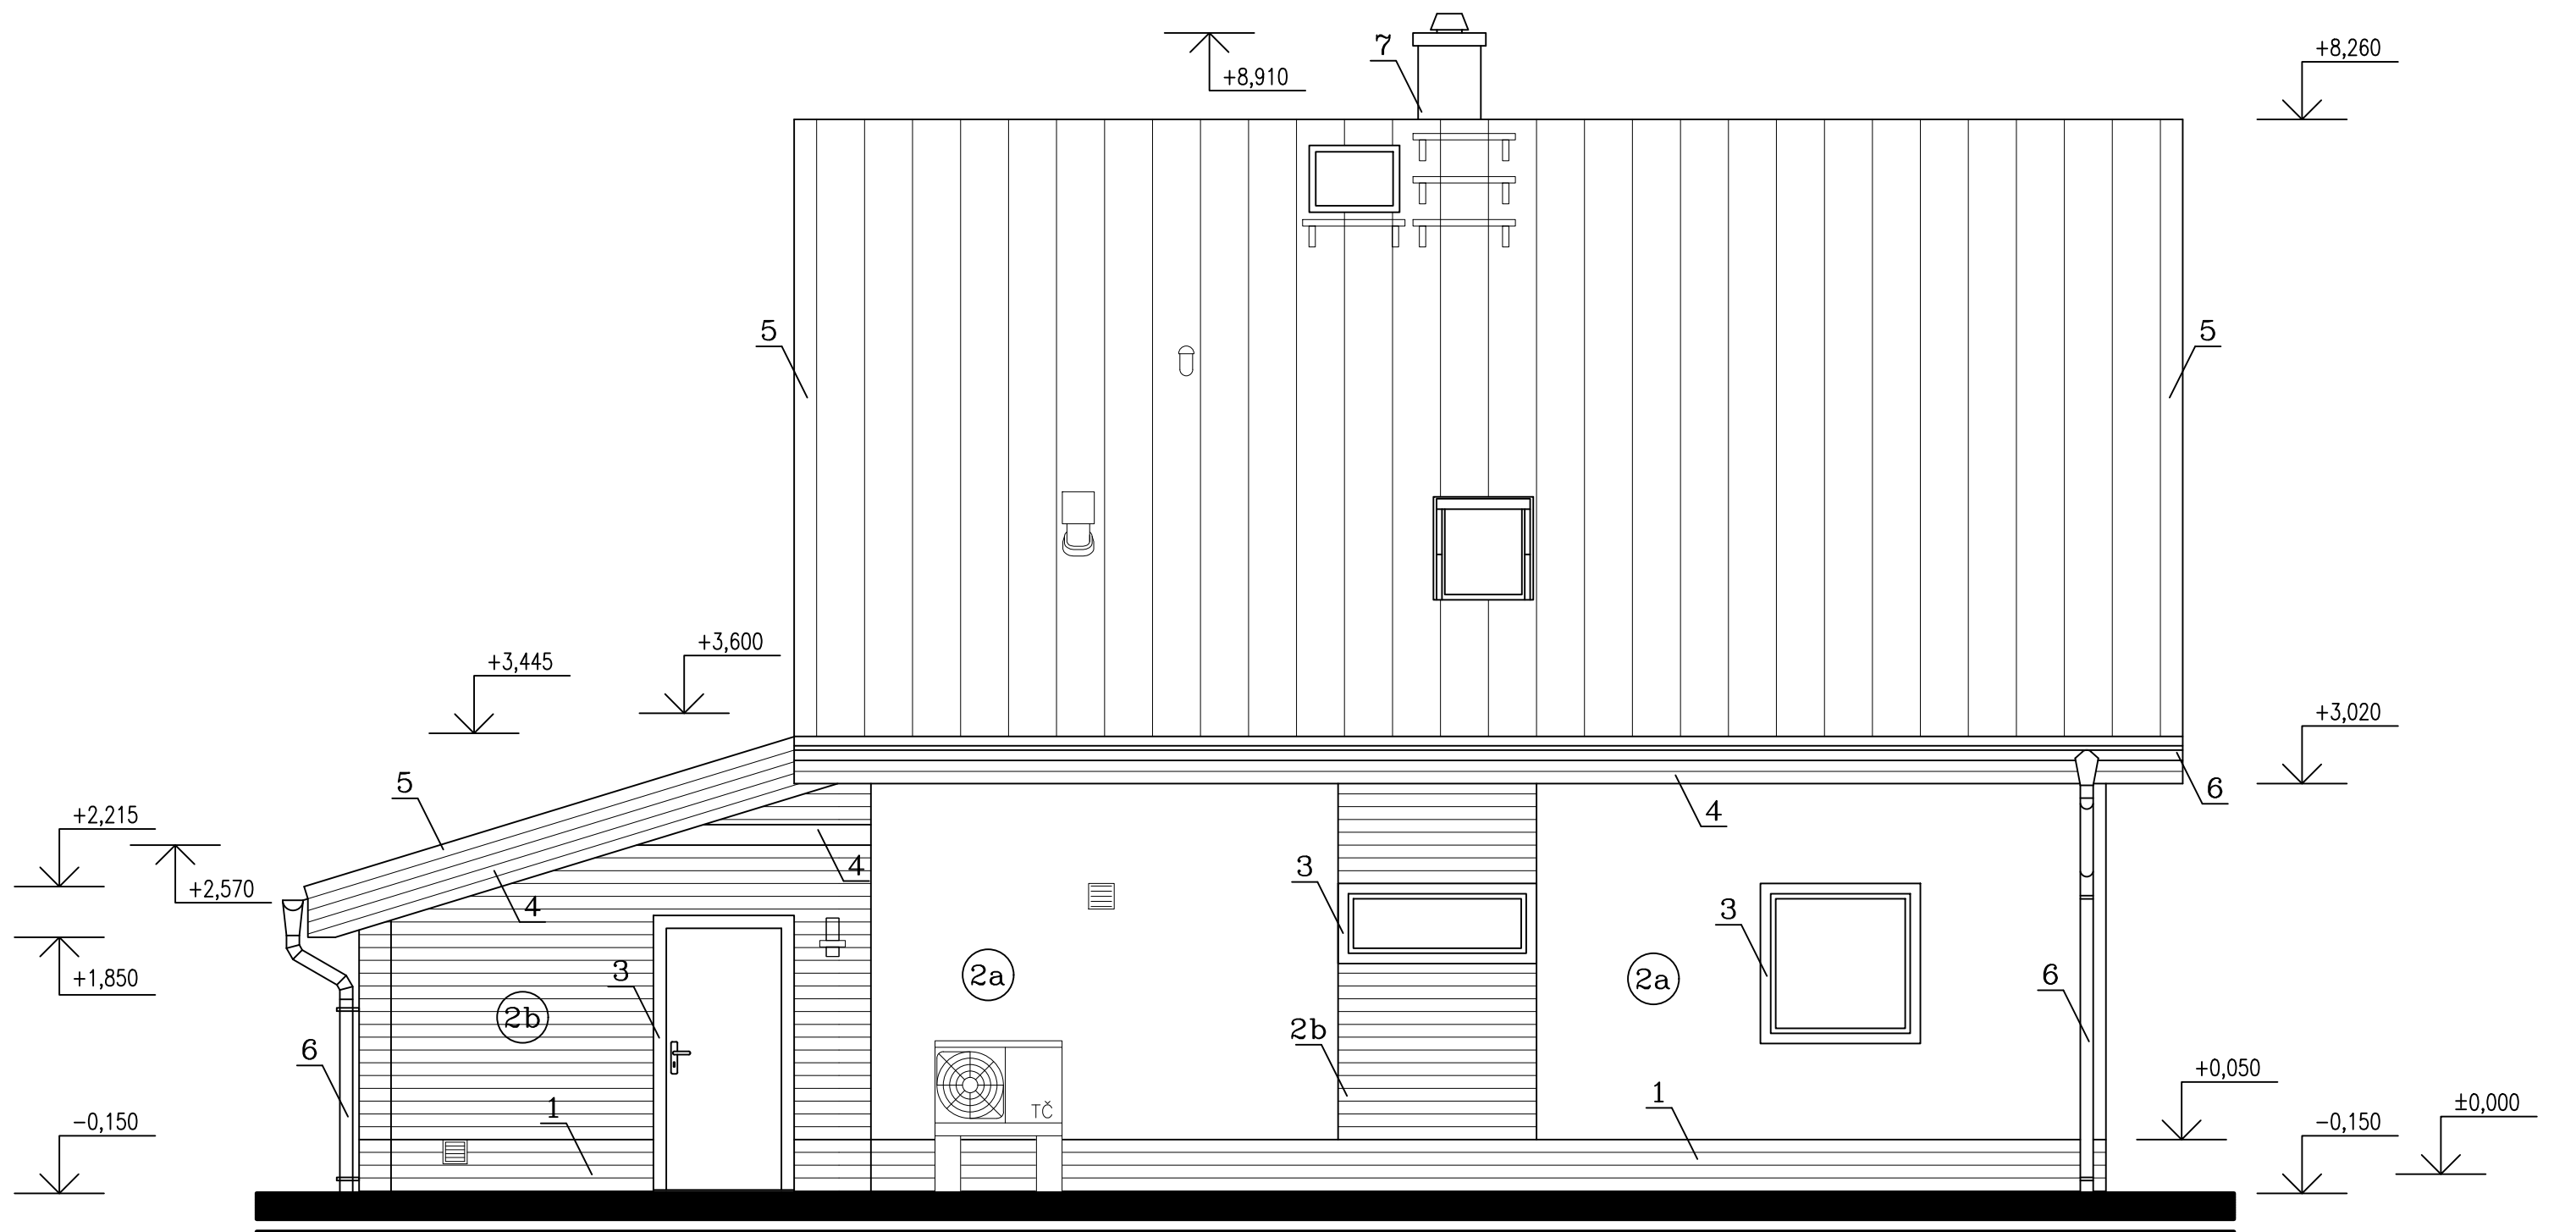

Legenda materiálů

- 1 sokl – klinkerové pásky TERCA
barevný odstín tmavě hnědý
- 2 vnější omítka WEBER.PAS AQUABALANCE tenkovrstvá jemnozrná (zrno 1,5 mm)
barevný odstín č. OK4C – okrový (2a) v kombinaci s obkladem klinkerovými pásky
TERCA – odstín tmavě hnědý (2b)
- 3 výplně otvorů – dveře, okna budou dřevěné
barevný odstín tmavě hnědý
- 4 dřevěné prvky – podbití palubkami
nátěr lazurovacím lakem na dřevo – odstín tmavě hnědý
- 5 betonová střešní taška BRAMAC CLASSIC – barevný odstín břidlicově černý
- 6 klempířské výrobky – pozinkovaný plech + nátěr odstín tmavě hnědý
- 7 nadstřešní část komína – vnější omítka WEBER.PAS AQUABALANCE
tenkovrstvá jemnozrná (zrno 1,5 mm), barevný odstín č. OK4C – okrový

Tato dokumentace je duševním majetkem projektového ateliéru: Ing. Karel Peterka, Thermo plus, Trutnov
Nesmí být užívána, šířena kopiemi a uveřejňována bez předchozího písemného souhlasu autora.

Paré číslo



Hlavní projektant: Ing. Karel Peterka	Zodpovědný projektant: Ing. Karel Peterka	Vypracoval: Lukáš Materna
Místo: k.ú. Velká Hraštice, p.p.č. 91/48	Stavebník: Ekaterina Matveeva, U Slovanky 2440/5C, Praha	
Název akce: RODINNÝ DŮM "BEÁTA"		Formát: 2xA4
Příloha: ARCHITEKTONICKO-STAVEBNÍ ŘEŠENÍ POHLED SEVEROVÝCHODNÍ		Datum: listopad 2021
		Stupeň PD: typový projekt
		Č.zakázky: 030/21/TP
		Měřítko: 1:50
		Č. přílohy: D.1.1.A.12