
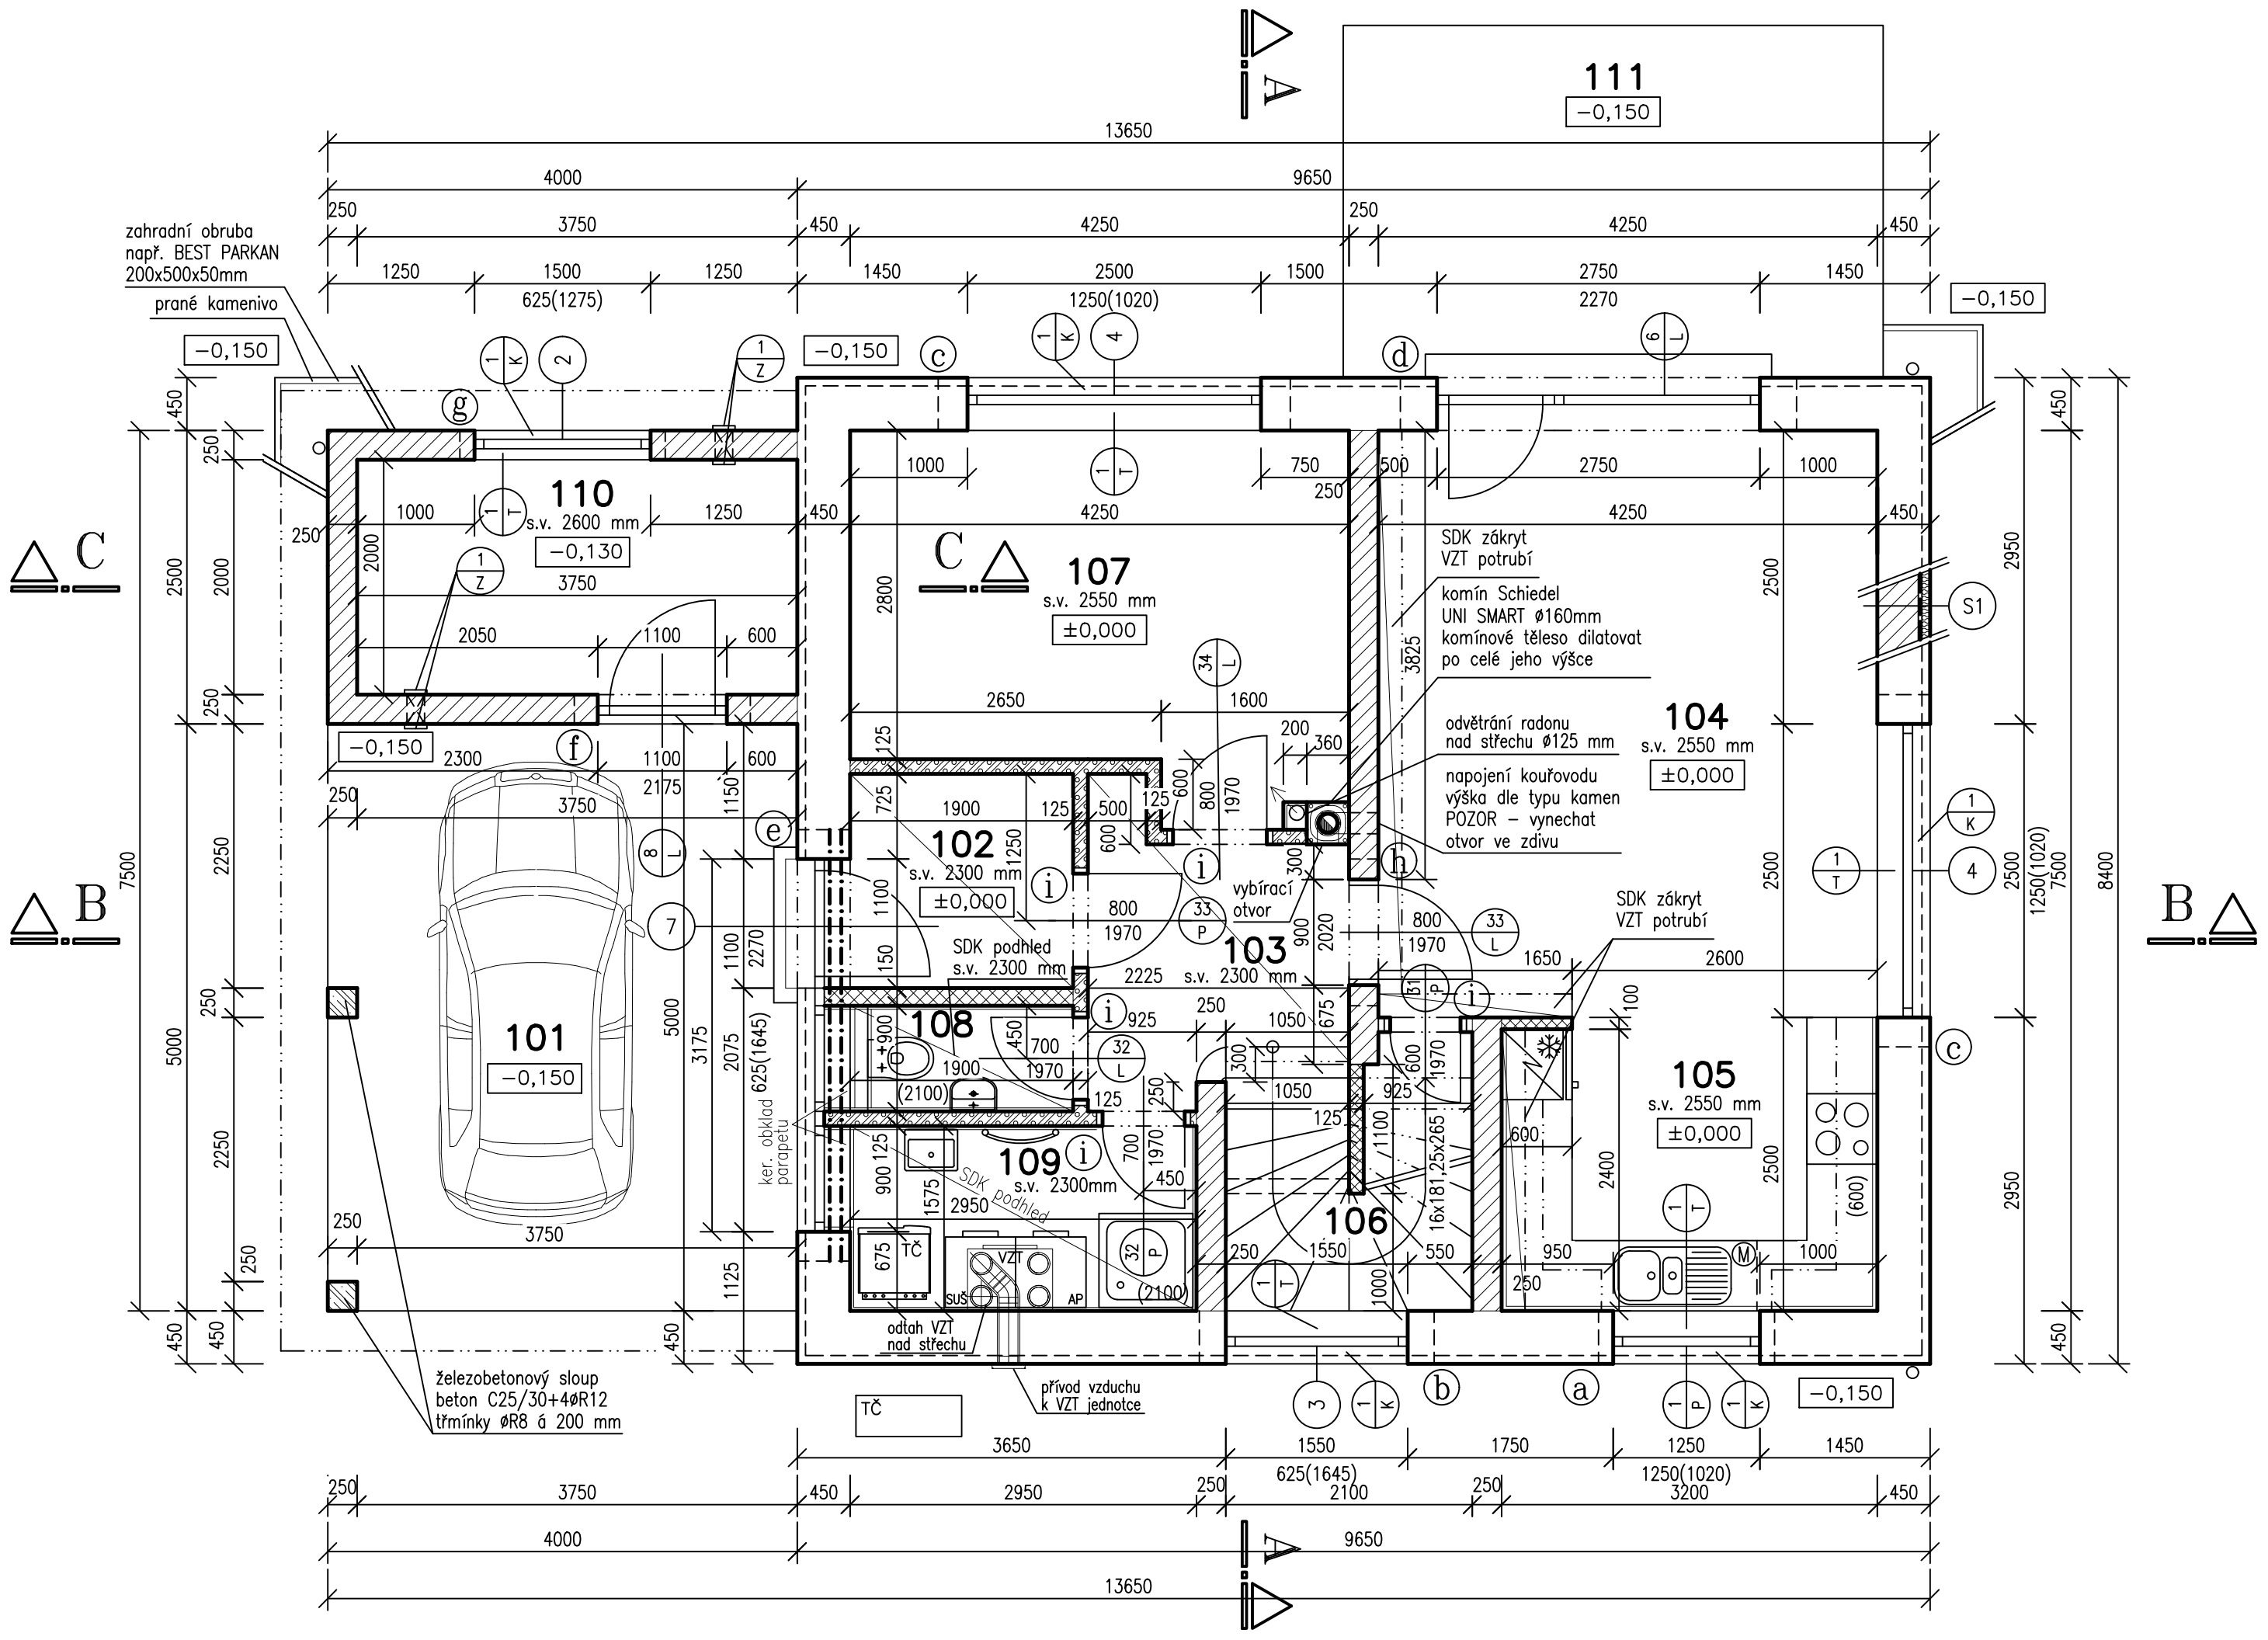
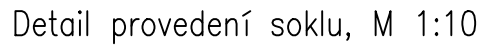


Detail provedení ostění a parapetu okenních otvorů, M 1:10

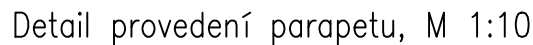

POZNÁMKA: plocha místností v tabulce označuje celkovou plochu místností včetně vestavěných skříní a kuchyňské linky

– dvojice ocelových válcovaných profilů budou vzájemně svařeny pásovinou 50/5 ve vzdálenostech 300mm na spodních i horních pásnicích a obetonují se

-
 zdivo z cihel broušených POROTHERM 44 T Profi, P8 (248x440x249 mm) včetně cihel doplňkových – cihla poloviční POROTHERM 44 1/2 T Profi, P8 (123x440x249 mm), dodávána jako dvojkol na maltu pro tenké spáry POROTHERM Profi (malta je součástí dodávěk cihel)
 první řádek vyztýž ze soklových cihel broušených POROTHERM 38 TS Profi, P8 (248x380x249 mm)
 druhý řádek vyztýž z cihel broušených POROTHERM 38 T Profi, P8 (248x380x249 mm)
 zdivo založit na základnici maltu POROTHERM Profi AM
-
 zdivo z cihel broušených POROTHERM 24 Profi, P10 (372x240x249 mm)
 na tenkovrstvou maltu POROTHERM Profi (malta je součástí dodávěk cihel)
 první řádek vyztýž ze soklových cihel broušených POROTHERM 24 S Profi, P10 (372x240x249 cm)
 zdivo založit na základnici maltu POROTHERM Profi AM
-
 zdivo z cihel broušených POROTHERM Profi 15, P10 (497x140x249 mm)
 na tenkovrstvou maltu POROTHERM Profi (malta je součástí dodávěk cihel)
 zdivo založit na základnici maltu POROTHERM Profi AM
-
 zdivo z cihel broušených POROTHERM Profi 11,5, P10 (497x115x249 mm)
 na tenkovrstvou maltu POROTHERM Profi (malta je součástí dodávěk cihel)
 zdivo založit na základnici maltu POROTHERM Profi AM
-
 zdivo z cihel POROTHERM Profi 11,5 AKU Profi, P10 (497x115x249 mm)
 na maltu POROTHERM Profi (malta je součástí dodávěk cihel)
 zdivo založit na základnici maltu POROTHERM Profi AM
-
 zdivo z cihel broušených POROTHERM Profi 8, P10 (497x80x249 mm)
 na maltu POROTHERM Profi (malta je součástí dodávěk cihel)
 zdivo založit na základnici maltu POROTHERM Profi AM

- * veškeré prostory ZT, ÚT EL provést dle příslušné části jednotlivých dílů projektové dokumentace
- * vnitřní dveře v příčkách jsou kolovány na osu a rozměry znamenají jejich světlé rozměry, při použití obložkových zárubní je třeba provést otvor větší dle montážních požadavků dodavatele dveří (šířka dveří +100mm, výška dveří +50mm, tj. 1970+50=2020mm)
- * překlady nad příčkami jsou navrženy pro obložkové zárubně (zvětšení otvoru o 100 mm)



Hlavní projektant: Ing. Karel Peterka		Zodpovědný projektant: Ing. Karel Peterka		Vyracoval: Lukáš Materna		
Místo: k.ú. Velká Hraštice, p.p.č. 91/48		Stavebník: Ekaterina Matveeva, U		Slavany 2440/5S, Praha		
Název akce: RODINNÝ DŮM „BEÁTA“				Formát		6x4
				Datum		listopad 2021
				Stupeň PD		typový projekt
				Č.zakázky		030/21/TP
				Príloha:		Č. přílohy:
ARCHITEKTONICKO–STAVEBNÍ ŘEŠENÍ				Měřítko:		1:50
PŘÍZEMÍ						D.1.1.A.3