



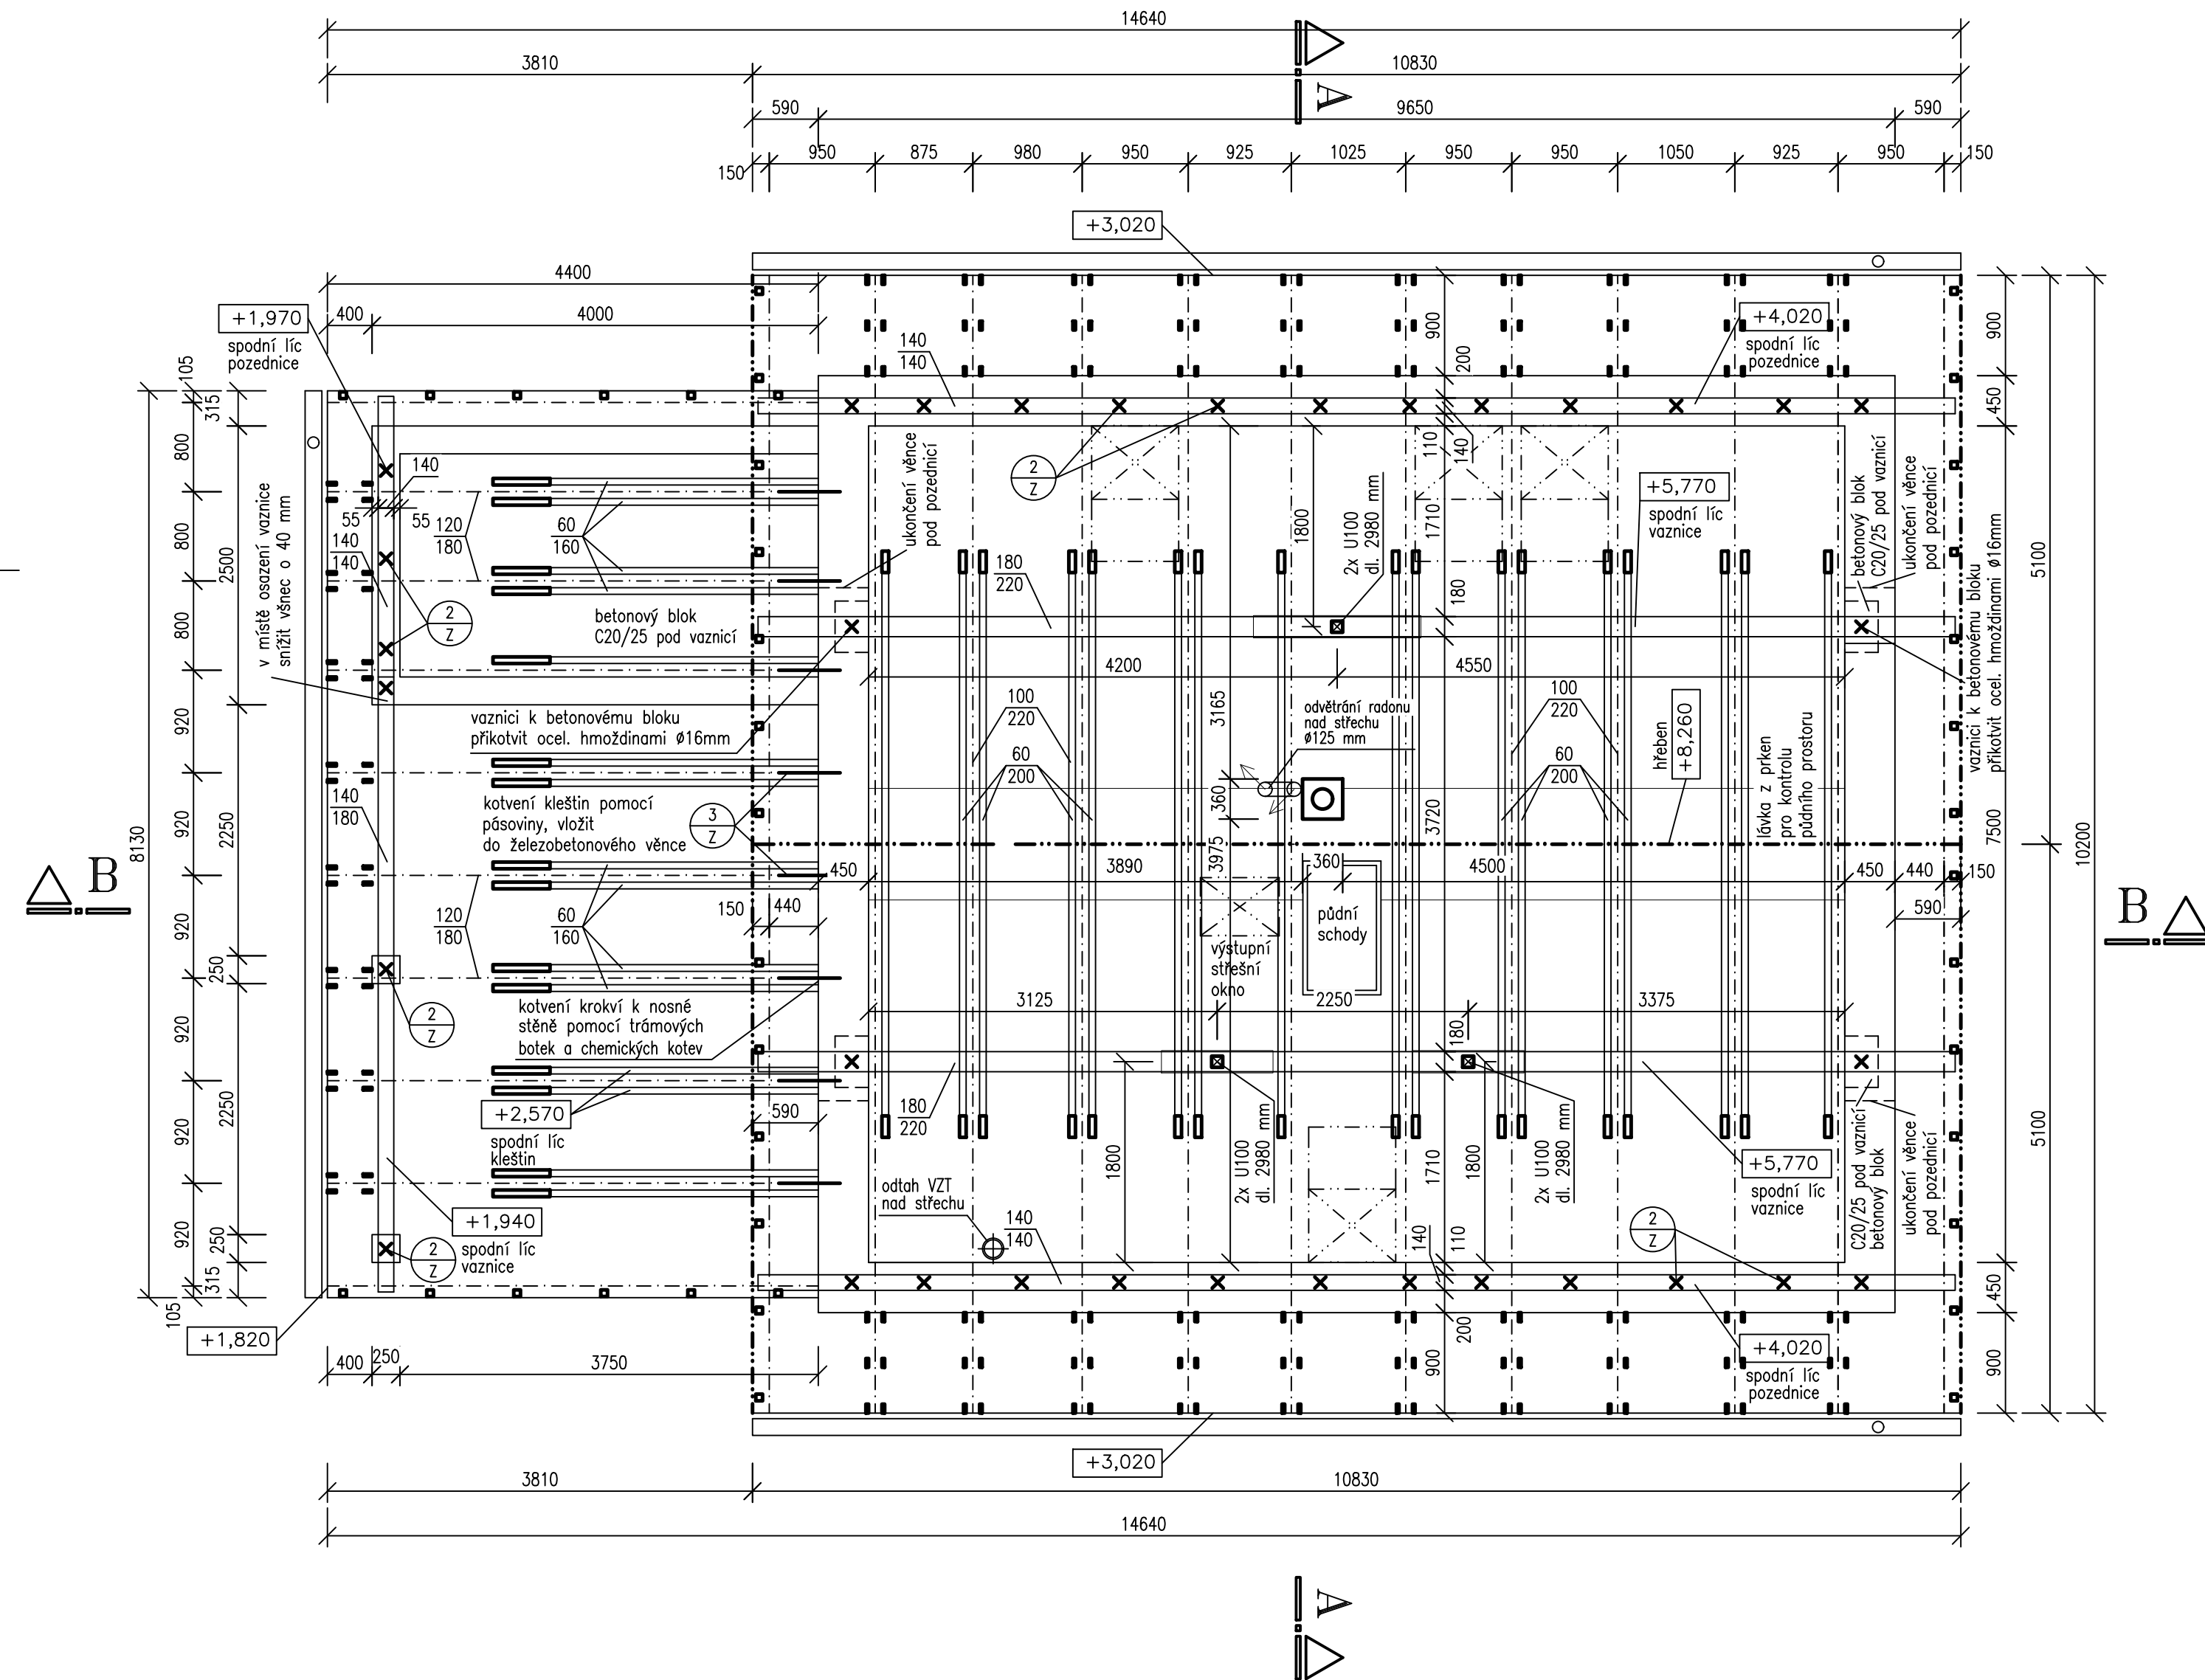

Detail D1

měřítko 1:25


kotvicí prvek ocelových stojek krovu
– plotna 200/300/8 mm
(přikotvit ocelovými hmoždinkami do věnce,
(případně přivařit ke stropním nosníkům)

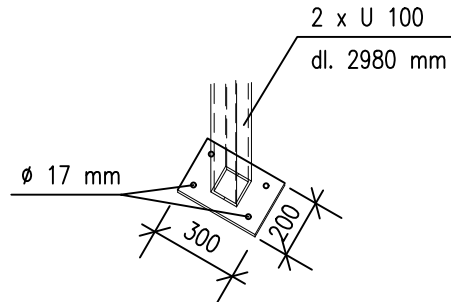

Detail D2

měřítko 1:25

kotvicí prvek dřevěných vaznic
k ocelovým stojkám krovu
– plech 200/1500/8 mm přivařit vodorovně
ke stojce (2 x U 100) + svislý plech
200/1000/8 mm s předvrtanými otvory
pro svorníky Ø 16 mm

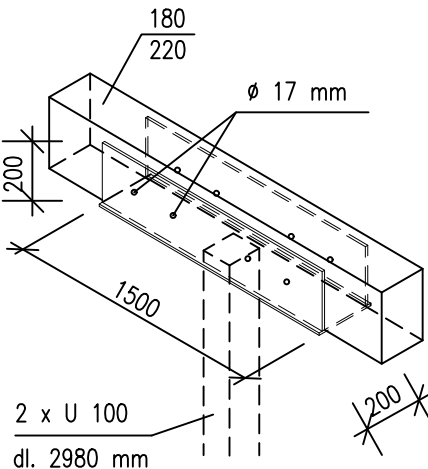

Výpis materiálů: ŘEZIVO

ŘEZIVO C24
VLHKOST max.20%

RODINNÝ DŮM:				
OZNAČENÍ	PROFIL	DÉLKA (m)	KUSY	CELKOVÁ DÉLKA
krokev	100/220	7,30 m	24	175,20 m
kleština	60/200	5,40 m	17	92,00 m
pozednice	140/140	11,00 m	2	21,80 m
vaznice	180/220	10,90 m	2	21,80 m

PŘÍSTŘEŠEK PRO AUTO A ZAHRADNÍ NÁŘADÍ:				
OZNAČENÍ	PROFIL	DÉLKA (m)	KUSY	CELKOVÁ DÉLKA
krokev	120/180	4,80 m	10	48,00 m
kleština	60/160	3,00 m	15	45,00 m
pozednice	140/140	2,60 m	1	2,60 m
pozední vaznice	140/180	5,60 m	1	5,60 m

Kotvení krokví nad přístřeškem a zahradním nářadím k nosné stěně
bude provedeno pomocí trámových botek a chemických kotev

Poznámka:

- * pozednice budou podloženy nepískovanou lepenkou
- * délky všech prvků kromě pozednic (měřené bez dělení na běžné m)
jsou zaokrouhleny pouze na 100mm směrem nahoru; pro objednávku
délky řeziva je nutné zohlednit prořez
- * nepohledové části krovu je nutno preventivně ošetřit přípravkem
proti houbám, plísním a škůdcům LIGNOFIX SUPER – výrobce Qualichem s.r.o.
pohledové části se ošetří přísadou do nátěru
(nátěr nepohledových částí je vhodné z důvodů kontroly pigmentovat)
- * ocelové prvky krovu jsou vykázány samostatně
- * laťování pod krytinou není uvedeno ve výpisu řeziva
- * spojení krokve a kleštiny – 2x svorník Ø12 s podložkami 50/50/5
(na každé straně kleštiny)
- * všechny krokve budou kotveny na pozednici oboustranně
–vždy dvěma spojovacími úhelníky 70/70/2 mm (BOVA)
celkem 24 ks (6x4) hřebíků BV/KH Ø4mm, délka 70 mm (F = 8,52 kN)

Upozornění:

- * před objednávkou řeziva ověřit soulad mezi projektovými rozměry
a skutečností přímo na stavbě, nutno zohlednit prořez !!!

Tato dokumentace je duševním majetkem projektového ateliéru: Ing. Karel Peterka, Thermo plus, Trutnov
Nesmí být užívána, šířena kopiemi a uveřejňována bez předchozího písemného souhlasu autora.

Paré číslo



Hlavní projektant: Ing. Karel Peterka	Zodpovědný projektant: Ing. Karel Peterka	Vypracoval: Lukáš Materna
Místo: k.ú. Velká Hraštice, p.p.č. 91/48	Stavebník: Ekaterina Matveeva, U Slovanky 2440/5C, Praha	
Název akce: RODINNÝ DŮM "BEÁTA"		Formát: 4xA4
		Datum: listopad 2021
		Stupeň PD: typový projekt
Č.zakázky: 030/21/TP		Č.přílohy: 030/21/TP
Příloha: ARCHITEKTONICKO–STAVEBNÍ ŘEŠENÍ KROV		Měřítko: 1:50 D.1.1.A.5