
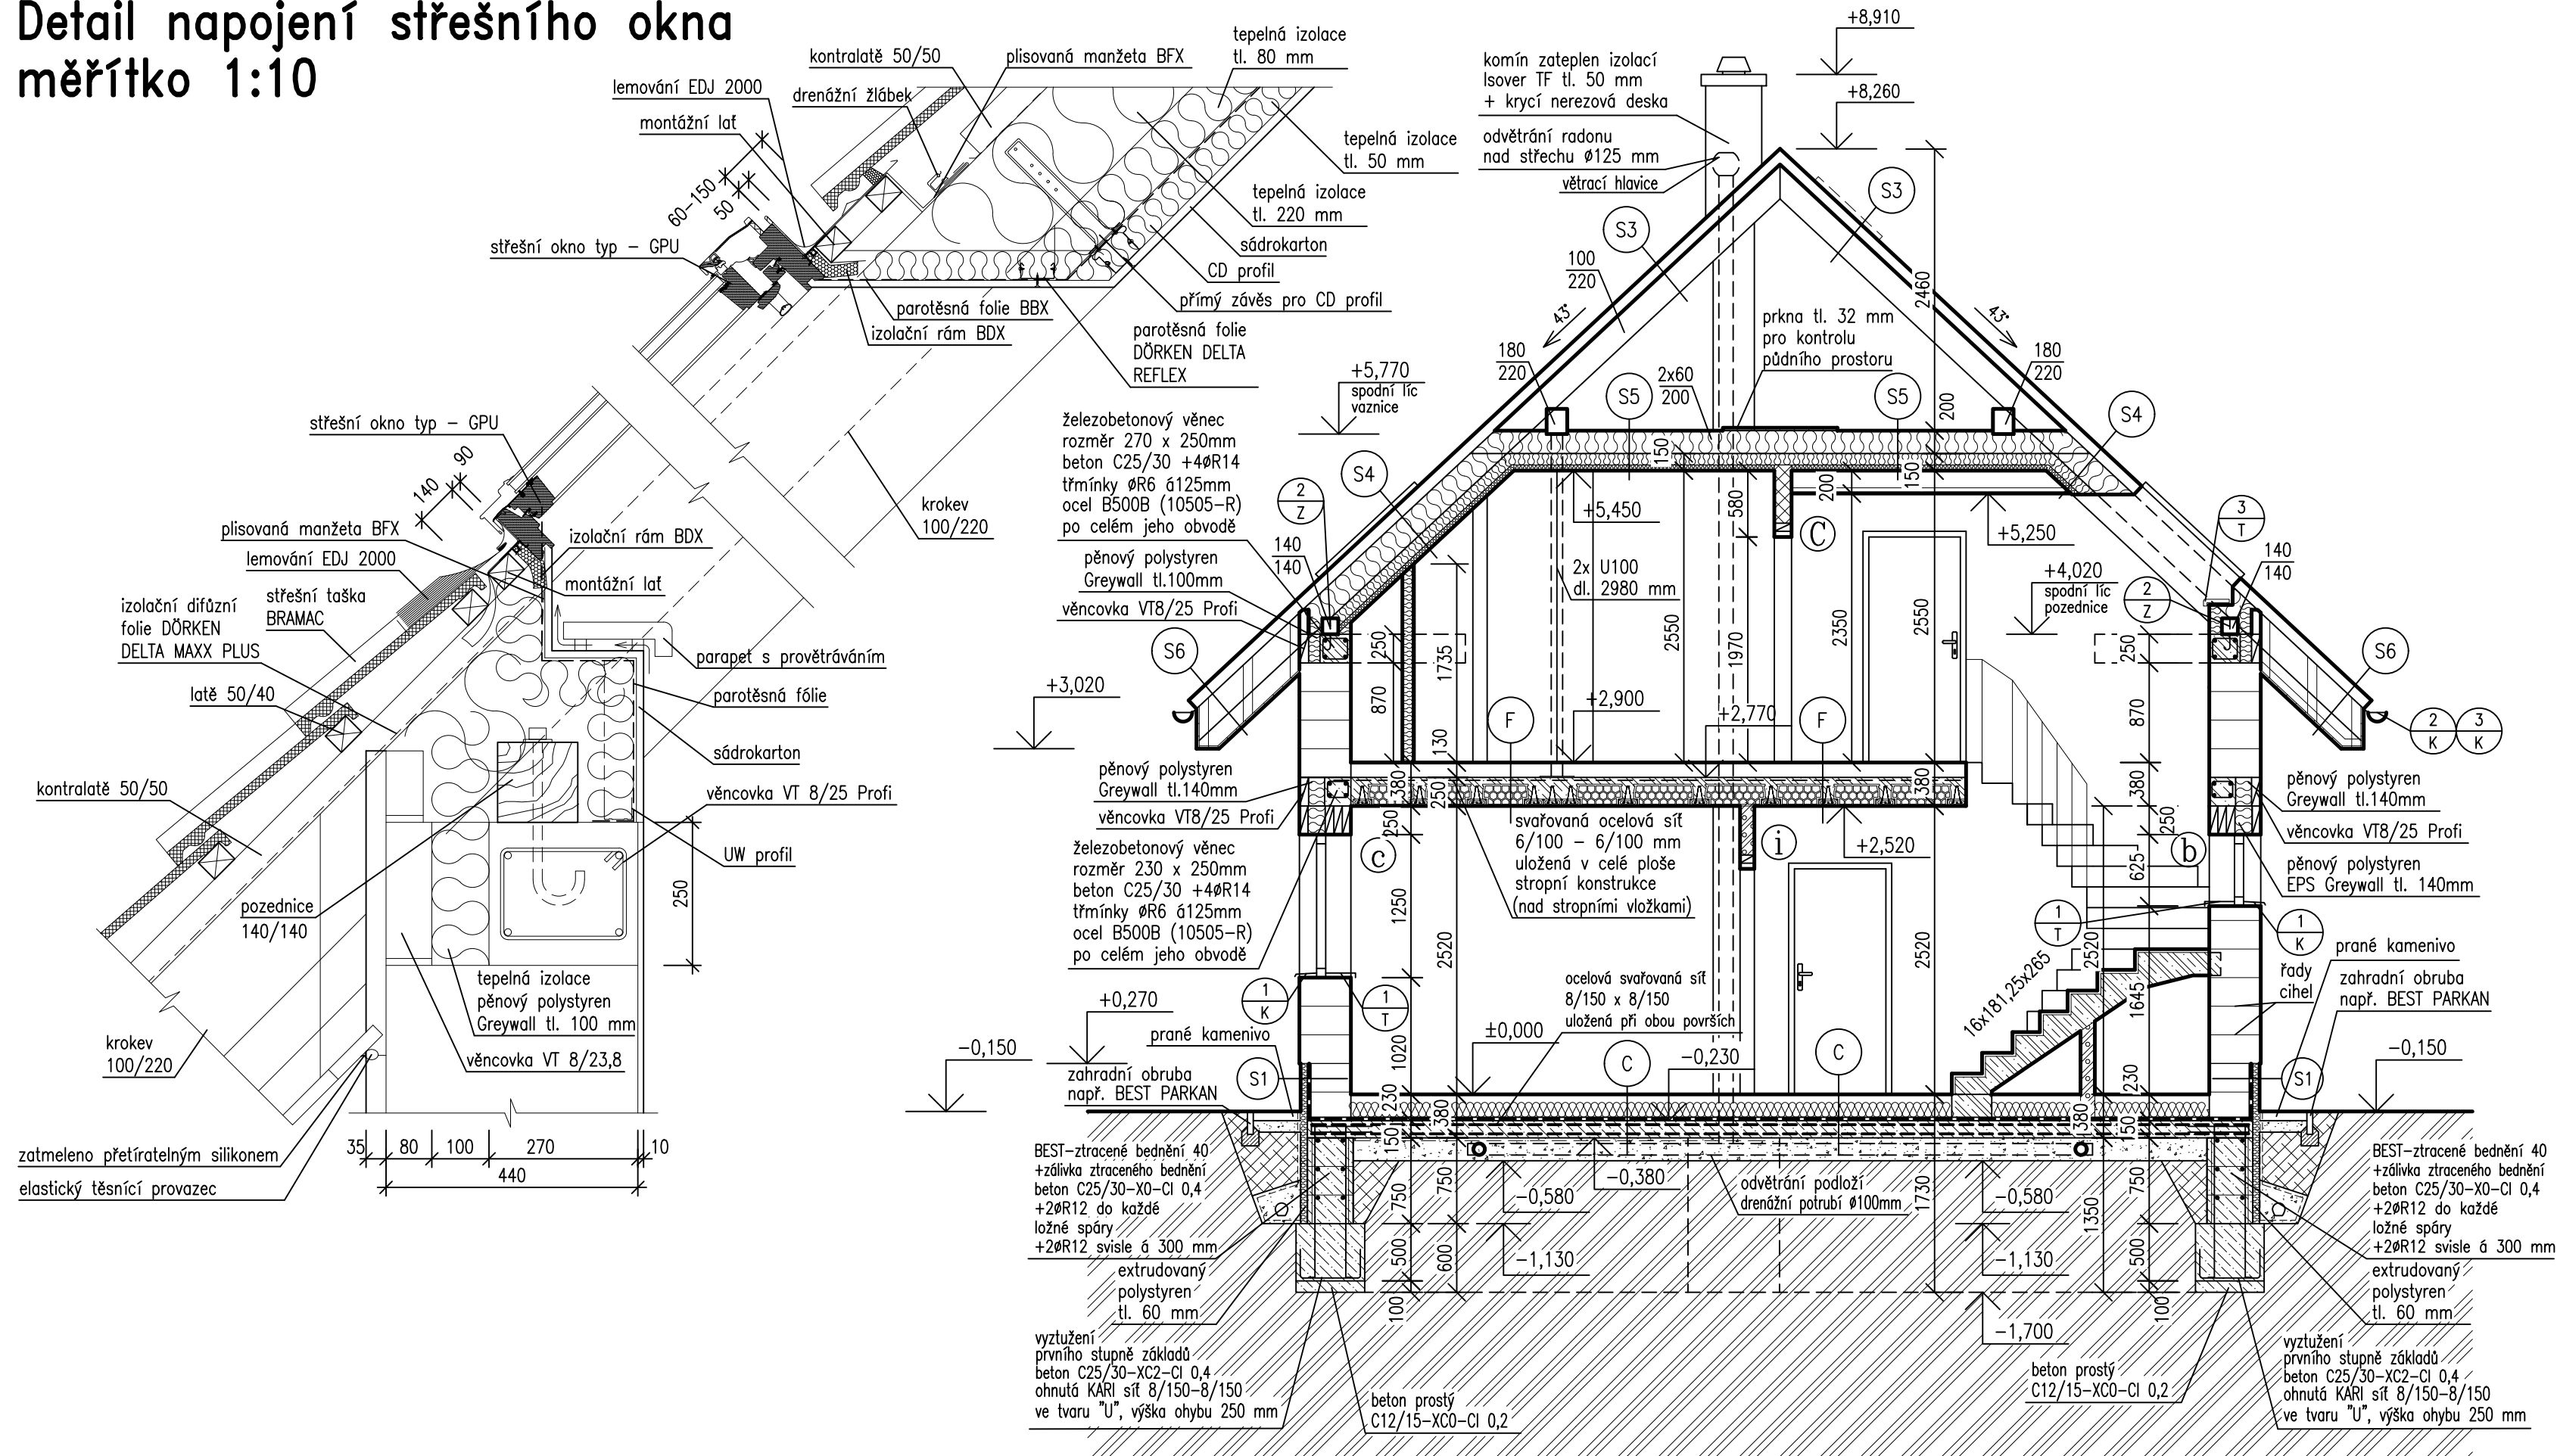
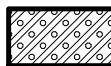


Detail napojení střešního okna měřítko 1:10

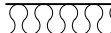

legenda materiálu:

- | | |
|---|---|
|  | zdivo z cihel broušených POROTHERM 44 T Profi, P8 (248x440x249 mm) včetně sibil doplňkových – cihla poloviční POROTHERM 44 1/2 T Profi, P8 (123x440x249 mm), dodávána jako dvojblok na maltu pro tenké spáry POROTHERM Profi (malta je součástí dodávek cihel)
první řádek vyzdít ze soklových cihel broušených POROTHERM 38 TS Profi, P8 (248x380x249 mm)
druhý řádek vyzdít z cihel broušených POROTHERM 38 T Profi, P8 (248x380x249 mm)
zdivo založit na základací maltě POROTHERM Profi AM |
|  | zdivo z cihel broušených POROTHERM Profi 15, P10 (497x140x249 mm)
na tenkovrstvou maltu POROTHERM Profi (malta je součástí dodávek cihel)
zdivo založit na základací maltě POROTHERM Profi AM |
|  | zdivo z cihel broušených POROTHERM Profi 11,5, P10 (497x115x249 mm)
na tenkovrstvou maltu POROTHERM Profi (malta je součástí dodávek cihel)
zdivo založit na základací maltě POROTHERM Profi AM |
|  | beton C25/30–XC2–Cl 0,4 (B30)
(první stupeň základů a podlahová deska)
beton C25/30–X0–Cl 0,4 (B30)
(druhý stupeň základů (bedněná část))
beton C25/30 – XC1 – Cl 0,2 (B30)
(beton věnců, stropní konstrukce) |
|  | násyp (zásyp) dobře hutnitelnou
zeminou, hutnit po vrstvách
max. 100 mm (ld > 0,67) |
|  | štrkavý podsyp |
|  | zem původní |
|  | tepelná izolace |
|  | hydroizolace |

Tato dokumentace je duševním majetkem projektového ateliéru: Ing. Karel Peterka, Thermo plus, Trutnov
Nesmí být užívána, šířena kopiemi a uveřejňována bez předchozího písemného souhlasu autora.

Paré číslo



Hlavní projektant: Ing. Karel Peterka		Zodpovědný projektant: Ing. Karel Peterka		Vyracoval: Lukáš Materna	
Místo: k.ú. Velká Hraštice, p.p.č. 91/48			Stavebník: Ekaterina Matveeva, U Slovanky 2440/5C, Praha		
Název akce: RODINNÝ DŮM "BEÁTA"			Formát	3xA4	
			Datum	listopad 2021	
			Stupeň PD	typový projekt	
			Č.zakázky	030/21/TP	
Příloha: ARCHITEKTONICKO–STAVEBNÍ ŘEŠENÍ ŘEZ A–A			Měřítko: 1:50	Č. přílohy: D.1.1.A.7	