



číslo	účel	plocha (m ²)
101	ZAVĚTRÍ	19,81
102	ZADVĚŘÍ	3,51
103	HALA	4,67
104	OBÝVACÍ POKOJ	21,25
105	KUCHYŇ	7,94
106	SPÍŽ	3,34
107	PRACOVNA	12,72
108	WC	1,71
109	SPRCHA + DOMÁCÍ PRÁCE	4,65
110	JÍZDNÍ KOLA, ZAHRADNÍ NÁŘADÍ	7,50
111	TERASA	13,80

tabulka účelu místnosti

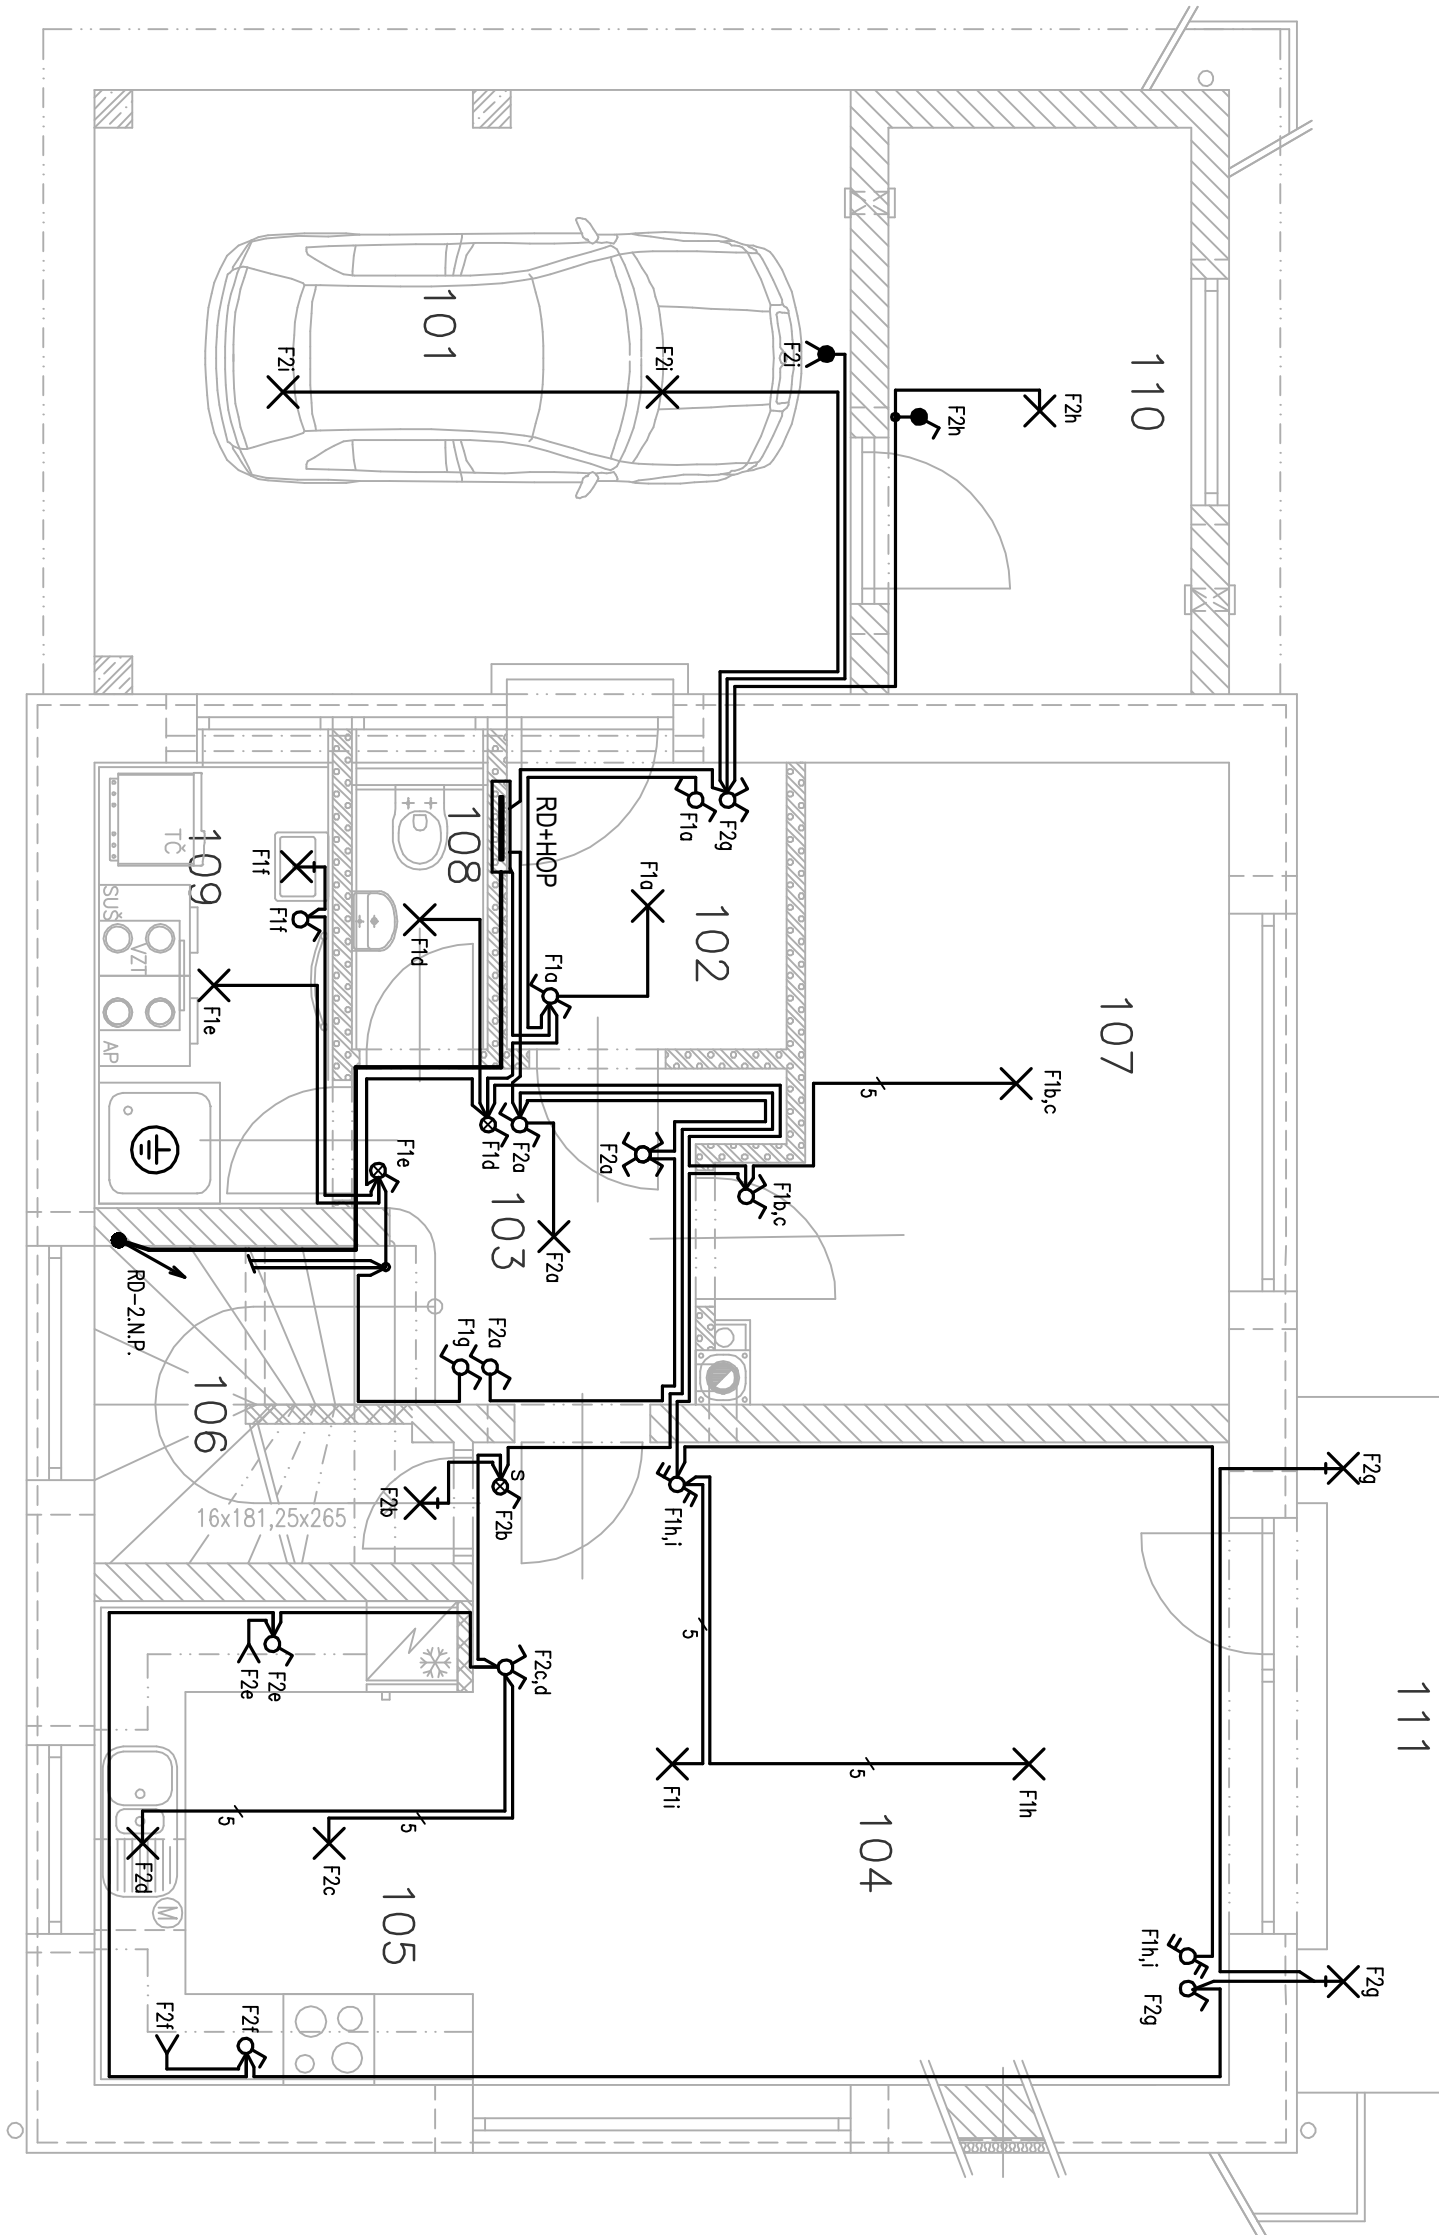

- VYPÍNAČ JEDNOPÓLOVÝ (ŘAZ.1) IP20
- VYPÍNAČ JEDNOPÓLOVÝ S ORIENTAČNÍ DOUŠŇAVKOU (ŘAZ.1So) IP20
- VYPÍNAČ JEDNOPÓLOVÝ SE SIGNALIZAČNÍ DOUŠŇAVKOU (ŘAZ.1S) IP20
- SPÍNAČ SERIOVÝ (ŘAZ.5) IP20
- SPÍNAČ STŘÍDAVÝ (ŘAZ.6) IP20
- SPÍNAČ KŘÍŽOVÝ (ŘAZ.7) IP20
- SPÍNAČ DVOJITÝ STŘÍDAVÝ (ŘAZ.6+6) IP20
- POHYBOVÉ ČIDLO IP44

TČ

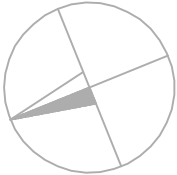

Ing. Hana Bezstarosti		Belveder 188, Dobruška, 518 01		Tel.: 606 83 73 08 * IČO:67465935		Razítko :
Zodpovědný projektant :		Ing. Hana Bezstarosti		Stupeň : dos		
Vyraboval :				Datum : 11/2021		
Investor : Ekaterina Matveeva, U Slovanky 2440/5C, 182 00 Praha				Č. zak. : 61/2021/EL		
Místo stavby : k.ú. Velká Hrašnice, p.p.č. 91/48				Měřítko : 1 : 50		
RODINNÝ DŮM TYP "BEATA"				Formát : 1 x A3		
				Č. výkr. : E1		
D.1.4 – Elektroinstalace		Č. paré :		Podpis :		
Půdorys 1.n.p. – světelné rozvody						

TECHNICKÁ ZPRÁVA JE NEDILNOU SOUČÁSTÍ PD