


tabulka účelu místnosti

číslo	účel	plocha (m ²)
201	HALA	4,61
202	LOŽNICE	12,22
203	POKOU	15,72
204	POKOU	12,15
205	LÁŽEŇ + WC	7,28
206	KOMORA	0,91

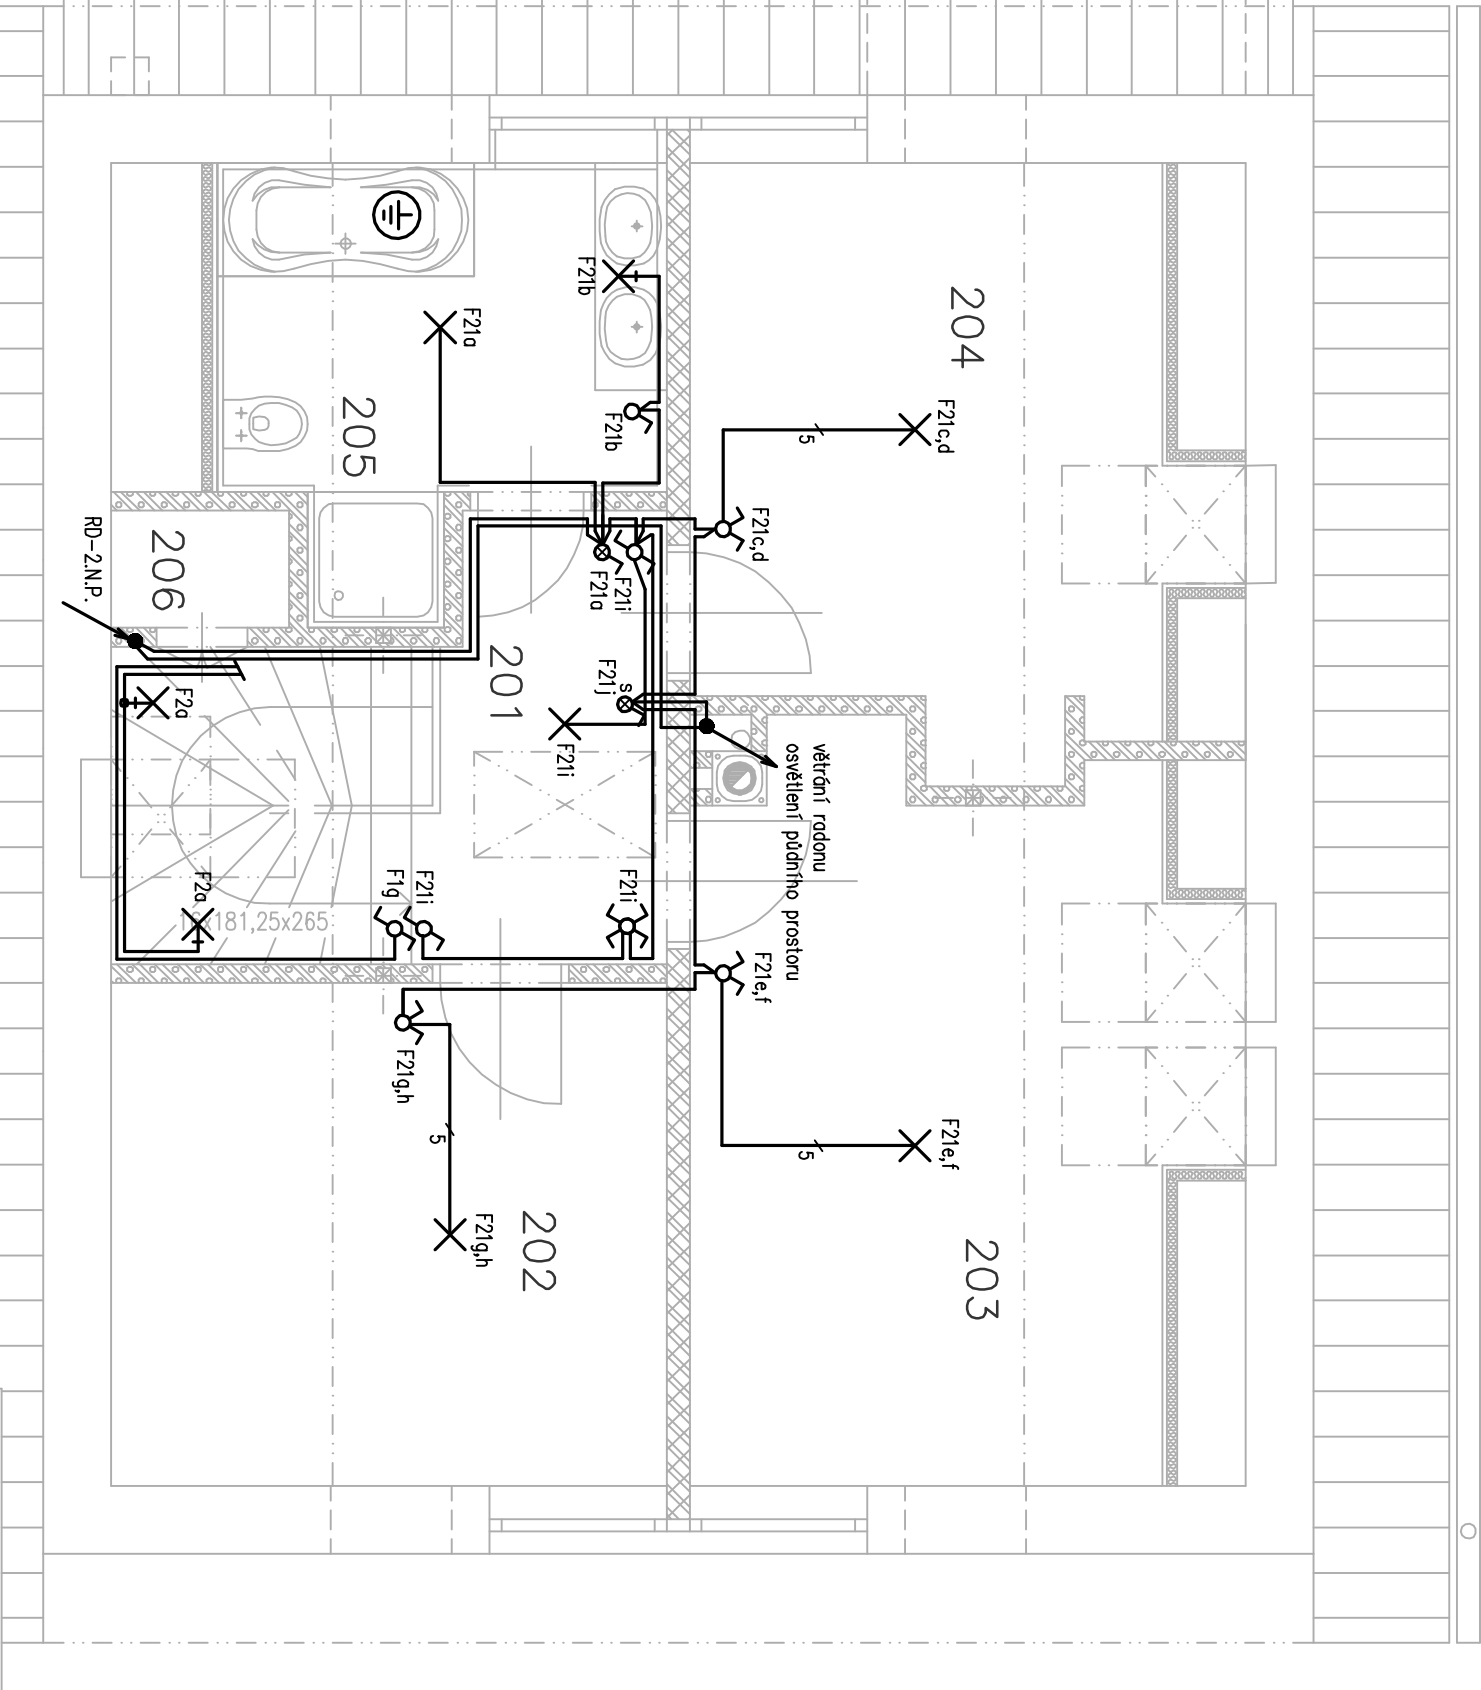

- VPINAČ JEDNOPOLOVÝ S ORIENTAČNÍ DOUTNAVKOU (ŘAZ.1S0) IP20
- VPINAČ JEDNOPOLOVÝ SE SIGNALIZAČNÍ DOUTNAVKOU (ŘAZ.1S) IP20
- SPINAČ SERIOVÝ (ŘAZ.5) IP20
- SPINAČ STRÍDAVÝ (ŘAZ.6) IP20
- SPINAČ KŘÍŽOVÝ (ŘAZ.7) IP20

TECHNICKÁ ZPRÁVA JE NEDÍLNOU SOUČÁSTÍ PD

Ing. Hana Bezstarosti		Belveder 188, Dobruška, 518 01		Tel.: 606 83 73 08 * IČO:67465935		Razítko :
Zodpovědný projektant :		Ing. Hana Bezstarosti		Stupeň : dos		
Vpracoval :		<i>Hana Bezstarosti</i>		Datum : 11/2021		
Investor : Ekaterina Matveeva, U Slovanky 2440/5C, 182 00 Praha				Č. zak.: 61/2021/EL		
Místo stavby : k.ú. Velká Hrašnice, p.p.č. 91/48				Měřítko : 1 : 50		
RODINNÝ DŮM TYP "BEATA"				Formát: 1 x A3		
				Č. výkr. : E2		
				Č. paré :		
D.1.4 – Elektroinstalace				Podpis :		
Půdorys 2.n.p. – světelné rozvody						