


tabulka účelu místnosti

číslo	účel	plocha (m ²)
101	ZAVĚTRÍ	19,81
102	ZADVEŘÍ	3,51
103	HALA	4,67
104	OBYVACÍ POKOJ	21,25
105	KUCHYŇ	7,94
106	SPÍŽ	3,34
107	PRACOVNA	12,72
108	WC	1,71
109	SPRCHA + DOMÁCÍ PRÁCE	4,65
110	JÍZDNÍ KOLA, ZAHRADNÍ NÁŘADÍ	7,50
111	TERASA	13,80

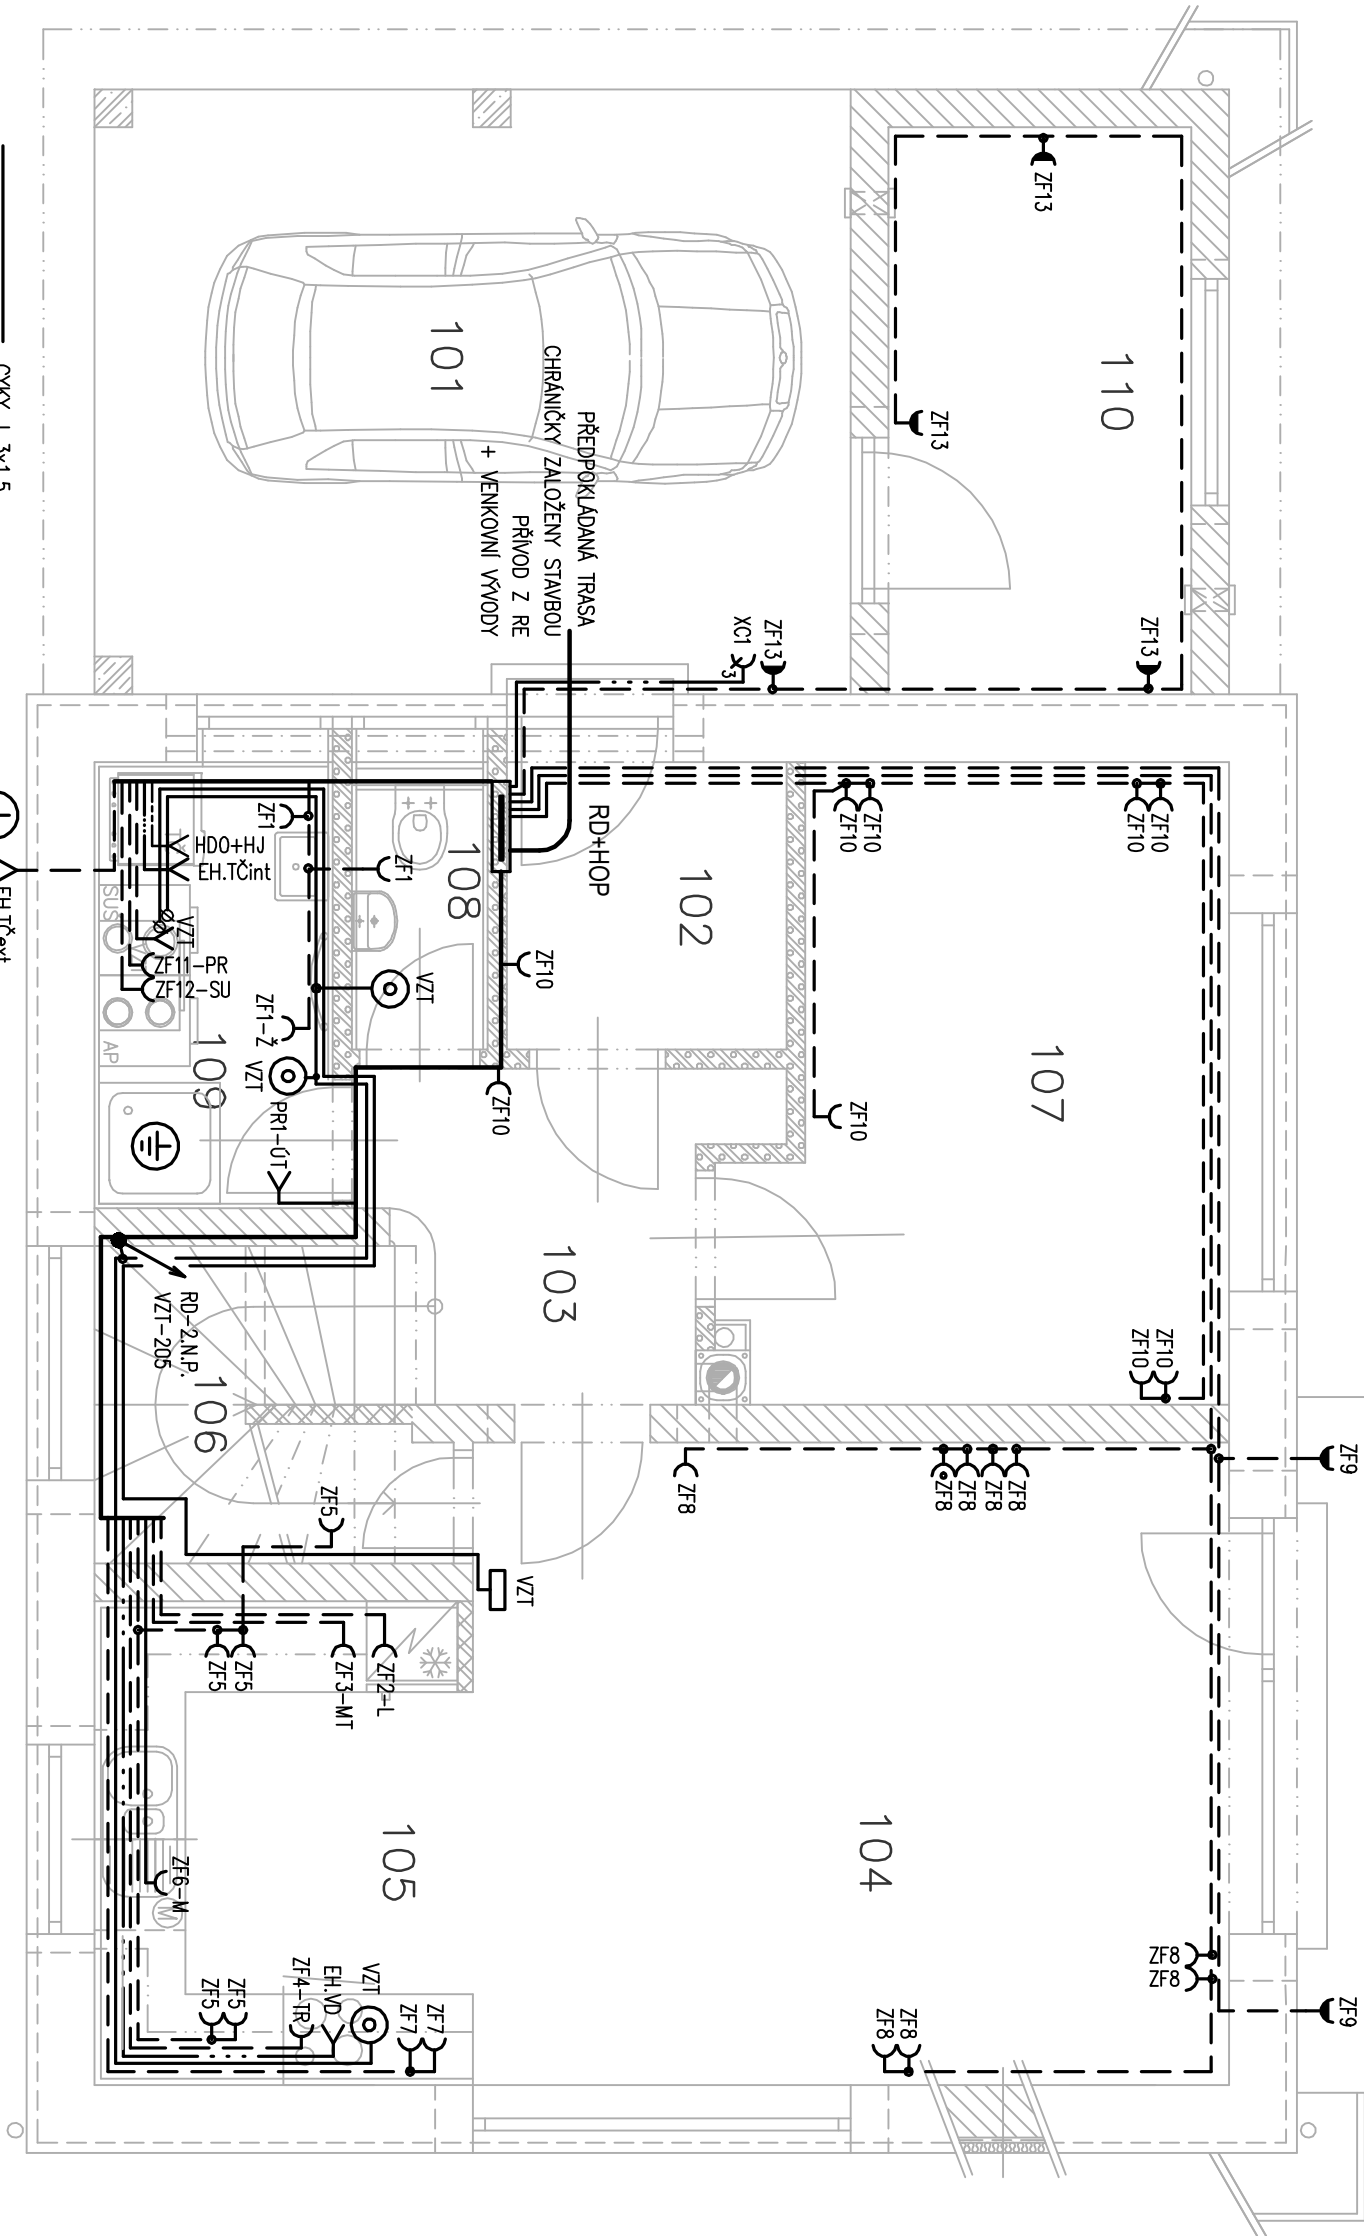

- CYKY J 3x1,5
- CYKY J 3x2,5
- .-.-.- CYKY J 5x2,5, 4
- _____ SPOLEČNÁ TRASA

- ⊙ TLAČÍTKOVÝ OVLADAČ (1/0), IP20
- ┘ ZASUVKA 230 V IP20
- ┘ ZASUVKA 230 V S VESTAVĚNOU PŘEPĚTOVOU OCHRANOU IP20
- ┘ ZASUVKA 230 V IP44
- ┘ ZASUVKA 400V, 32A
- ⊕ MÍSTNOST S MÍSTNÍM (DOPŇUJÍCÍM) POSPOJOVÁNÍM

TECHNICKÁ ZPRÁVA JE NEDILNOU SOUČÁSTÍ PD

Ing. Hana Bezstarosti		Belveder 188, Dobruška, 518 01		Tel.: 606 83 73 08 * IČO:67465935		Razítko :	
Zodpovědný projektant :		Ing. Hana Bezstarosti					Stupeň : dos
Vyráběoval :							
Investor : Ekaterina Motveeva, U Slovanky 2440/5C, 182 00 Praha		Datum : 11/2021					
Místo stavby : k.ú. Velká Hrošnice, p.p.č. 91/48		Č. zak. : 61/2021/EL					
RODINNÝ DŮM TYP "BEATA"		Měřitko : 1 : 50					
		Formát : 1 x A3					
		Č. výkř. : E3					
D.1.4 – Elektroinstalace		Č. paré :					Podpis :
Půdorys 1.n.p. – ostatní rozvody							