


tabulka účelu místnosti

číslo	účel	plocha (m ²)
201	HALA	4,61
202	LOŽNICE	12,22
203	POKOU	15,72
204	POKOU	12,15
205	LÁŽEŇ + WC	7,28
206	KOMORA	0,91

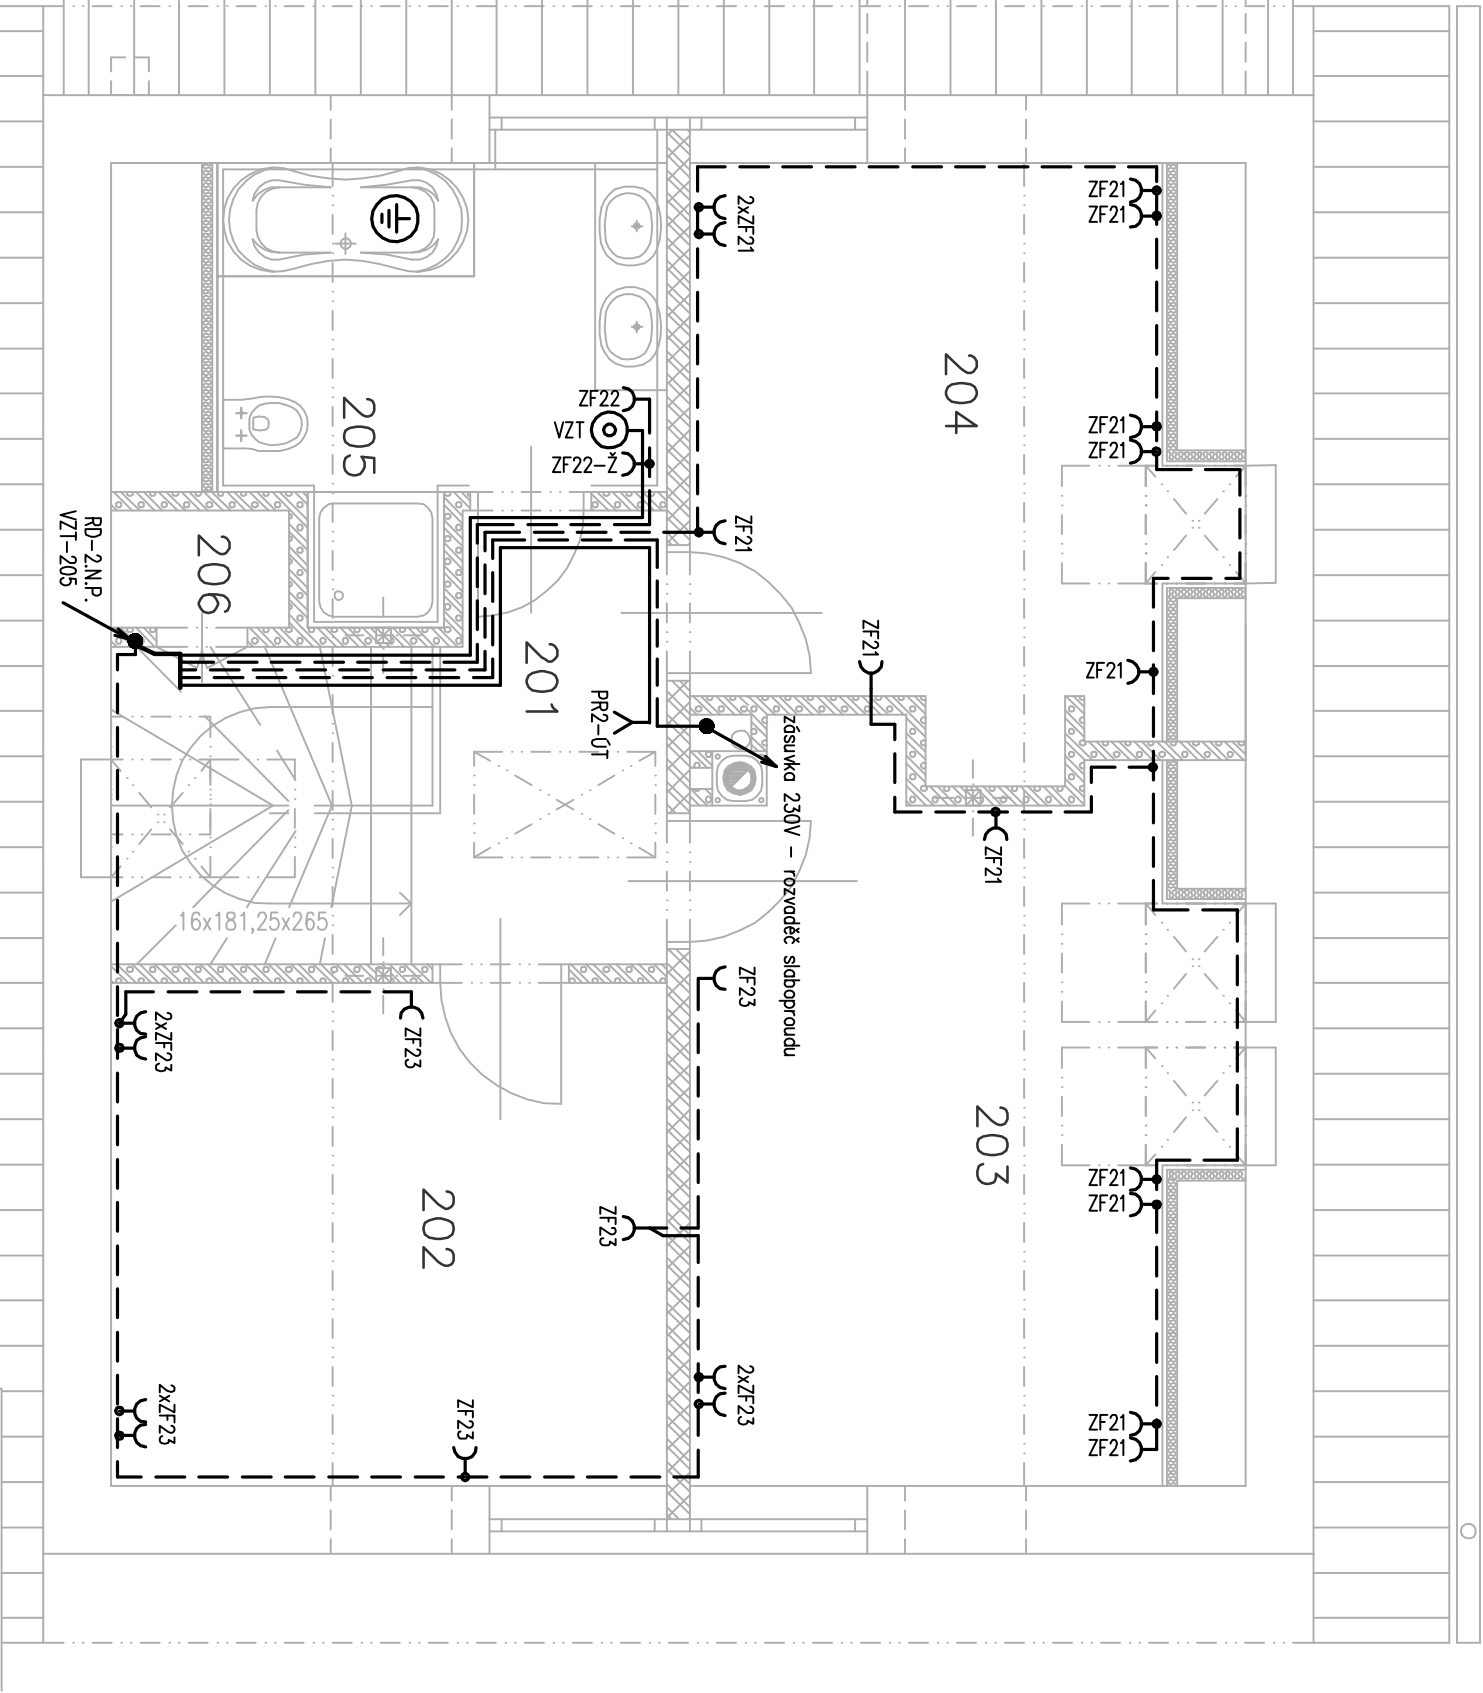

TECHNICKÁ ZPRÁVA JE NEDILNOU SOUČÁSTÍ PD

- Y ZÁSUVKA 230 V IP20
- ⊙ TLAČÍTKOVÝ OVLADAČ (1/0), IP20

Ing. Hana Bezstarosti		Belveder 188, Dobruška, 518 01		Tel.: 606 83 73 08 * IČO:67465935		Razítko :	
Zodpovědný projektant :		Ing. Hana Bezstarosti		Stupeň : dos			
Vyraboval :				Datum : 11/2021			
Investor : Ekaterina Matveeva, U Slovanky 2440/5C, 182 00 Praha				Č. zak.: 61/2021/EL			
Místo stavby : k.ú. Velká Hrošovice, p.p.č. 91/48				Měřítko : 1 : 50			
RODINNÝ DŮM TYP "BEATA"				Formát : 1 x A3			
				Č. výkr. :			
				Č. paré :		Podpis :	
D.1.4 – Elektroinstalace							
Půdorys 2.n.p. – ostatní rozvody							