



tabulka účelu místnosti

ČÍSLO	ÚČEL	PLOCHA (m ²)
101	ZAVĚTRÍ	19,81
102	ZÁDVEŘÍ	3,51
103	HALA	4,67
104	OBYVACÍ POKOJ	21,25
105	KUCHYŇ	7,94
106	SPÍŽ	3,34
107	PRACOVNA	12,72
108	WC	1,71
109	SPRCHA + DOMÁCÍ PRÁCE	4,65
110	JÍZDNÍ KOLA, ZAHRADNÍ NAŘADÍ	7,50
111	TERASA	13,80

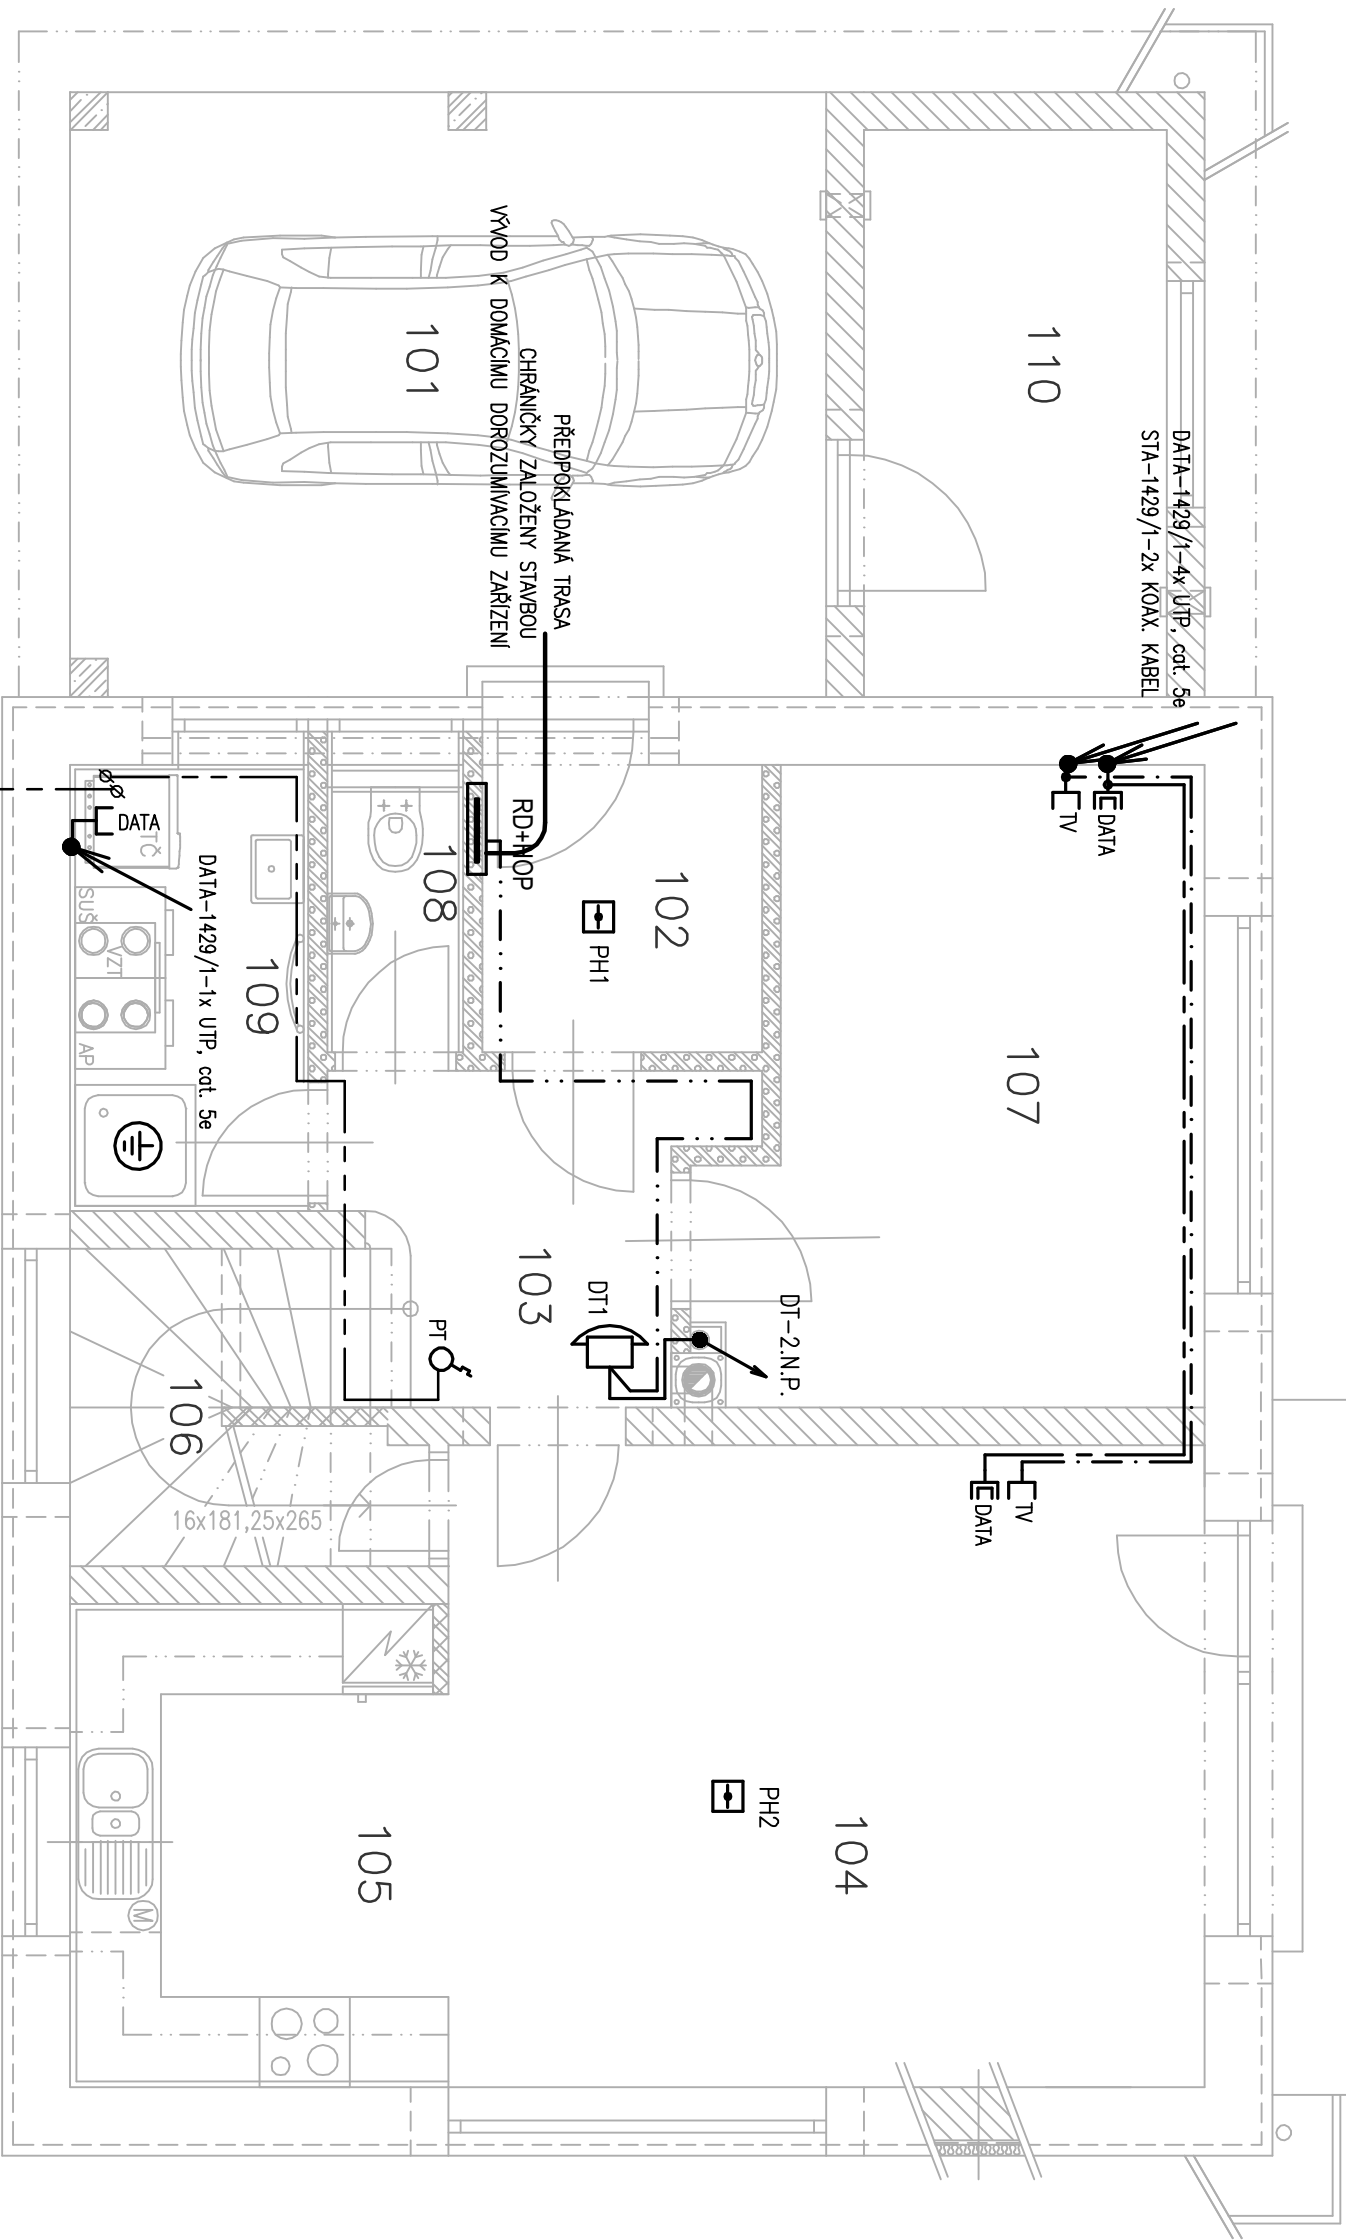

- DATA
ZASUVKA JEDNODUCHÁ 1xRJ45 IP20
- TV DATA
ZASUVKA DVOUITÁ 2xRJ45 IP20
- TV
ZASUVKA TV
- DOMÁCÍ (VIDEO)TELEFON
- POŽÁRNÍ HLASIČ
- VNITŘNÍ TEPLOTNÍ ČIDLO (dodávka ÚT)
- VENKOVNÍ TERMOSTAT (dodávka ÚT)

- · — · — · — STA-1429/1-1-2xKOA.X. KABEL
- — — — — DATA-1429/1-2xUTP, cat. 5e
- · · — · · — VEDENÍ DOMÁCÍHO DOROZUMVACÍHO ZAŘÍZENÍ SYKFY 5x2x0,5
- — — — — VEDENÍ PROPOJOVACÍ TERMOSTATY S REGULACÍ TEPELNĚHO ČERPADLA J-Y(SI)Y 4x1

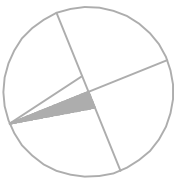

Ing. Hana Bezstarosti Belveder 188, Dobruška, 518 01 Tel.: 606 83 73 08 * IČO:67465935		Razítko :	
Zodpovědný projektant :	Ing. Hana Bezstarosti	Stupeň : dos	
Vypracoval :		Datum : 11/2021	
Investor :	Ekaterina Motveeva, U Slovanky 2440/5C, 182 00 Praha	Č. zak.: 61/2021/EL	
Místo stavby :	k.ú. Velká Hrošnice, p.p.č. 91/48	Měřítko : 1 : 50	
RODINNÝ DŮM TYP "BEATA"		Formát : 1 x A3	
D.1.4 – Elektroinstalace		Č. výkr. : E5	Podpis :
Půdorys 1.n.p. – sídboproudé rozvody		Č. paré :	