
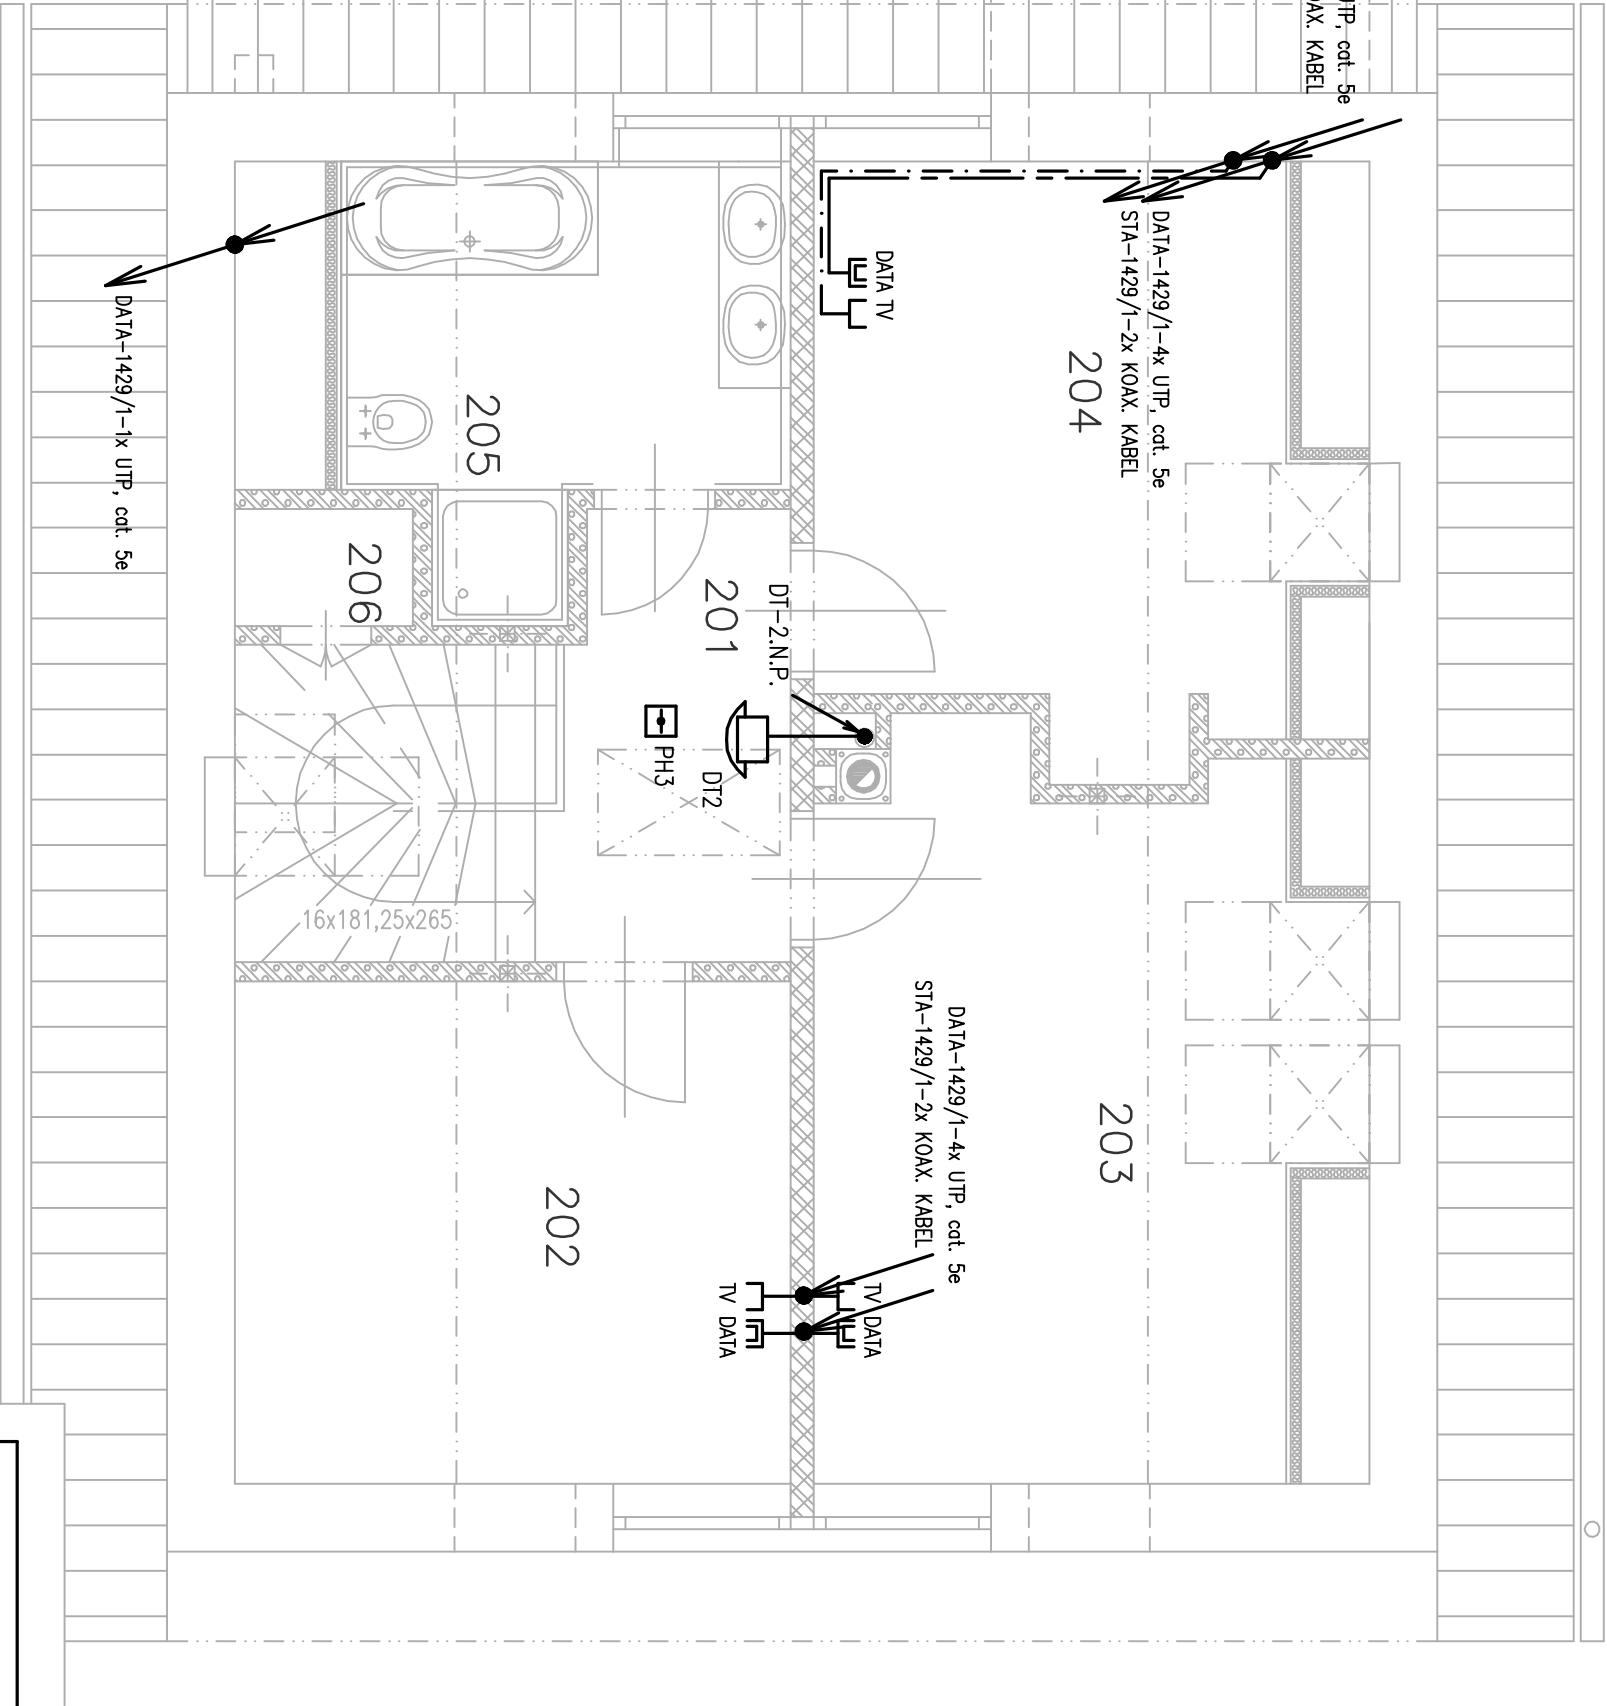


tabulka účelu místnosti

ČÍSLO	ÚČEL	PLOCHA (m ²)
201	HALA	4,61
202	LOŽNICE	12,22
203	POKOU	15,72
204	POKOU	12,15
205	LÁŽEŇ + WC	7,28
206	KOMORA	0,91

LEGENDA

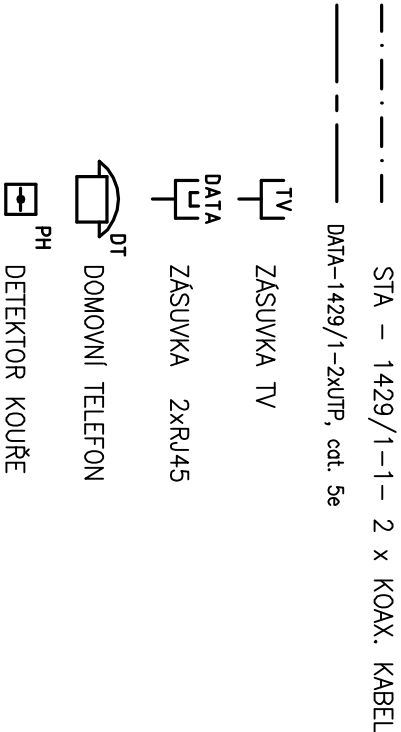

Ing. Hana Bezstarosti		Belveder 188, Dobruška, 518 01		Tel.: 606 83 73 08 * IČO:67465935		Razítko :
Zodpovědný projektant :		Ing. Hana Bezstarosti		<i>Hana Bezstarosti</i>		
Vyraboval :						
Investor : Ekaterina Matveeva, U Slovanky 2440/5C, 182 00 Praha		Č. zak.: 61/2021/EL				
Místo stavby : k.ú. Velká Hrašnice, p.p.č. 91/48		Měřítko : 1 : 50				
RODINNÝ DŮM TYP "BEATA"		Formát: 1 x A3				
		Č. výkr.: E6				
D.1.4 – Elektroinstalace		Č. paré :				Podpis :
Přodory 2.n.p. – sídoproudé rozvody						