


RD

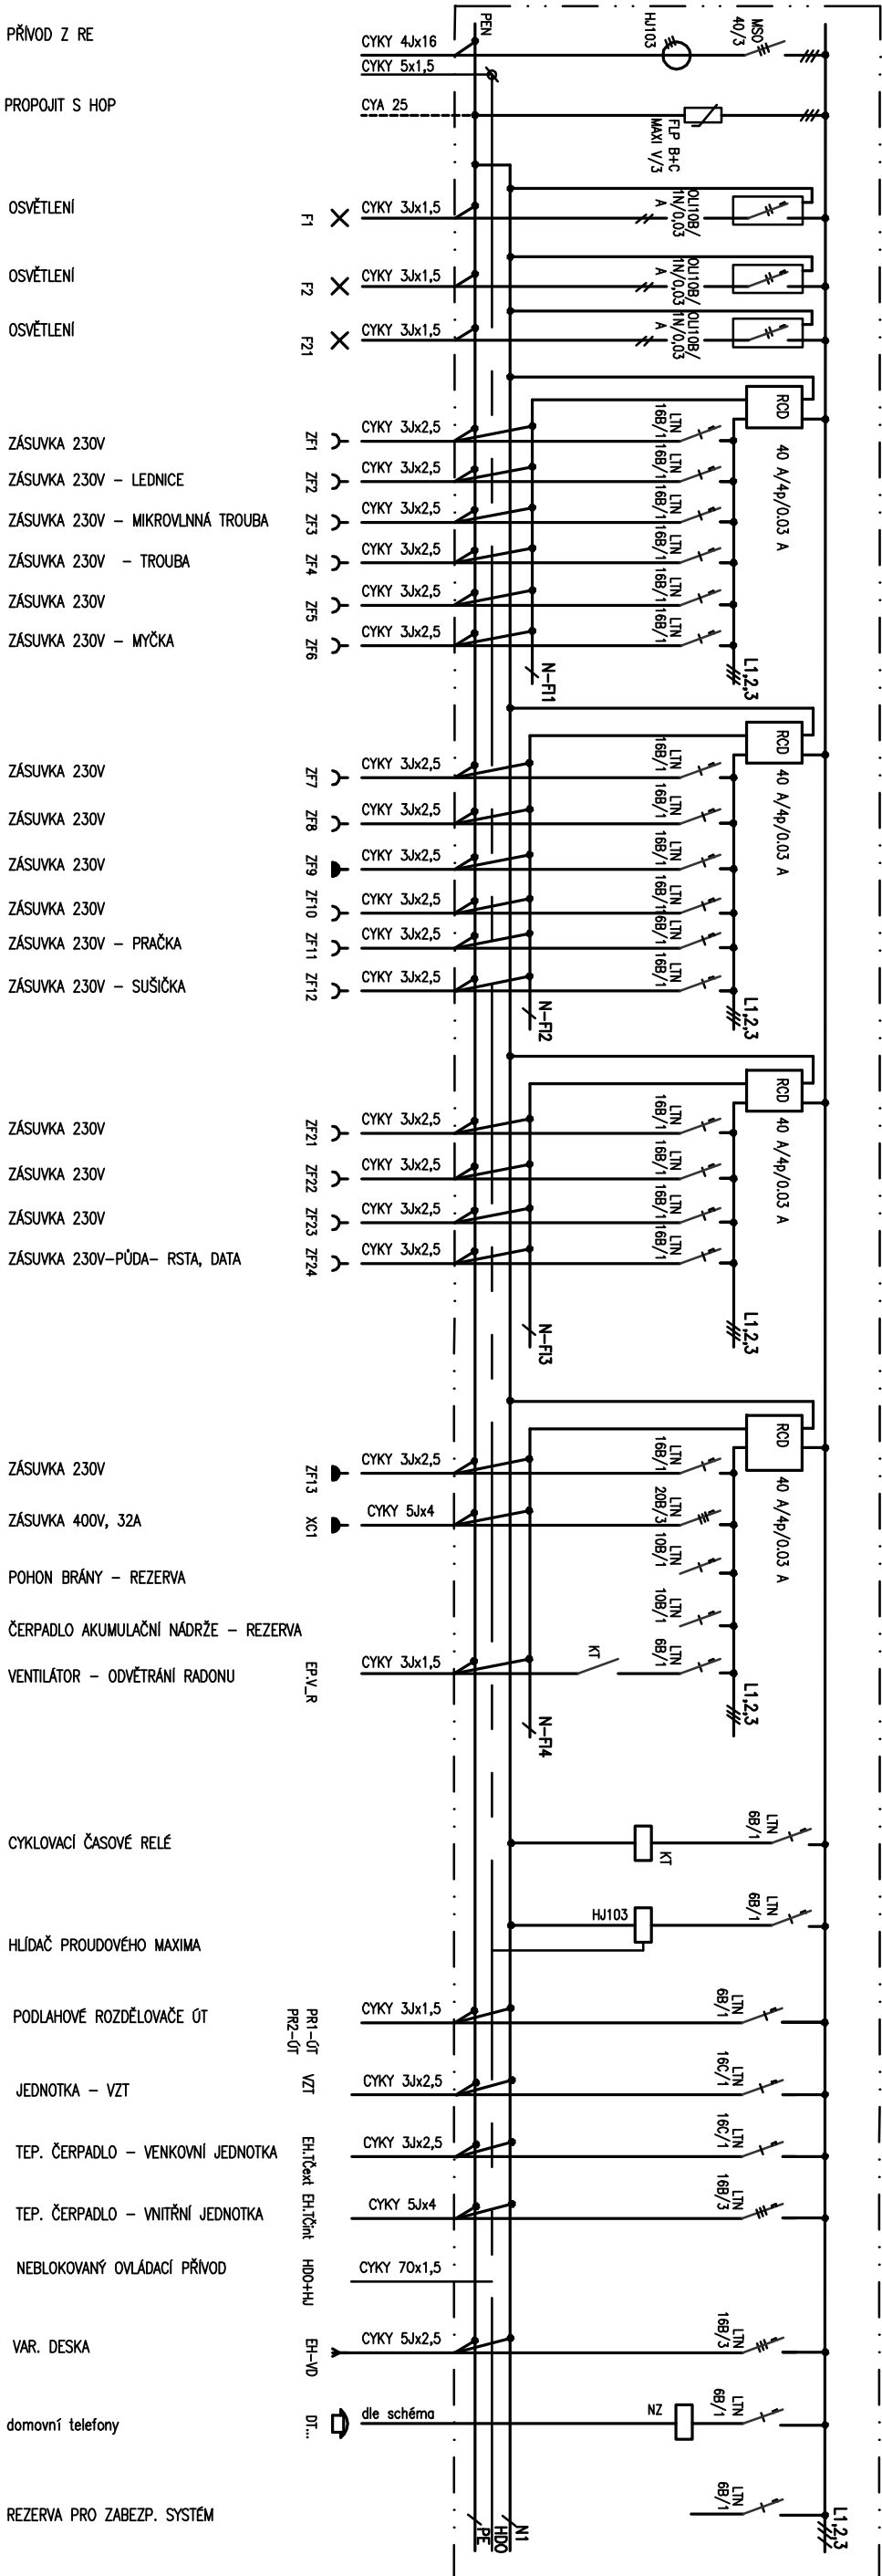

RD

Rozvodnice zapuštěná PRA25524 + PRA16524, 120 modulů, IP 40/20

rozměr rozvodnice - (570 x 930x 95) mm

- USPOŘÁDÁNÍ PŘÍSTROJŮ DLE ZVYKLOSTÍ PROVÁDĚCÍ FIRMY
- VNĚJŠÍ Vlivy : NORMÁLNÍ, AB5 VNITŘNÍ CHRÁNĚNÝ PROSTOR
- TYP POUŽITÉ ROZVODNICE DOHODNOUT PŘED MONTÁŽÍ SE STAVBOU (POŽADAVEK NIKY)
- PROUDOVÁ SOUSTAVA 3+PE+N, 50 Hz, 230/400 V, TN - C - S
- OCHRANA PŘED ÚRAZEM EL. PROUDEM DLE ČSN 33 2000-4-41 ed.2 AUTOMATICKÝM ODPOJENÍM OD ZDROJE,
- DOPLNĚKOVÁ PROUDOVÝM CHRÁNIČEM S VYBAVOVACÍM PROUDEM 30 mA.

Ing. Hana Bezstarosti		Belveder 188, Dobruška, 518 01		Tel.: 606 83 73 08 * IČO:67465935		Razítko :			
Zodpovědný projektant :									
Vyraboval :									
Investor : Ekaterina Matveeva, U Slovanky 2440/5C, 182 00 Praha									
Místo stavby : k.ú. Velká Hrošnice, p.p.č. 91/48									
RODINNÝ DŮM TYP "BEATA"									
Formát : 1 x A3									
Č. výkr. : E7									
Č. paré :									
D.1.4 – Elektroinstalace						Schéma rozvodnice RD			