



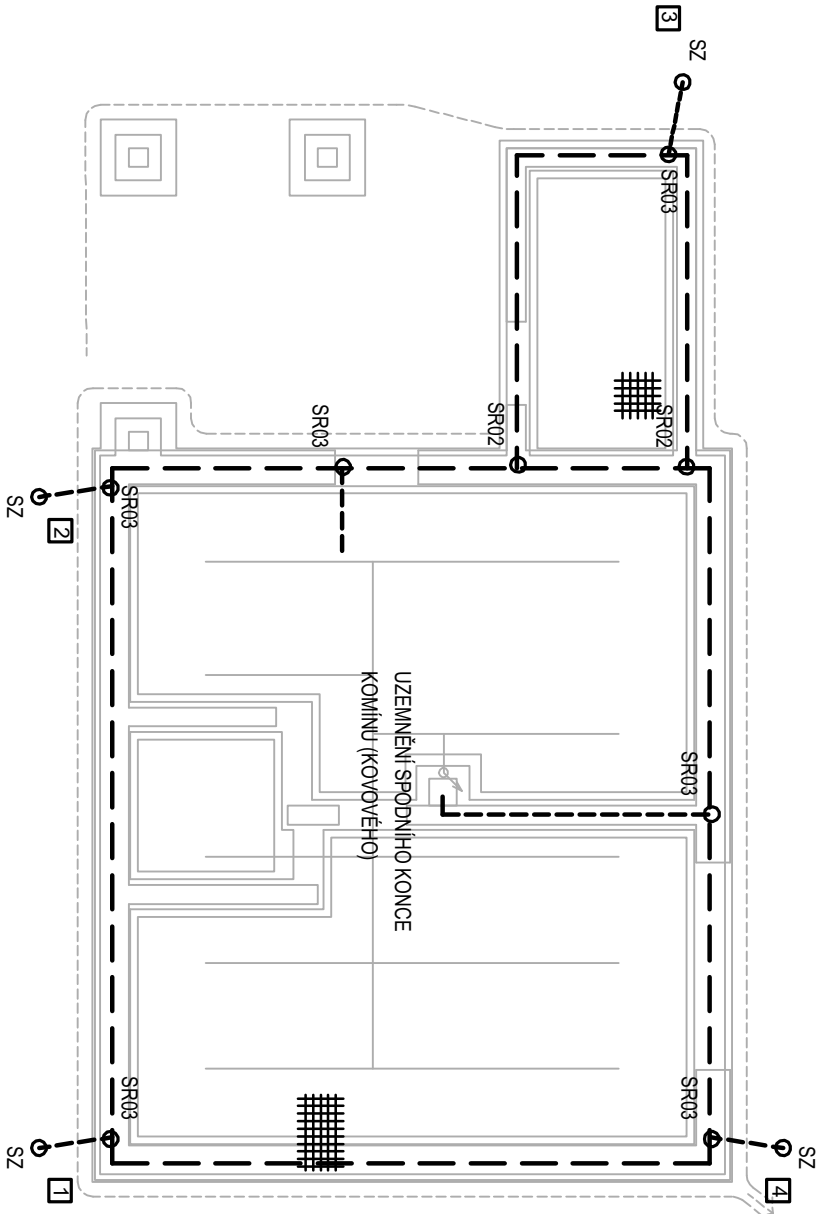

## LEGENDA

- VEDENÍ FeZn Ø 10 mm
- SYSTÉM UZEMNĚNÍ – OBVODOVÝ ZEMNIČ TYPU B – STROJENÝ ZÁKLADOVÝ ZEMNIČ
- ZEMNÍ PÁSEK BUDE V NĚKOLIKA MÍSTECH PEVNĚ PROPOJEN S KARI SÍTÍ
- SR02 ZEMNÍ SVORKA SPOJOVACÍ, PLOCHÉ VODIČE
- SR03 ZEMNÍ SVORKA SPOJOVACÍ, KULATÝ A PLOCHÝ VODIČ

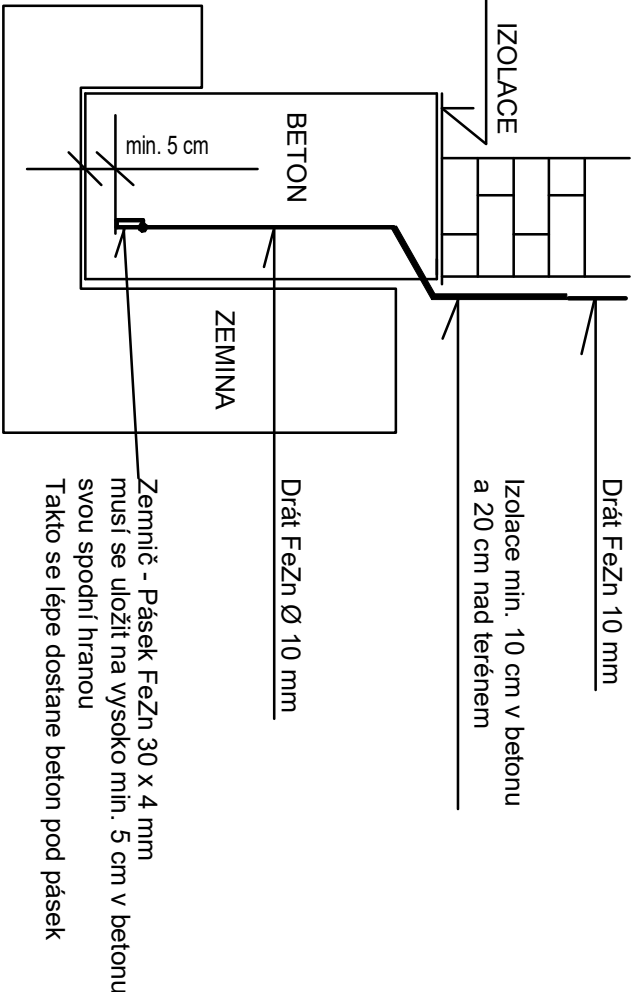

PROVEDENÍ HROMOSVODU MUSÍ ODPOVÍDAT ŘADĚ ČSN EN 62 305, ed.2.  
PROVEDENÍ UZEMNĚNÍ MUSÍ ODPOVÍDAT ČSN 33 2000–5–54 ed.3.

|                                                                 |  |                                               |  |                                   |  |           |
|-----------------------------------------------------------------|--|-----------------------------------------------|--|-----------------------------------|--|-----------|
| Ing. Hana Bezstarosti                                           |  | Belveder 188, Dobruška, 518 01                |  | Tel.: 606 83 73 08 * IČO:67465935 |  | Razítko : |
| Zodpovědný projektant :                                         |  | Ing. Hana Bezstarosti <i>Hana Bezstarosti</i> |  |                                   |  |           |
| Vyraboval :                                                     |  |                                               |  |                                   |  |           |
| Investor : Ekaterina Matveeva, U Slovanky 2440/5C, 182 00 Praha |  |                                               |  | Stupeň : dos                      |  |           |
| Místo stavby : k.ú. Velká Hrošnice, p.p.č. 91/48                |  |                                               |  | Datum : 11/2021                   |  |           |
|                                                                 |  |                                               |  | Č. zak.: 61/2021/EL               |  |           |
|                                                                 |  |                                               |  | Měřítko : 1 : 100                 |  |           |
| RODINNÝ DŮM<br>TYP "BEATA"                                      |  |                                               |  | Formát : 1 x A3                   |  |           |
|                                                                 |  |                                               |  | Č. výkr. : E8                     |  |           |
| D.1.4 – Elektroinstalace                                        |  |                                               |  | Č. paré :                         |  |           |
| Uzemnění                                                        |  |                                               |  |                                   |  |           |