


hodnoty oddělovací vzdálenosti s (m) jsou uvažovány pro km=0,5

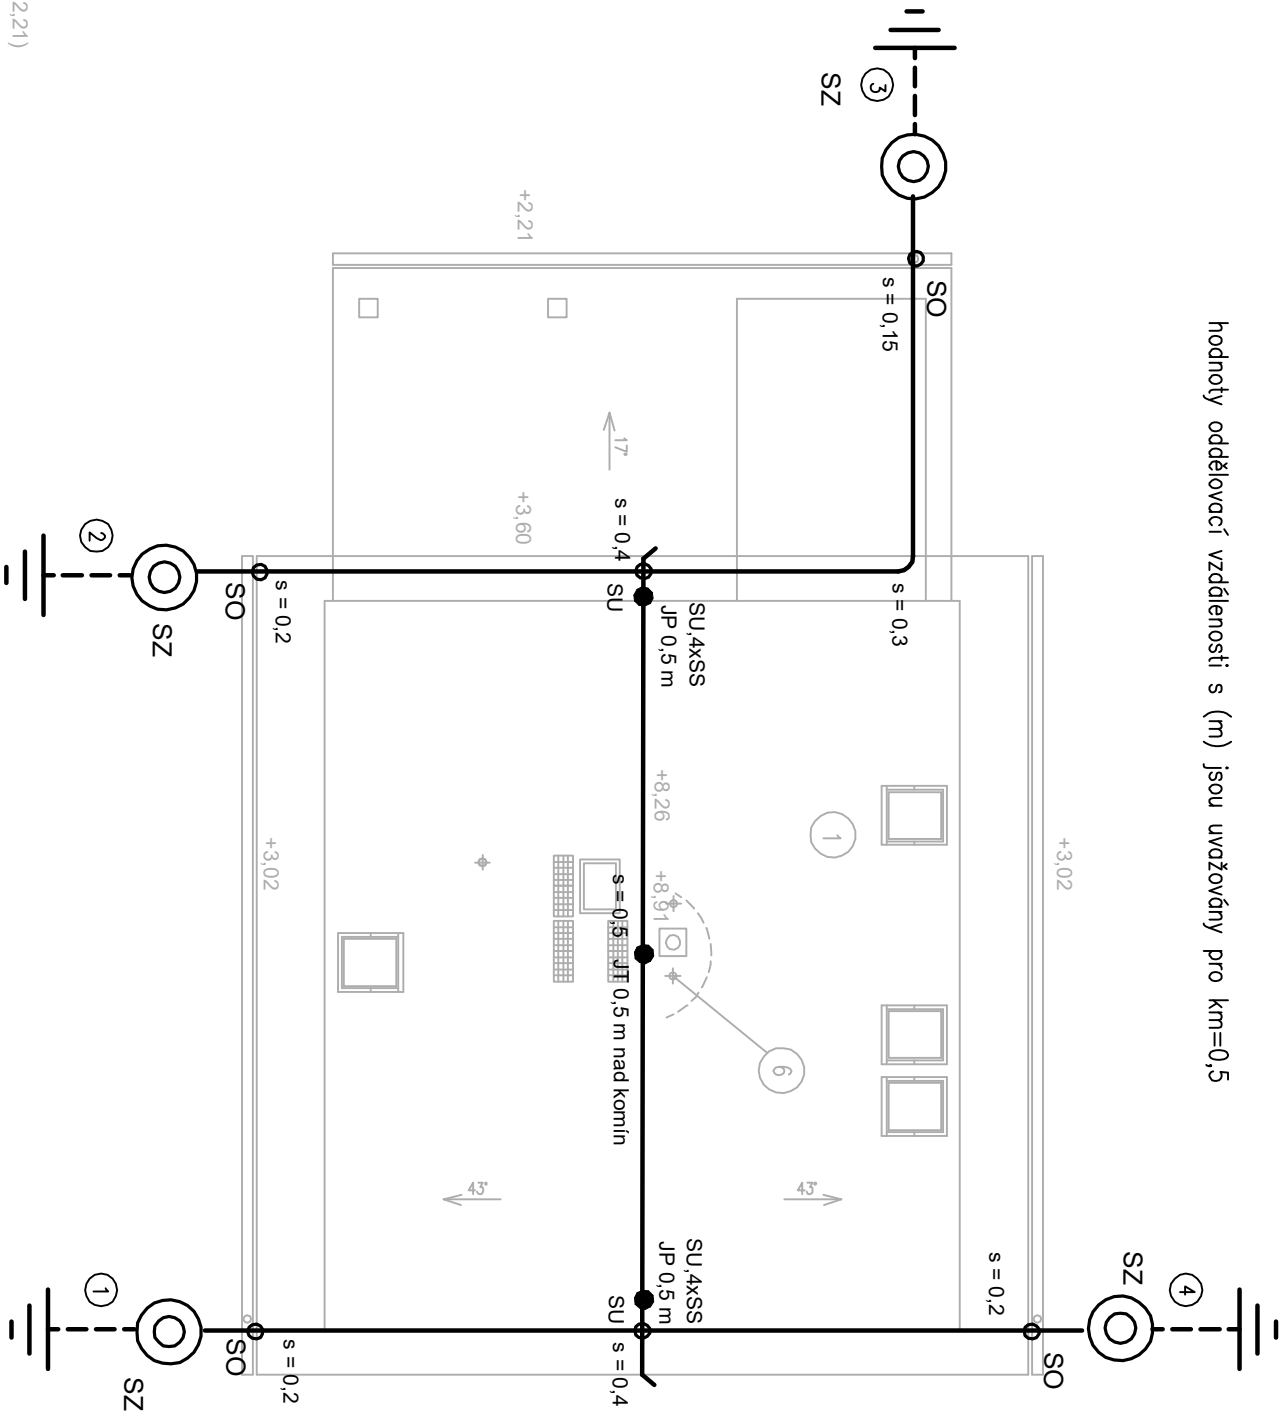

JIMACI VEDENÍ ALMGSI Ø 8 mm VČ. PODPĚR
(vzhledem k barvě krytiny je vhodné použití "barevného" drátu (Propster))

VEDENÍ FeZn Ø 10 mm

SYSTÉM UZEMNĚNÍ – OBVODOVÝ ZEMNIČ TYPU B – STROJENÝ ZÁKLADOVÝ ZEMNIČ FeZn 30x4

- JT JIMACÍ TYČ
- SO SVORKA OKAPOVÁ
- SU SVORKA UNIVERZÁLNÍ
- SS SVORKA SPOJOVACÍ
- SZ SVORKA ZKUŠEBNÍ
- ZT ZAVADĚCÍ TYČ

Poznámky:

- Třída LPS 3 – METODA OCHRANNÉHO ÚHLU
- SKLON STŘECHY (od svislice) 47°
- OCHRANNÝ ÚHEL VYTVOŘENÝ JIMACÍM VEDENÍ NA HŘEBENU (8,5 m) 63°
- OCHRANNÝ ÚHEL VYTVOŘENÝ POMOCNÝM JIMACÍM (9 m) 62°
- OCHRANNÝ ÚHEL VYTVOŘENÝ JIMACÍM U KOMÍNA (9,5 m) 61°
- druh tašky – Classic
- odstín – břidlicově černý

Dešťové žlaby a svody budou pronýťovány (5).
Spodní konce dešťových svodů a komínu (v případě celokovového) budou propojeny s uzemněním.
Hromosvody a návaznost na uzemnění jsou navrženy podle ČSN EN 62 305
Všechny svody budou propojeny na zemnič typu B.
Pro objekt jsou navrženy 4 ks svodů z jímací soustavy.
Při přechodu jednotlivých svodů do země je nutno na nich provést protikoroziní ochranu min. 20 cm nad terénem a 10 cm v betonu dle ČSN 33 2000–5–54 čl. NA. 10.6.
Hodnota odporu uzemnění by měla být do 10 Ohmů dle ČSN EN 62 305.

ANTÉNNÍ STOŽÁR BUDE UMÍSTĚN V LPZ 0_g, JINAK MUSÍ BÝT OPATŘEN
VLASTNÍM ODDÁLENÝM TYČOVÝM JIMACÍM.
SVOD OD ANTÉNY MUSÍ BÝT UZEMNĚN DO HOP PŘES BLESKOJISTKY.

PROVEDENÍ HROMOSVODU MUSÍ ODPOVÍDAT ŘADĚ ČSN EN 62 305, ed.2.
PROVEDENÍ UZEMNĚNÍ MUSÍ ODPOVÍDAT ČSN 33 2000–5–54 ed.3.

Ing. Hana Bezstarosti		Belveder 186, Dobruška, 518 01		Tel.: 606 83 73 08 * IČO:67465935		Razítko :
Zodpovědný projektant :		Ing. Hana Bezstarosti				
Vyraboval :		<i>Hana Bezstarosti</i>				
Investor : Ekaterina Matveeva, U Slovanky 2440/5C, 182 00 Praha		Datum : 11/2021				
Místo stavby : k.ú. Velká Hroštica, p.p.č. 91/48		Č. zak.: 61/2021/EL				
		Měřítko : 1 : 100				
RODINNÝ DŮM TYP "BEATA"		Formát : 1 x A3				
		Č. výkr. : E9				
D.1.4 – Elektroinstalace		Č. paré :		Podpis :		
Hromosvody						