


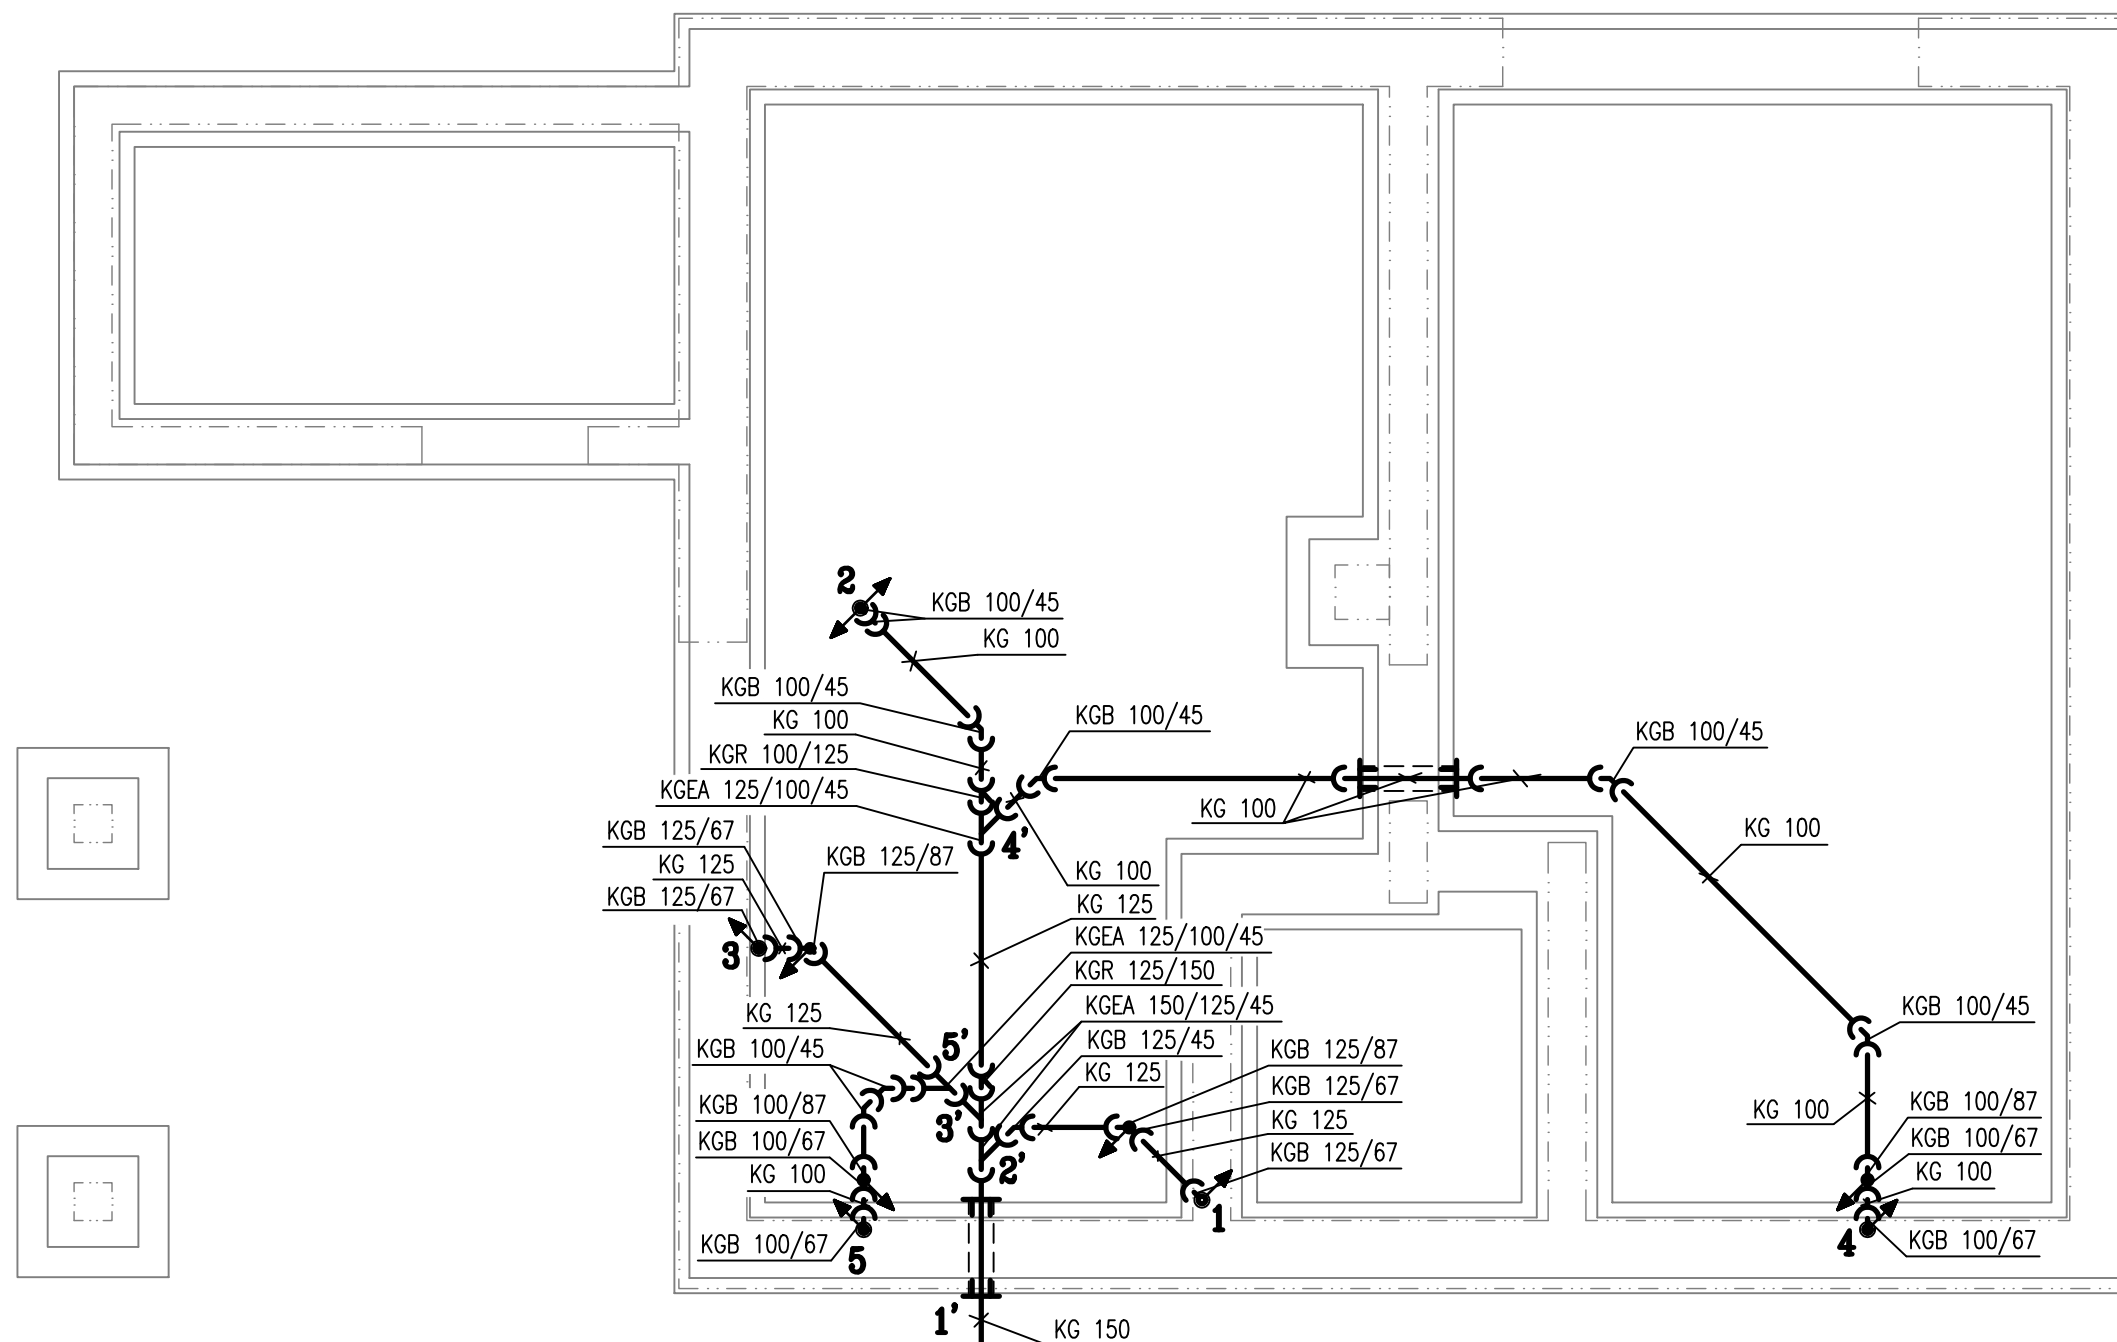

legenda Z.T.I.



ležatá kanalizace – KG systém z PVC

pokyny pro montáž – viz Technická zpráva

legenda zařizovacích předmětů

– viz Výpis zařizovacích předmětů

POZNÁMKA

Prostupy základovou deskou
utěsnit pomocí těsnících manžet
HL 800/110

Paré číslo



Hlavní projektant: Ing. Karel Peterka		Zodpovědný projektant: Ing. Karel Peterka		Vypracoval: Lukáš Materna	
Místo: k.ú. Velká Hraštice, p.p.č. 91/48			Stavebník: Ekaterina Matveeva, U Slovanky 2440/5C, Praha		
Název akce: RODINNÝ DŮM "BEÁTA"				Formát	2xA4
				Datum	listopad 2021
				Stupeň PD	typový projekt
				Č.zakázky	030/21/TP
Příloha: ZDRAVOTNĚ TECHNICKÉ INSTALACE KANALIZACE – ZÁKLADY				Měřítko:	Č. přílohy:
				—	D.1.4.Z.2