



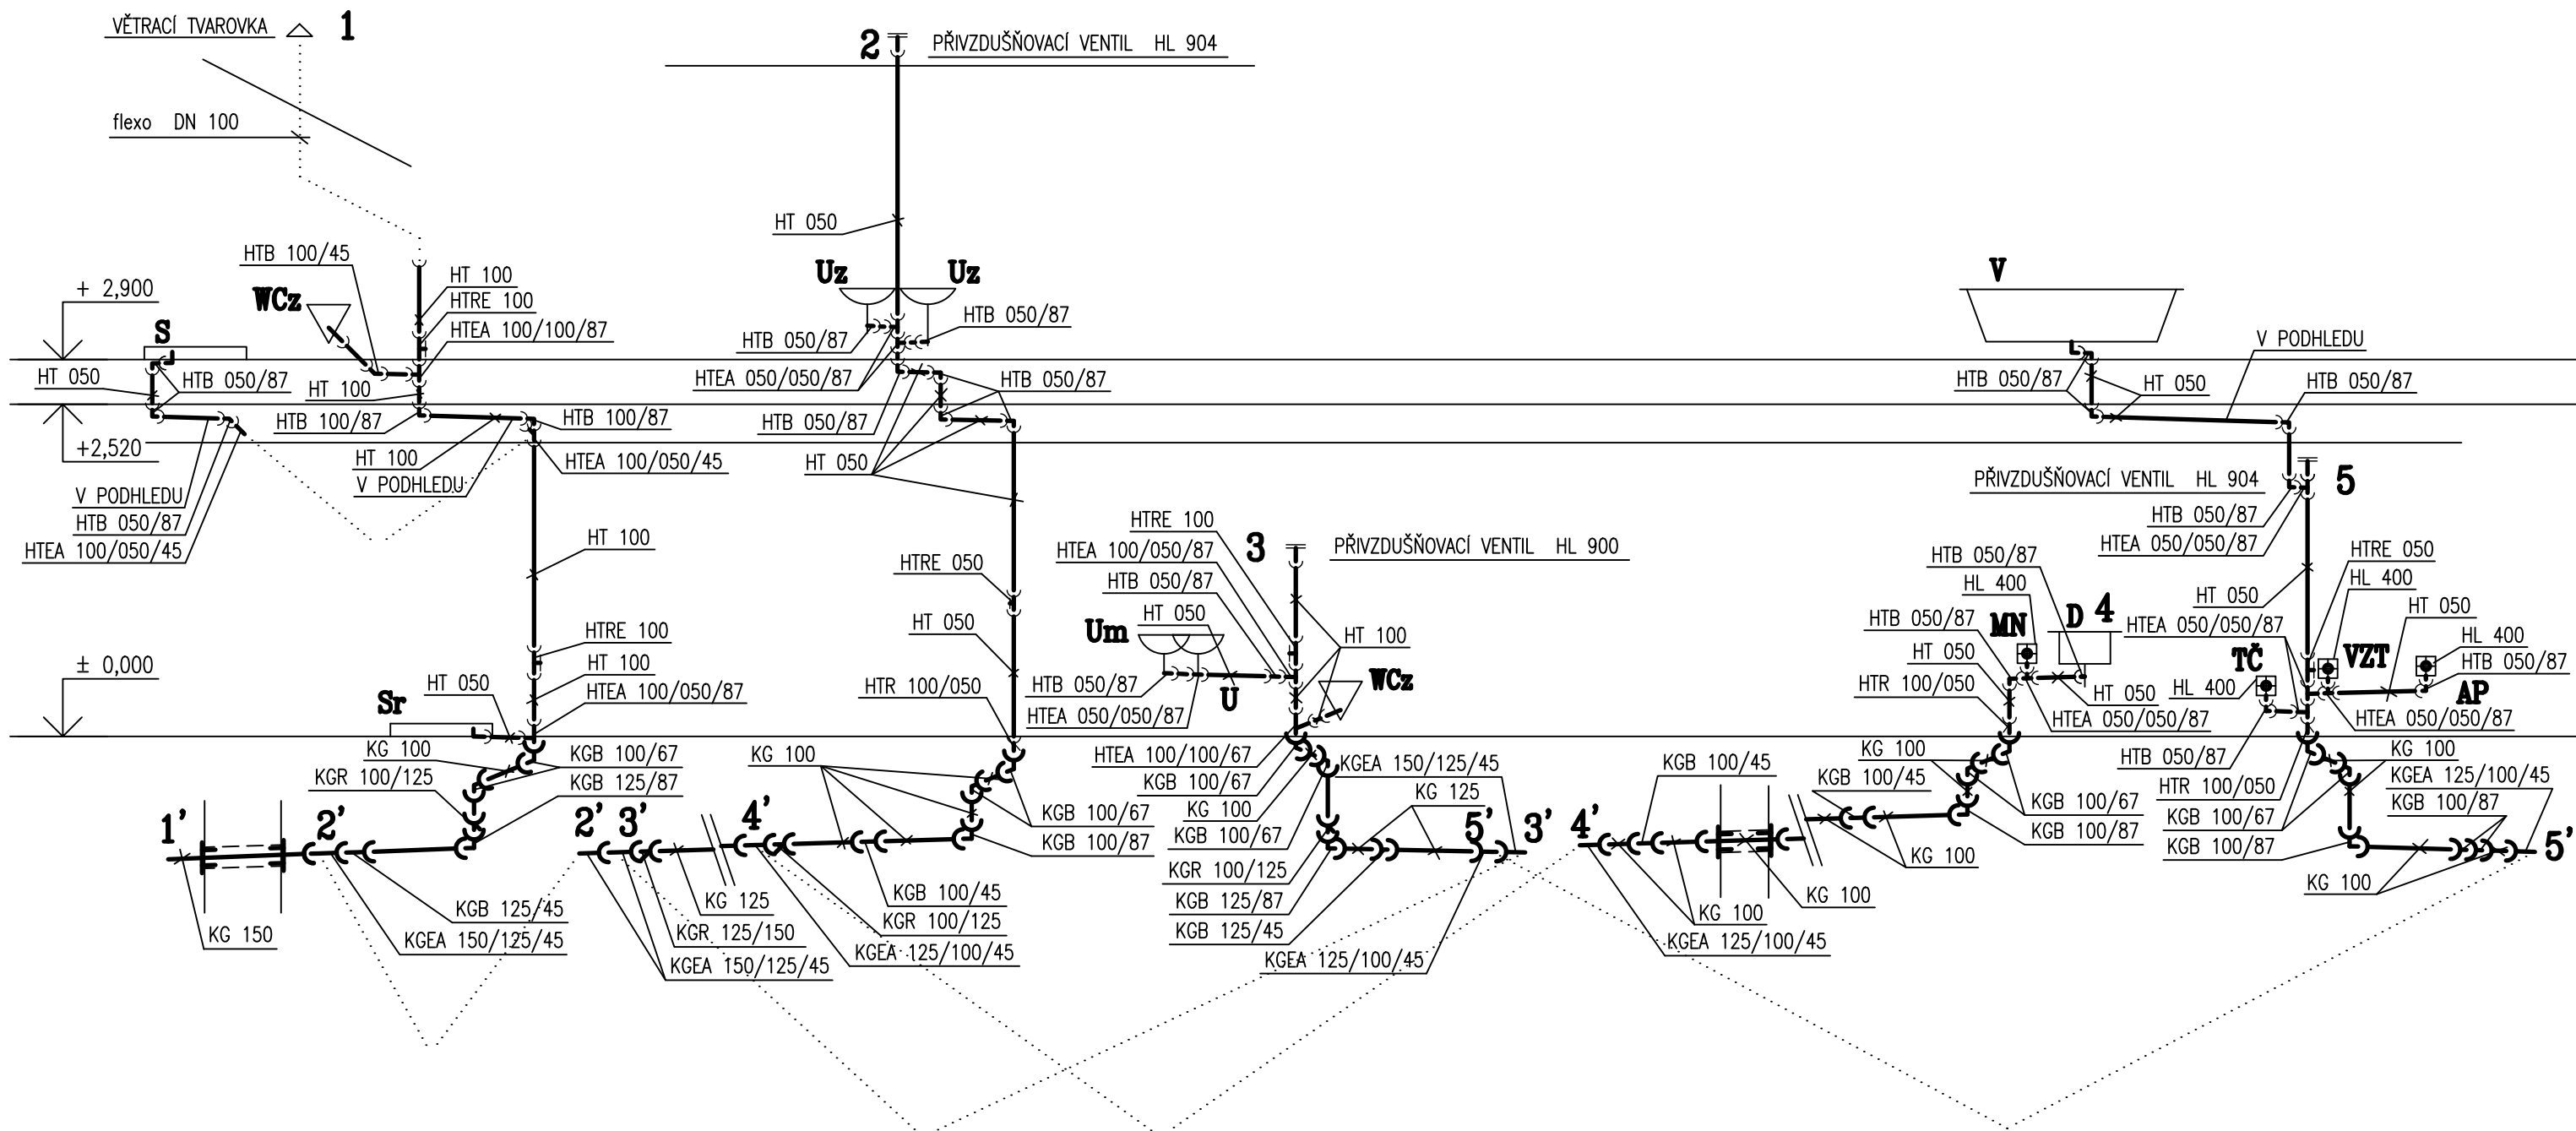

legenda Z.T.I.

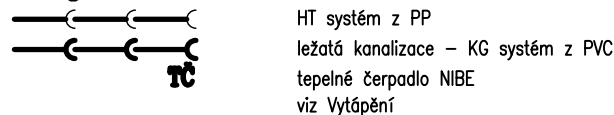

pokyny pro montáž – viz Technická zpráva
legenda zařizovacích předmětů
– viz Výpis zařizovacích předmětů

POZNÁMKA

Prostupy základovou deskou
utěsnit pomocí těsnících manžet
HL 800/110

Paré číslo



Hlavní projektant: Ing. Karel Peterka	Zodpovědný projektant: Ing. Karel Peterka	Vypracoval: Lukáš Materna
Místo: k.ú. Velká Hraštice, p.p.č. 91/48	Stavebník: Ekaterina Matveeva, U Slovanky 2440/5C, Praha	
Název akce: RODINNÝ DŮM "BEÁTA"		Formát: 2xA4
		Datum: listopad 2021
		Stupeň PD: typový projekt
		Č.zakázky: 030/21/TP
Příloha: ZDRAVOTNĚ TECHNICKÉ INSTALACE KANALIZACE – ŘEZY SVODY		Měřítko: Č. přílohy: D.1.4.Z.5