


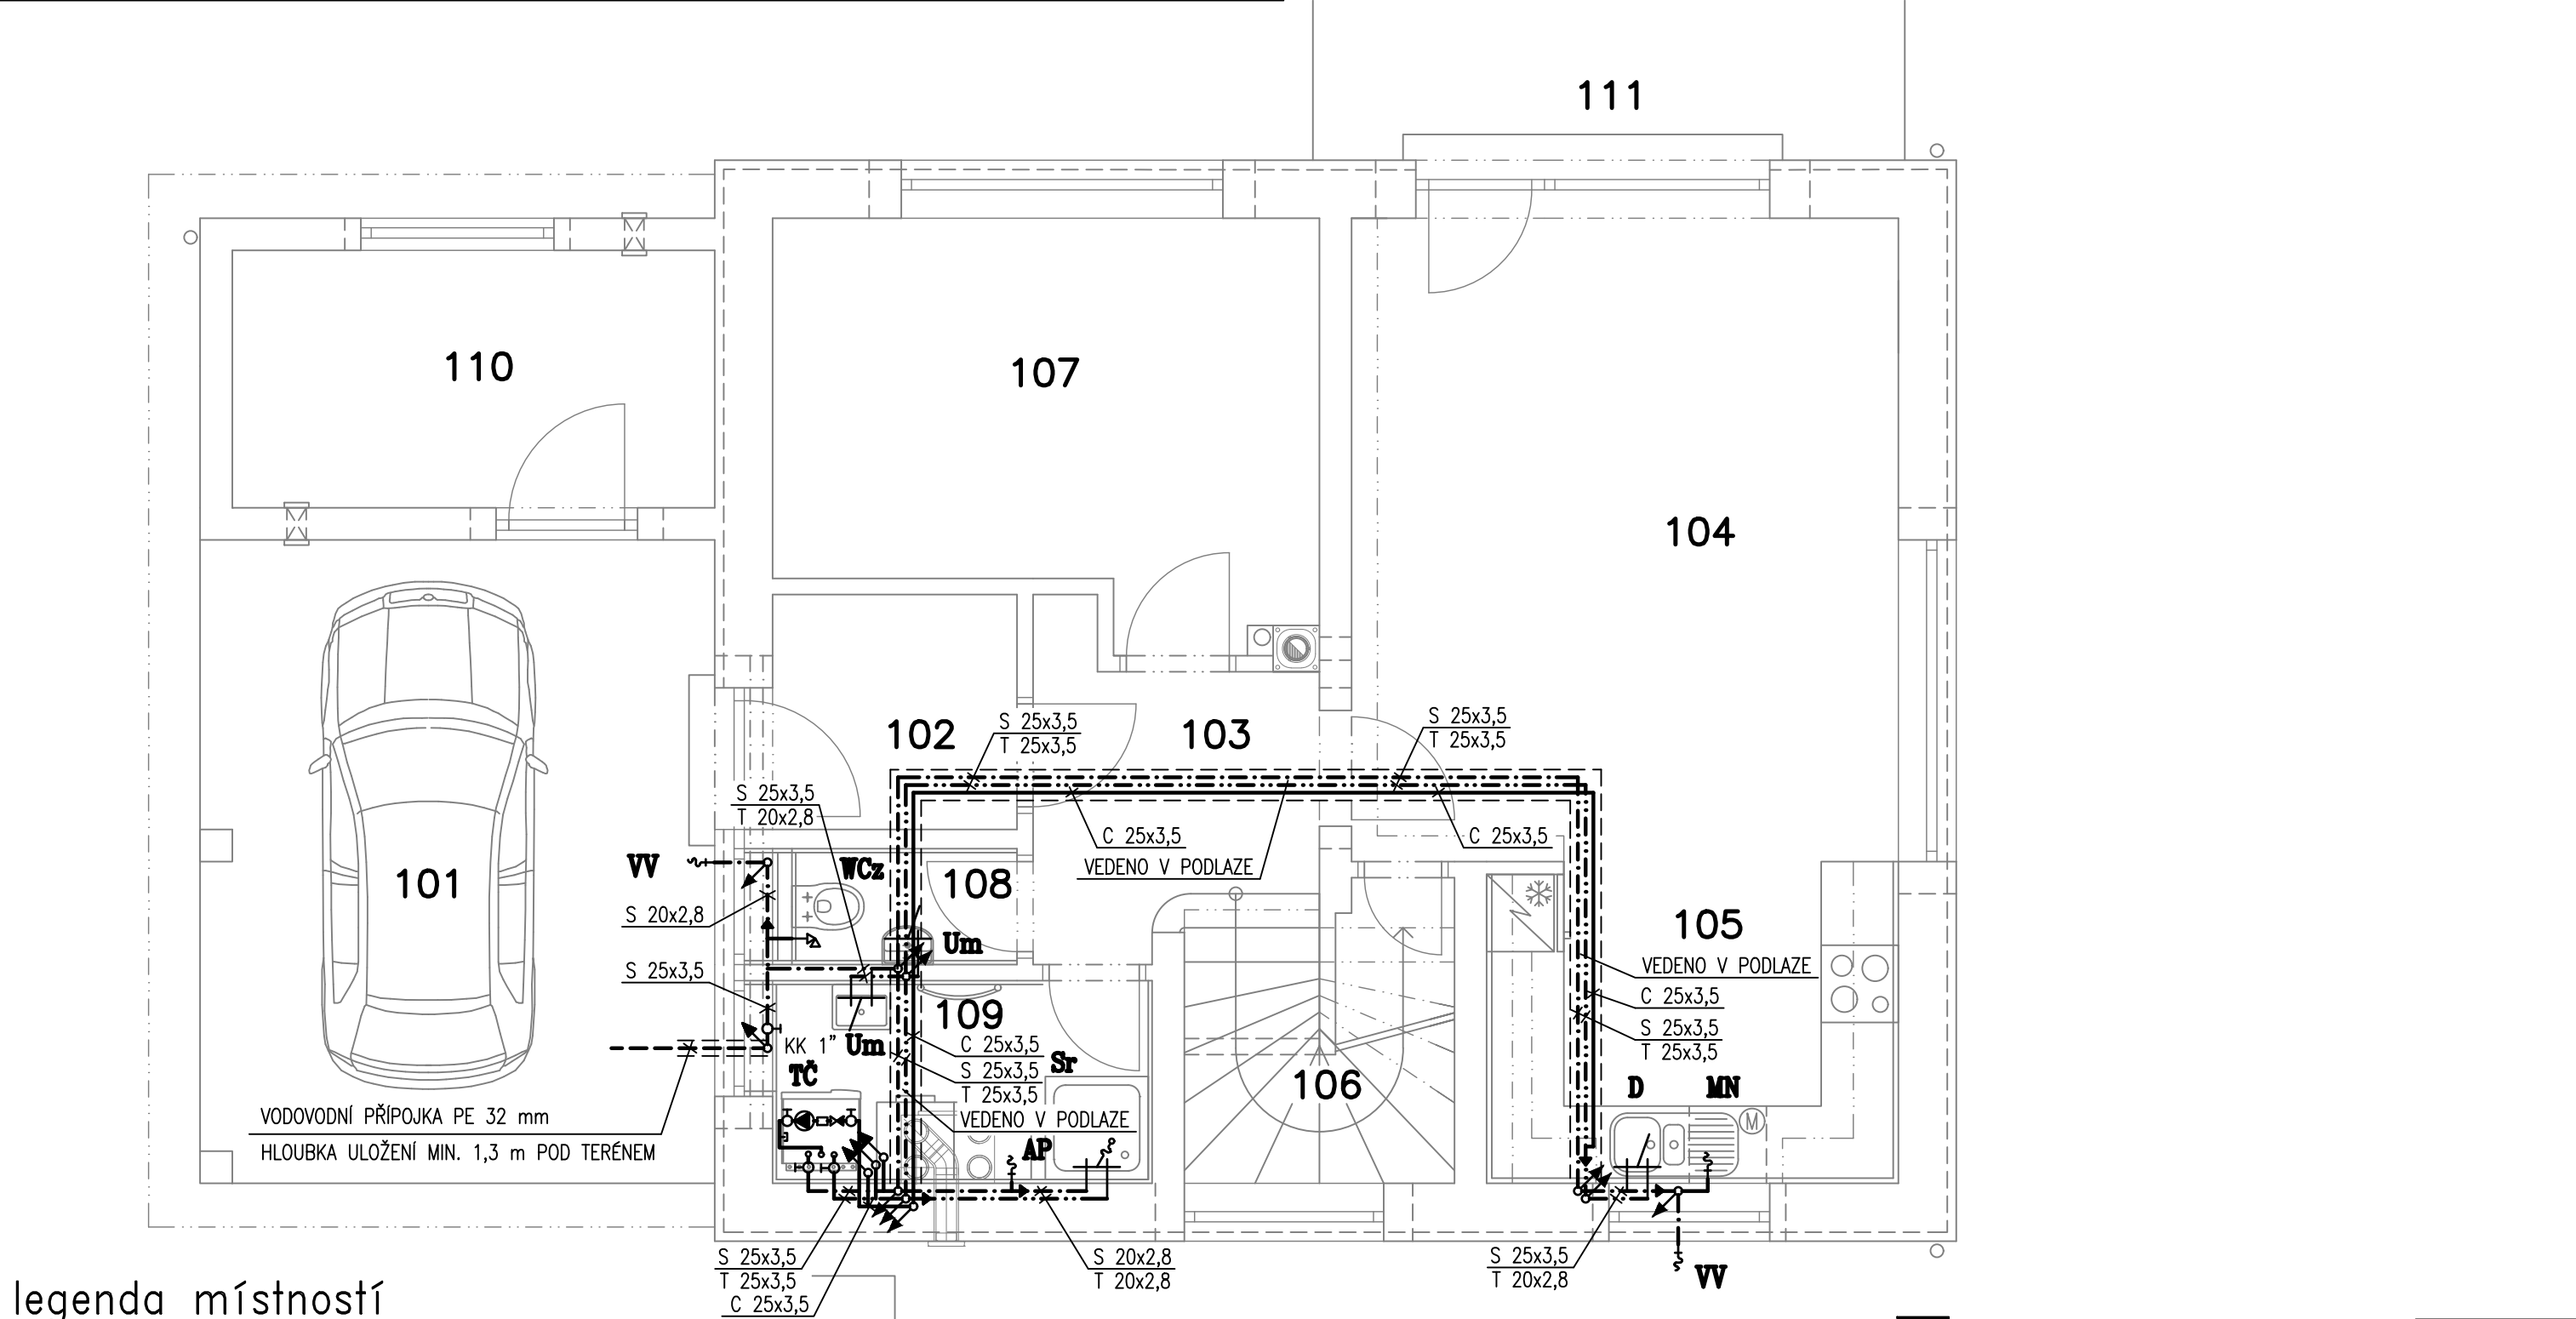

legenda místností

ČÍSLO	ÚČEL	PLOCHA (m ²)
101	ZAVĚTRÍ	19,81
102	ZÁDVEŘÍ	3,51
103	HALA	4,67
104	OBÝVACÍ POKOJ	21,25
105	KUCHYŇ	7,94
106	SPIŽ	3,34
107	PRACOVNA	12,72
108	WC	1,71
109	SPRCHA + DOMÁCÍ PRÁCE	4,65
110	JÍZDNÍ KOLA, ZAHRADNÍ NÁŘADÍ	7,50
111	TERASA	13,80

legenda Z.T.I.

—	voda studená
—	voda teplá
—	vodovodní přípojka
—	cirkulační potrubí
⊘	uzavírací armatura
⊘	vypouštěcí armatura
□	plnopřítokový vodovodní filtr
⋈	zpětná vodovodní klapka
●	cirkulační čerpadlo
⊙	Wilo-Star-Z NOVA C
⊙	tepelné čerpadlo NIBE
⊙	viz Vytápění
⊙	

pokyny pro montáž – viz Technická zpráva
legenda zařizovacích předmětů
– viz Výpis zařizovacích předmětů

POZNÁMKA

Písmena S, T, C označují trubky pro studenou, teplou vodu a pro cirkulační potrubí.

V místě křížení s potrubím vytápění budou rozvody vody uloženy nad potrubím vytápění.

Napojení tepelného čerpadla provést podle montážních podkladů výrobce

Vodoměrná sestava bude umístěna ve vodoměrné šachtě.



Paré číslo

Hlavní projektant: Ing. Karel Peterka	Zodpovědný projektant: Ing. Karel Peterka	Vypracoval: Lukáš Materna
Místo: k.ú. Velká Hraštice, p.p.č. 91/48	Stavebník: Ekaterina Matveeva, U Slovanky 2440/5C, Praha	
Název akce: RODINNÝ DŮM "BEÁTA"		Formát: 2xA4
Příloha: ZDRAVOTNĚ TECHNICKÉ INSTALACE VODOVOD – PŘÍZEMÍ		Datum: listopad 2021
		Stupeň PD: typový projekt
		Č.zakázky: 030/21/TP
		Měřítko: —
		Č. přílohy: D.1.4.Z.6