


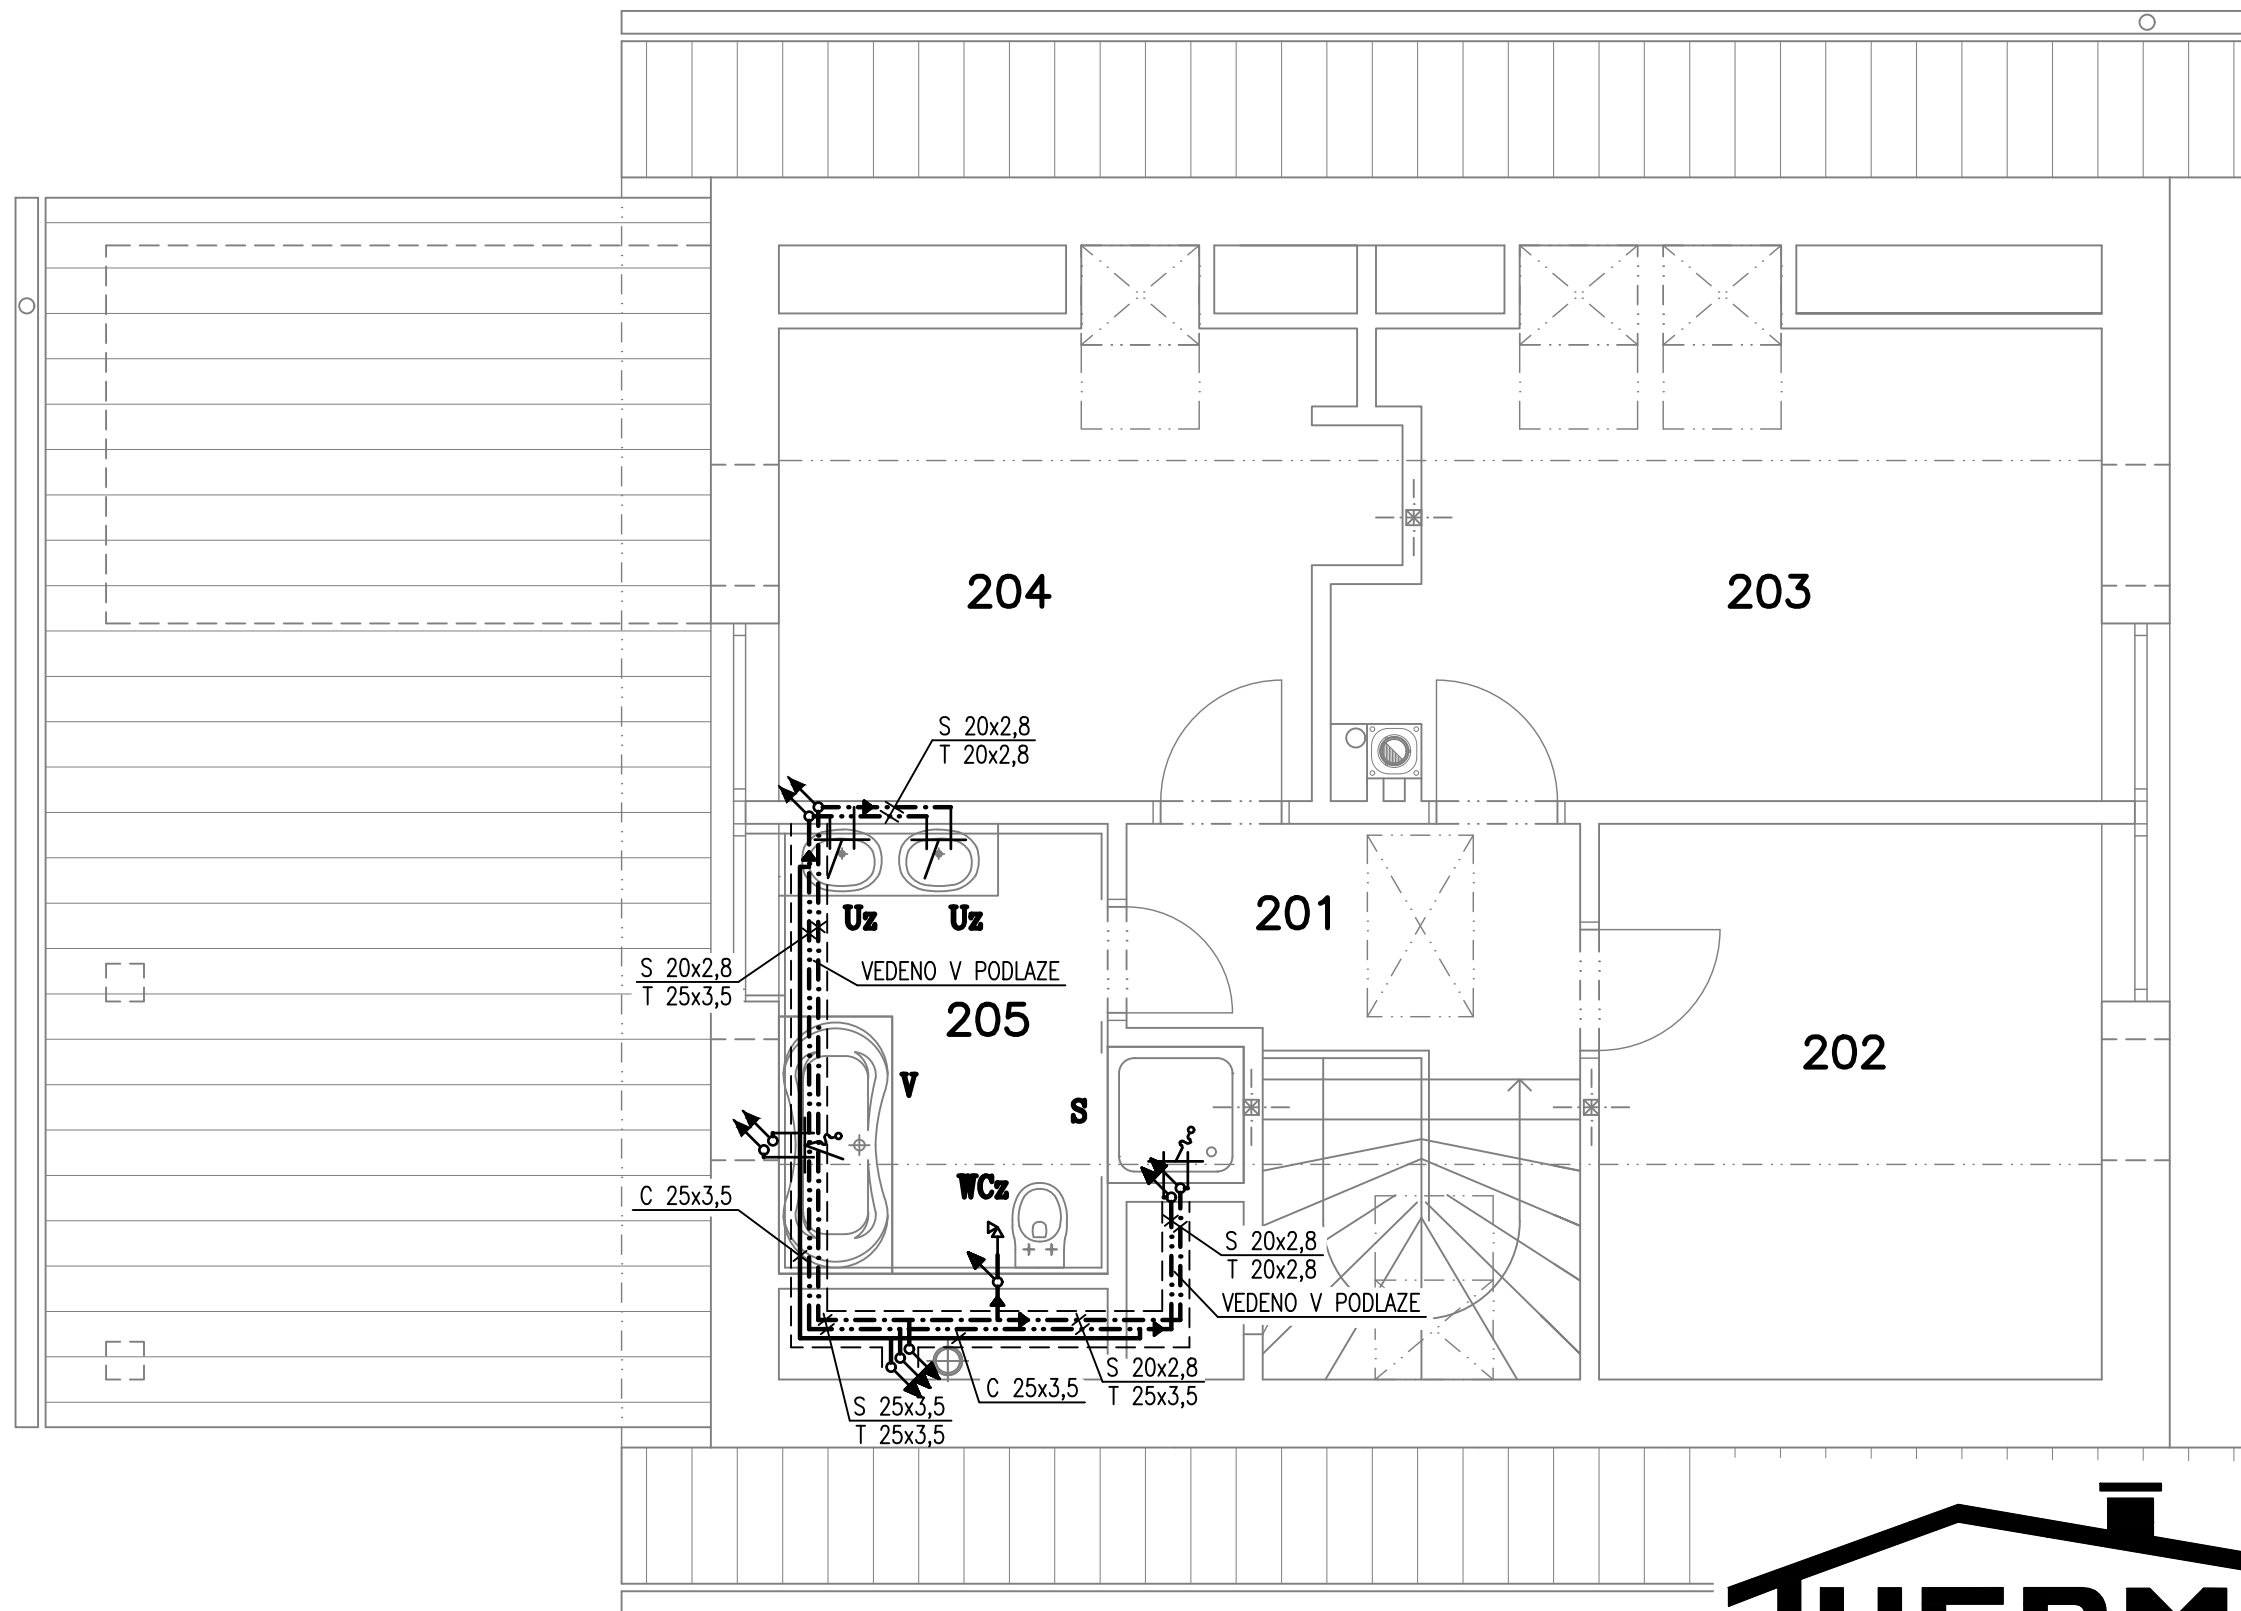

Paré číslo

legenda místností

ČÍSLO	ÚČEL	PLOCHA (m ²)
201	HALA	4,61
202	LOŽNICE	12,22
203	POKŮJ	15,72
204	POKŮJ	12,15
205	LÁŽEŇ + WC	7,28
206	KOMORA	0,91

legenda Z.T.I.

---	voda studená
---	voda teplá (TUV)
---	cirkulační potrubí
Ø	uzavírací armatura

pokyny pro montáž – viz Technická zpráva
legenda zařizovacích předmětů
– viz Výpis zařizovacích předmětů

POZNÁMKA

Písmena S, T, C označují trubky pro studenou, teplou vodu a pro cirkulační potrubí.

V místě křížení s potrubím vytápění budou rozvody vody uloženy nad potrubím vytápění.



Hlavní projektant: Ing. Karel Peterka	Zodpovědný projektant: Ing. Karel Peterka	Vypracoval: Lukáš Materna
Místo: k.ú. Velká Hraštice, p.p.č. 91/48	Stavebník: Ekaterina Matveeva, U Slovanky 2440/5C, Praha	
Název akce: RODINNÝ DŮM "BEÁTA"		Formát: 2xA4
		Datum: listopad 2021
		Stupeň PD: typový projekt
		Č.zakázky: 030/21/TP
Příloha: ZDRAVOTNĚ TECHNICKÉ INSTALACE VODOVOD – PODKROVÍ		Měřítko: — Č. přílohy: D.1.4.Z.7