


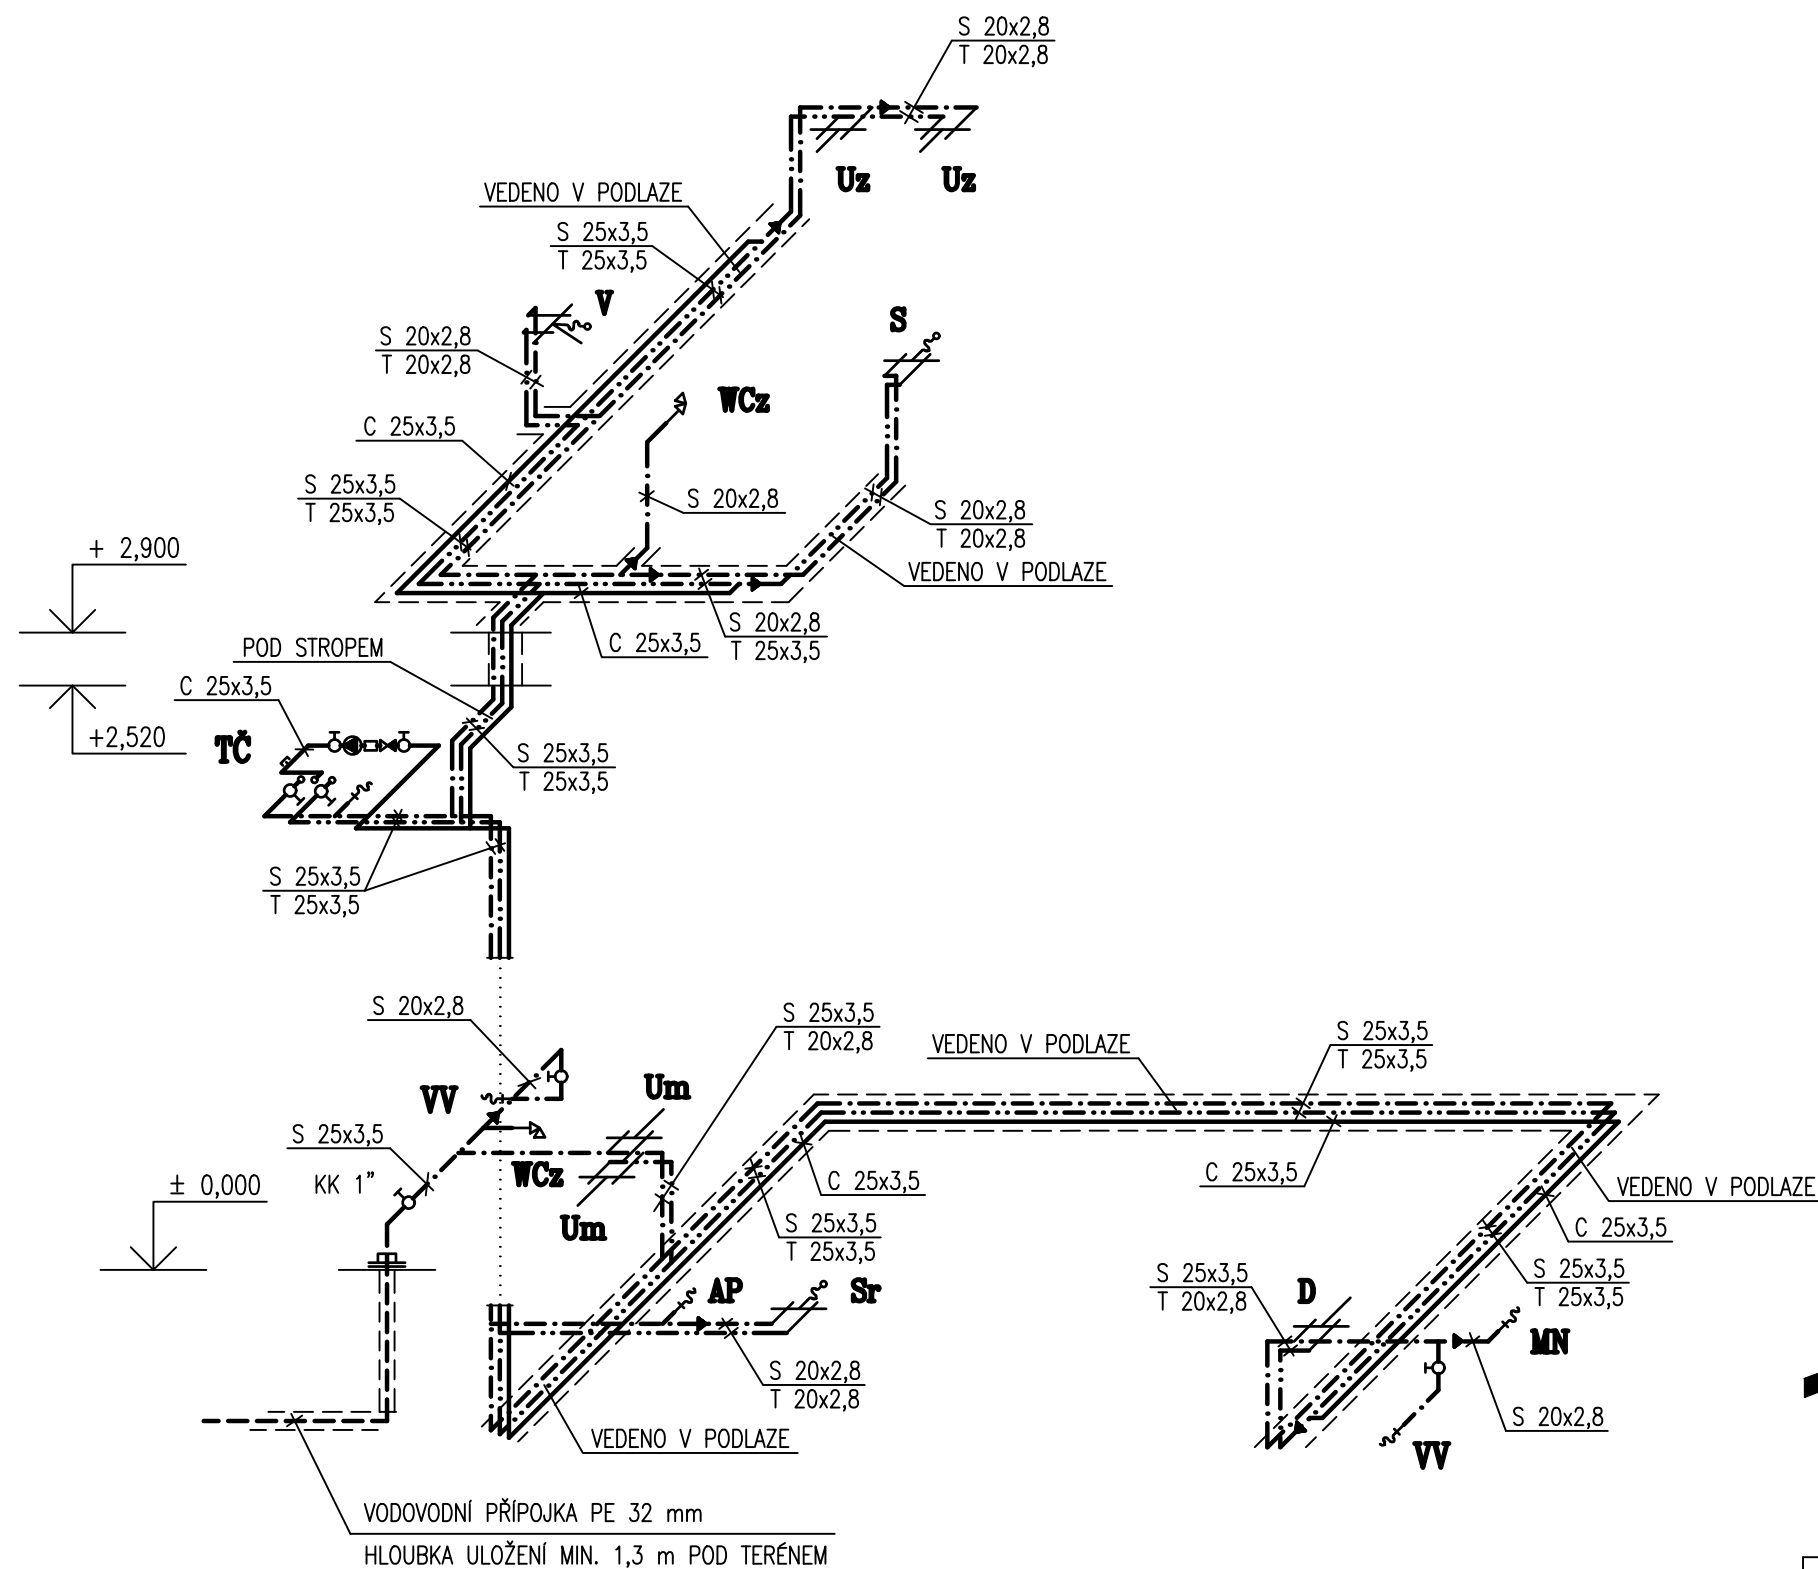

legenda Z.T.I.

-----	voda studená
-----	voda teplá
-----	vodovodní přípojka
-----	cirkulační potrubí
⊗	uzavírací armatura
⊥	vypouštěcí armatura
□	plnopřítokový vodovodní filtr
⌞	zpětná vodovodní klapka
⊙	cirkulační čerpadlo
⊙	Wilo-Star-Z NOVA C
⊙	tepelné čerpadlo NIBE
⊙	viz Vytápění

pokyny pro montáž – viz Technická zpráva

legenda zařizovacích předmětů

– viz Výpis zařizovacích předmětů

POZNÁMKA

Písmena S, T, C označují trubky pro studenou, teplou vodu a pro cirkulační potrubí.

V místě křížení s potrubím vytápění budou rozvody vody uloženy nad potrubím vytápění.

Napojení tepelného čerpadla provést podle montážních podkladů výrobce.

Vodoměrná sestava bude umístěna ve vodoměrné šachtě.

THERMO
projektový ateliér **PLUS**

Paré číslo

Hlavní projektant: Ing. Karel Peterka	Zodpovědný projektant: Ing. Karel Peterka	Vypracoval: Lukáš Materna
Místo: k.ú. Velká Hraštice, p.p.č. 91/48	Stavebník: Ekaterina Matveeva, U Slovanky 2440/5C, Praha	
Název akce: RODINNÝ DŮM "BEÁTA"		Formát: 2xA4
		Datum: listopad 2021
		Stupeň PD: typový projekt
		Č.zakázky: 030/21/TP
Příloha: ZDRAVOTNĚ TECHNICKÉ INSTALACE VODOVOD – SCHEMA ROZVODŮ		Měřítko: Č. přílohy: — D.1.4.Z.8