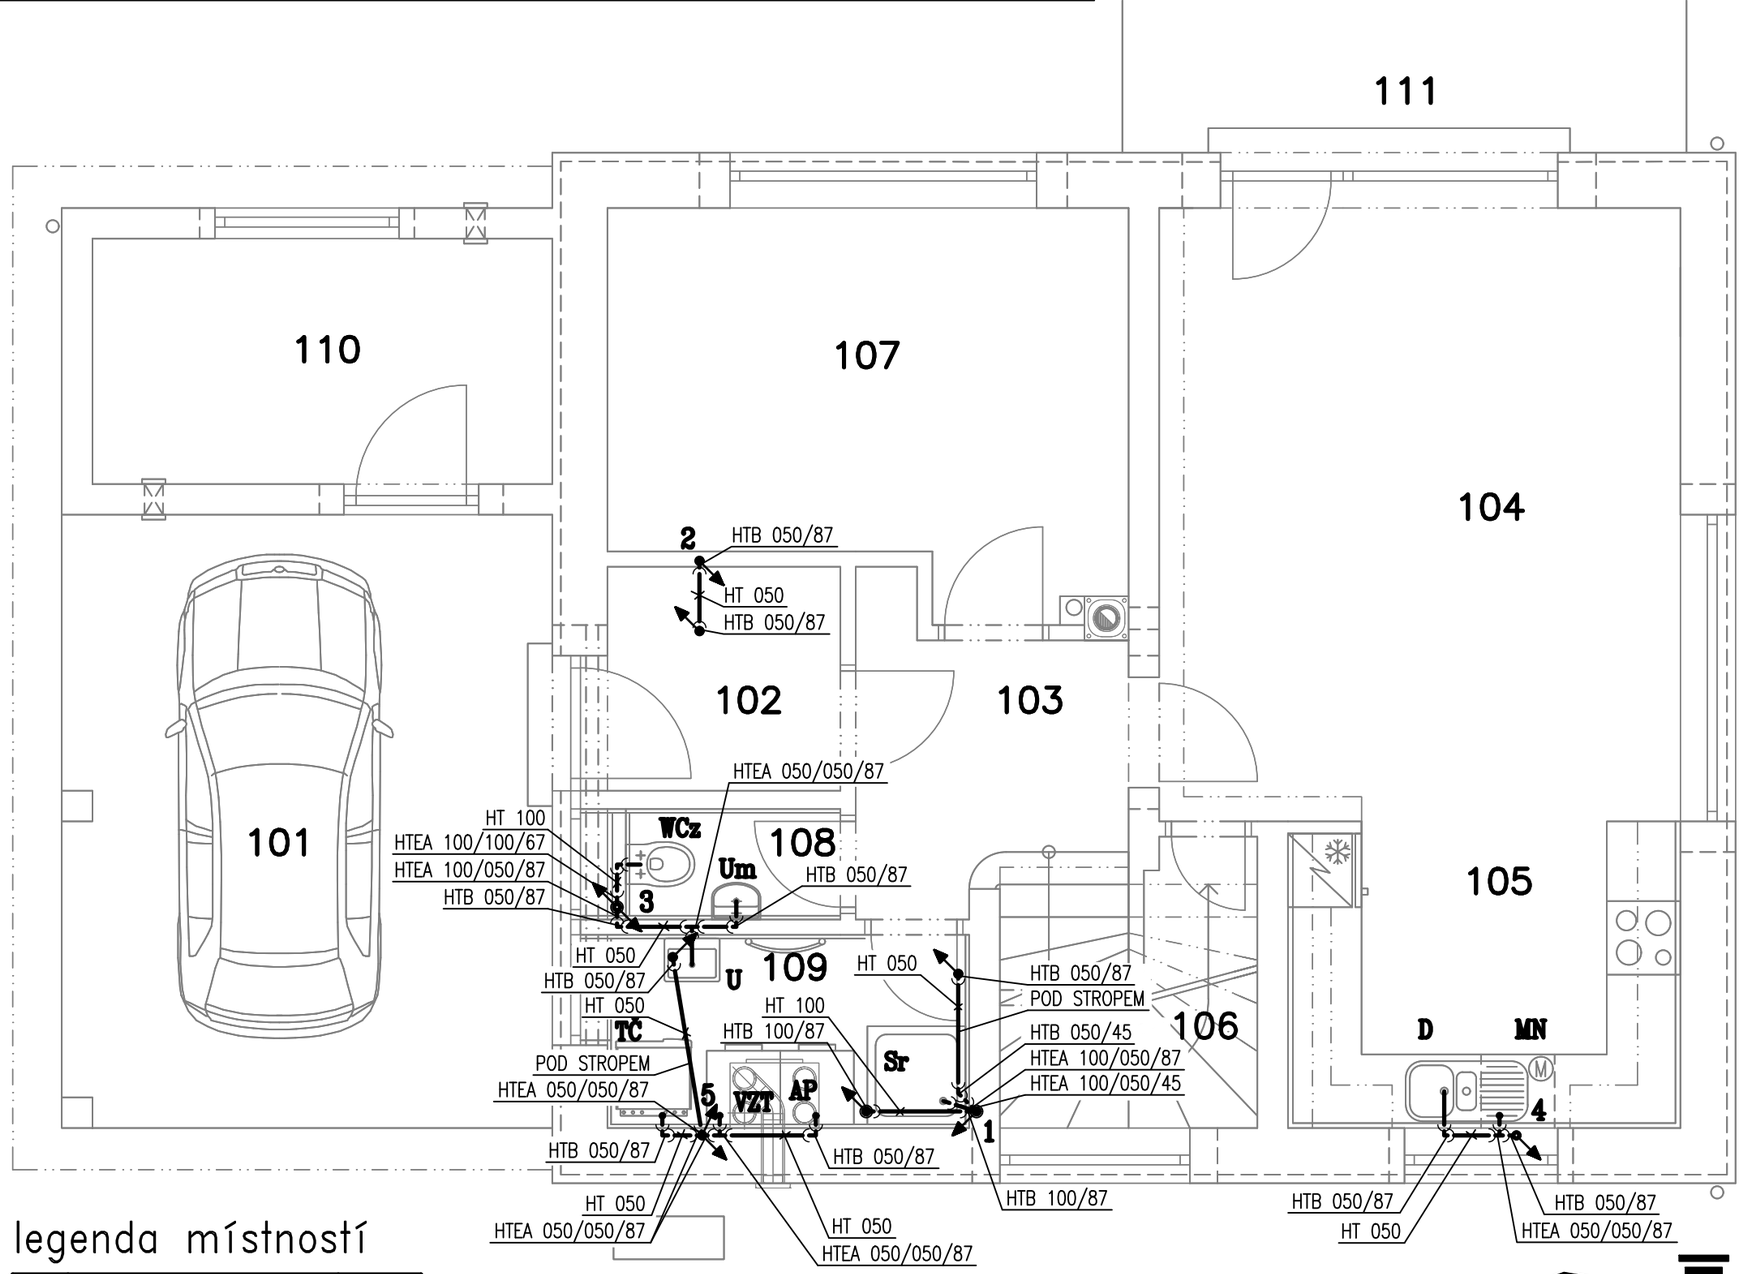



## legenda místností

| ČÍSLO | ÚČEL | PLOCHA ($m^2$) |
|---|---|---|
| 101 | ZÁVĚTŘÍ | 19,81 |
| 102 | ZÁDVEŘÍ | 3,51 |
| 103 | HALA | 4,67 |
| 104 | OBÝVACÍ POKOJ | 21,25 |
| 105 | KUCHYŇ | 7,94 |
| 106 | SPÍŽ | 3,34 |
| 107 | PRACOVNA | 12,72 |
| 108 | WC | 1,71 |
| 109 | SPRCHA + DOMÁCÍ PRÁCE | 4,65 |
| 110 | JÍZDNÍ KOLA, ZAHRADNÍ NÁŘADÍ | 7,50 |
| 111 | TERASA | 13,80 |

## legenda Z.T.I.

TČ

HT systém z PP
ležatá kanalizace – KG systém z PVC
tepelné čerpadlo NIBE
viz Vytápění

pokyny pro montáž – viz Technická zpráva
legenda zařizovacích předmětů
– viz Výpis zařizovacích předmětů

Paré číslo

THERMO PLUS
projektový ateliér

| | | |
|---|---|---|
| Hlavní projektant: Ing. Karel Peterka | Zodpovědný projektant: Ing. Karel Peterka | Vypracoval: Lukáš Materna |
| Místo: k.ú. Velká Hraštice, p.p.č. 91/48 | Stavebník: Ekaterina Matveeva, U Slovanky 2440/5C, Praha | |

Název akce:
# RODINNÝ DŮM "BEÁTA"

| | |
|---|---|
| Formát | 2xA4 |
| Datum | listopad 2021 |
| Stupeň PD | typový projekt |
| Č.zakázky | 030/21/TP |

Příloha:
ZDRAVOTNĚ TECHNICKÉ INSTALACE
## KANALIZACE – PŘÍZEMÍ

| Měřítko: | Č. přílohy: |
|---|---|
| – | D.1.4.Z.3 |