


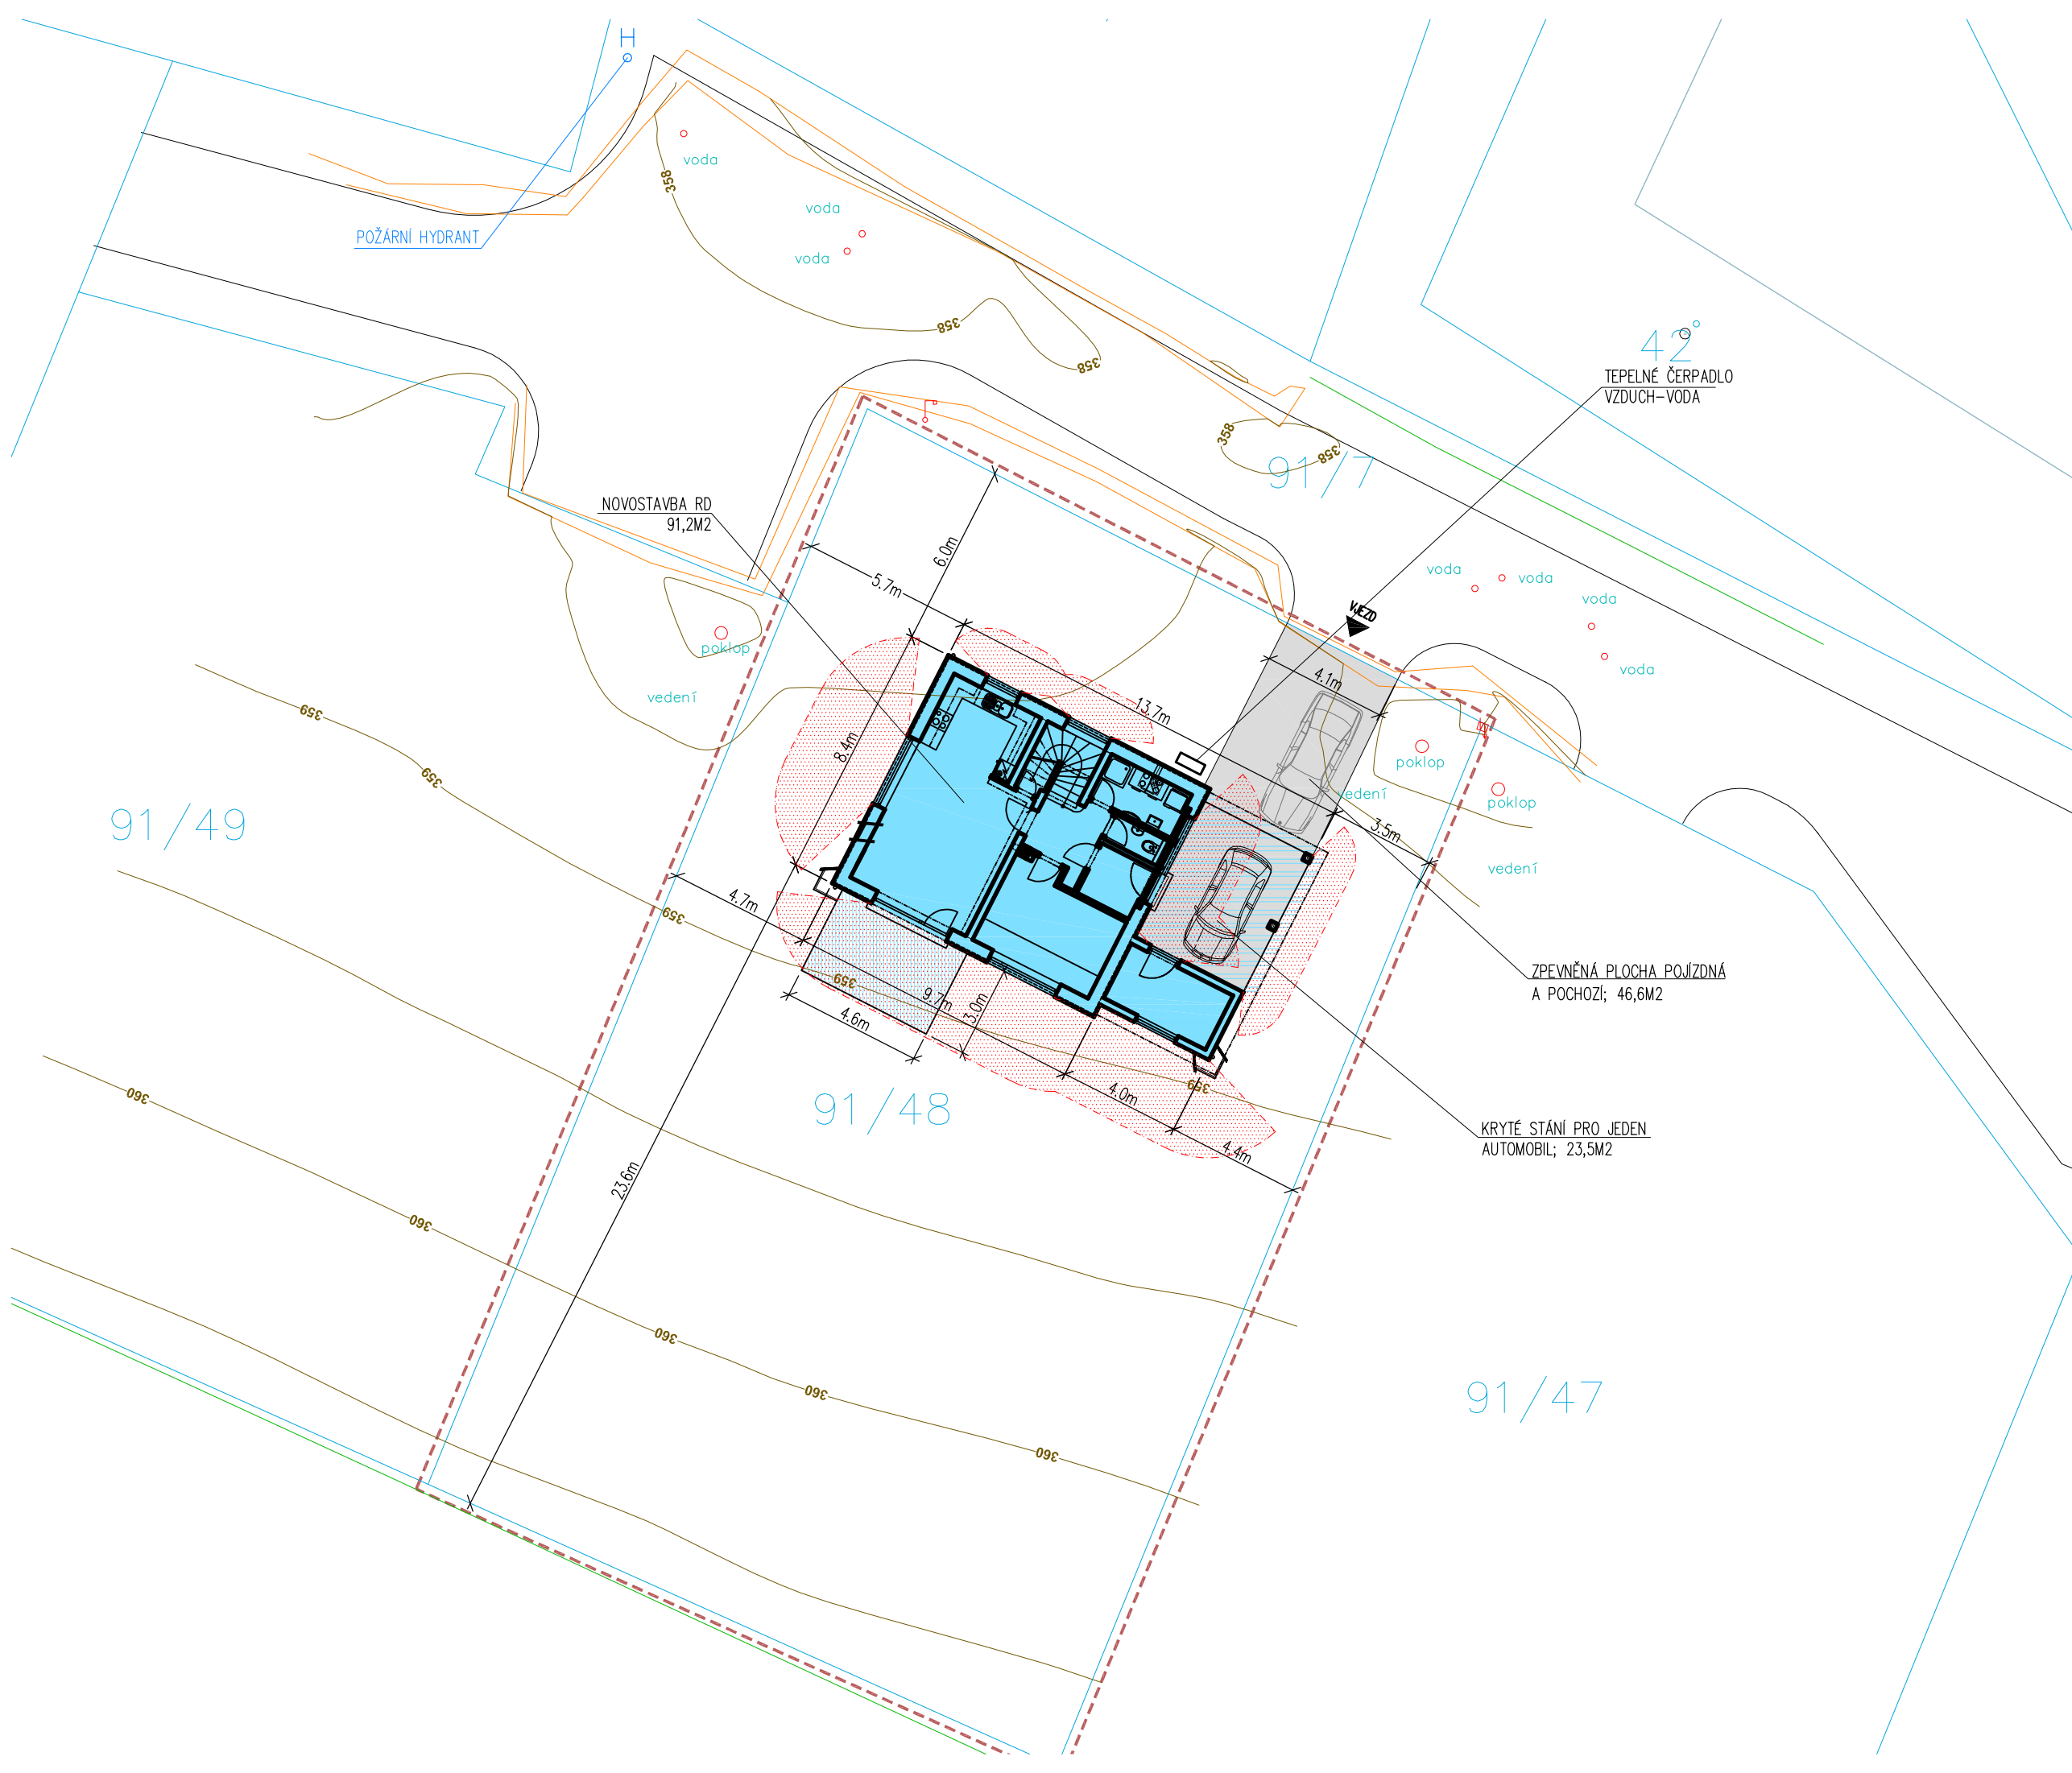

LEGENDA

- NOVÝ OBJEKT RD
- NOVÝ OBJEKT – KRYTÉ STÁNÍ
- NOVÝ OBJEKT – TERASA
- HRANICE KATASTRU
- ŘEŠENÉ ÚZEMÍ
- NOVÉ ZPEVNĚNÉ PLOCHY
- POŽÁRNĚ NEBEZPEČNÝ PROSTOR

S

± 0.000 = 359,200 m n.m. (BpV)

Tato dokumentace je duševním vlastnictvím f. PÍSEK SEYČEK ARCHITEKTI s.r.o.

STUPEN: DOKUMENTACE PRO SPOLEČNÉ ŘÍZENÍ	
Č. ZAKÁZKY:	PARÉ:
DATUM: PROSINEC 2021	
MĚŘÍTKO: 1:200	
FORMÁT: 2xA4	
ZODPOVĚDNÝ PROJEKTANT	písek seyček architekti
ING. ARCH. JAN SEYČEK	PISEK SEYČEK ARCHITEKTI S.R.O. KRÁSOVA 749/17, 130 00 PRAHA 3 TEL: +420 774 627 114, +420 606 427 854
VYPRACOVAL	PISEK SEYČEK ARCHITEKTI S.R.O. KRÁSOVA 749/17, 130 00 PRAHA 3 TEL: +420 774 627 114, +420 606 427 854
ING. JIŘÍ KLOFÁK	
INVESTOR: EKATERINA MATVEEVA U SILOVANKY 2440/5C, 182 00, PRAHA	
STAVBA: RODINNÝ DŮM "BEÁTA" K.Ú. VELKÁ HRAŠTICE PARC.Č. 91/48	
ČÁST DOKUMENTACE: POŽÁRNĚ BEZP. ŘEŠENÍ	Č. ČÁSTI: D.1.3
NÁZEV VÝKRESU: SITUACE	Č. VÝKRESU: 01