



ŘEZ ČERPACÍ JÍMKOU
měř. 1:25

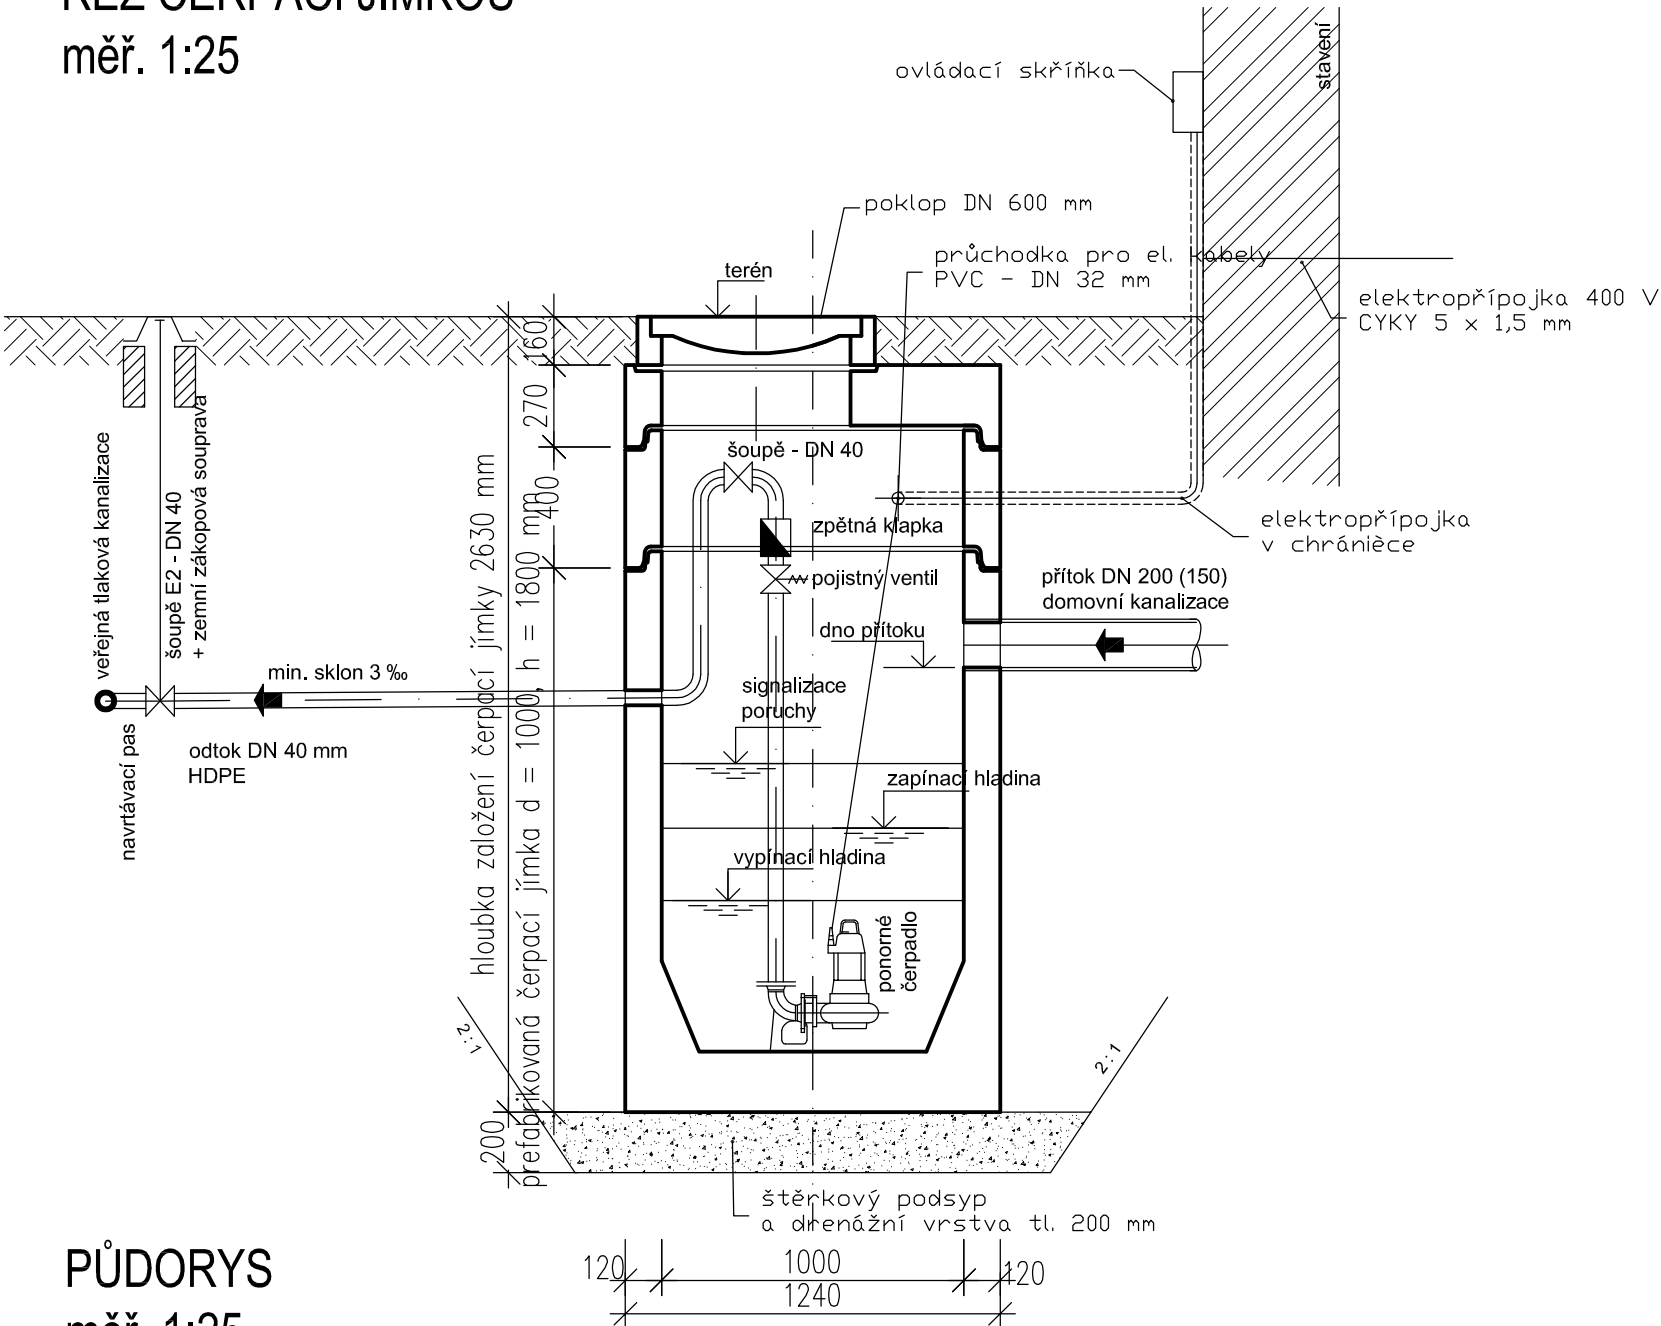

PŮDORYS
měř. 1:25

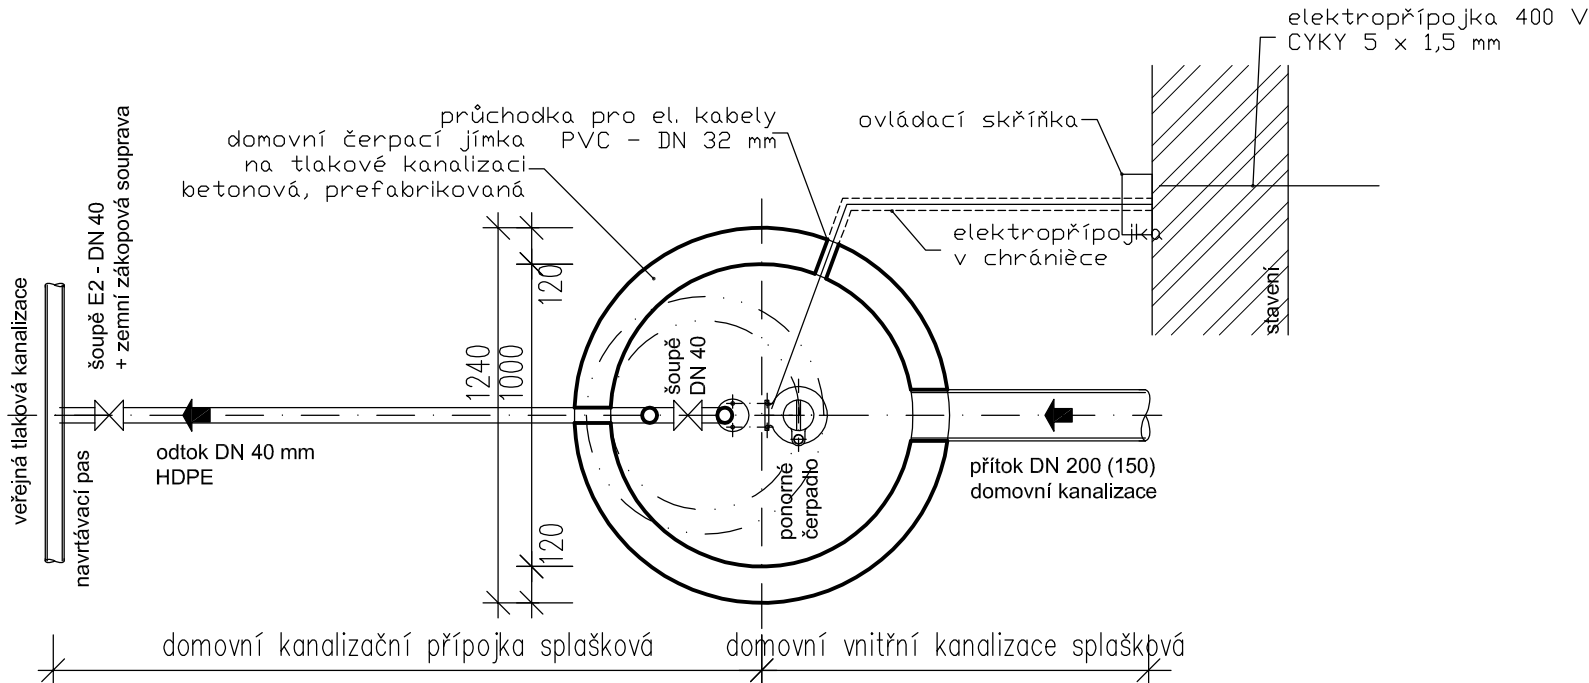

POZNÁMKA:

- ČERPACÍ JÍMKA MÁ MAXIMÁLNÍ KAPACITU 1,5M3, ČERPACÍ CYKLUS BUDE SPOUŠTĚN NA ÚROVNI 0,5 M3
- NA GRAVITAČNÍM POTRUBÍ BUDE UMÍSTĚNA ZPĚTNÁ Klapka
- JÍMKU JE MOŽNÉ REALIZOVAT I V PLASTOVÉM PROVEDENÍ

± 0.000 = 359,200 m n.m. (BpV)
Tato dokumentace je duševním vlastnictvím f. PÍSEK SEYČEK ARCHITEKTI s.r.o.

STUPEŇ: DOKUMENTACE PRO SPOLEČNÉ ŘÍZENÍ	
Č. ZAKÁZKY:	PARÉ:
DATUM: PROSINEC 2021	 písek seyček architekti
MĚŘITKO:	
FORMÁT:	
ZODPOVĚDNÝ PROJEKTANT	 PÍSEK SEYČEK ARCHITEKTI S.R.O. KORUNNÍ 810/104, 101 00 PRAHA 10 TEL: +420 774 627 114, +420 606 427 854
ING. ARCH. JAN SEYČEK	
VYPRACOVAL	
ING. JIŘÍ KLOFÁK	PÍSEK SEYČEK ARCHITEKTI S.R.O. KORUNNÍ 810/104, 101 00 PRAHA 10 TEL: +420 774 627 114, +420 606 427 854
INVESTOR: EKATERINA MATVEEVA U SILOVANKY 2440/5C, 182 00, PRAHA	
STAVBA: RODINNÝ DŮM "BEÁTA" K.Ú. VELKÁ HRAŠTICE PARC.Č. 91/48	
ČÁST DOKUMENTACE: TZB	Č. ČÁSTI: D.1.4.Z
NÁZEV VÝKRESU: DETAIL ČERPACÍ JÍMKY	Č. VÝKRESU: 20